



Lidl US, LLC  
3500 S. Clark St.  
Arlington , Virginia 22202  
P: (571) 398-5435

Project: 1517 Norcross GA - Jimmy Carter Blvd  
4990 Jimmy Carter Blvd  
Norcross, Georgia 30093

## Submittal #1-2.0 - Mast Arm Pole Shop Drawings #1,#2,#3 1 - Default Section

|                        |   |                   |                                                   |
|------------------------|---|-------------------|---------------------------------------------------|
| Revision               | 0   | Submittal Manager | Christopher Manes (21327198 CHA Consulting, INC.) |
| Status                 | Open   | Date Created      | Sep 18, 2026                                      |
| Issue Date             | Sep 18, 2026   | Spec Section      | 1 - Default Section                               |
| Responsible Contractor | Place Services Inc.   | Received From     | Tucker Teague (Place Services Inc.)               |
| Received Date          | Sep 25, 2026   | Submit By         | Sep 18, 2026                                      |
| Final Due Date         |   | Lead Time         |                                                   |
|                        |   | Cost Code         |                                                   |
| Location               |   | Type              | Shop Drawing                                      |
| Submittal Package      |   |                   |                                                   |
| Approvers              |   |                   |                                                   |
| Ball in Court          | Christopher Manes (21327198 CHA Consulting, INC.)   |                   |                                                   |
| Distribution           | Bobby McTeague (Place Services Inc.), Christopher Manes (21327198 CHA Consulting, INC.), JaWanna English-Neal (21327198 CHA Consulting, INC.), Jeff Belyea (21327198 CHA Consulting, INC.), Jens Byer (28101155 Lidl US, LLC), Luis Marcelino (Place Services Inc.), Todd Seldomridge (21327198 CHA Consulting, INC.), Tucker Teague (Place Services Inc.) |                   |                                                   |
| Description            | Place Services Inc. - No Exceptions Taken   |                   |                                                   |

### Submittal Workflow

| Name                               | Sent Date | Due Date | Returned Date | Response | Attachments                                                                        |
|------------------------------------|-----------|----------|---------------|----------|------------------------------------------------------------------------------------|
| General Information<br>Attachments |           |          |               |          | <a href="#">#1517 Lidl Norcross, GA - Mast Arm Pole Shop Drawings #1,#2,#3.pdf</a> |

Lidl 1517 Norcross, GA - Ground Up

4990 Jimmy Carter Blvd. Norcorss, GA 30093

Report generated by Tucker Teague (Place Services, Inc.)



Submittal #PSI-0006 - Shop Drawings for the Mast Arm Poles


|             |                                      |                  |            |
|-------------|--------------------------------------|------------------|------------|
| Creator     | Tucker Teague (Place Services, Inc.) | Submission due   | -          |
| Assignee    | Tucker Teague (Place Services, Inc.) | Response due     | 09/25/2026 |
| Reviewers   | -                                    | Closed on        | -          |
| Status      | Pending approval                     | Reference number | -          |
| Type        | Shop drawings                        | Specification    | -          |
| Description | -                                    |                  |            |

Approval (rev. 0)

|              |   |              |   |
|--------------|---|--------------|---|
| Responded by | - | Responded on | - |
| Response     | - |              |   |
| Notes        | - |              |   |
| Attachments  | - |              |   |

Submission (rev. 0)

|              |   |              |            |
|--------------|---|--------------|------------|
| Submitted by | Tucker Teague (Place Services, Inc.)   | Submitted on | 09/18/2026 |
| Notes        | Place Services Inc. - No Exceptions Taken   |              |            |
| Attachments  | PDF attachments are included in this export.<br><a href="#">↓ Mast Arm Pole Shop Drawings #1.pdf</a>   (Page 2) )<br><a href="#">↓ Mast Arm Pole Shop Drawings #2.pdf</a>   (Page 3) )<br><a href="#">↓ Mast Arm Pole Shop Drawings #3.pdf</a>   (Page 4) ) |              |            |


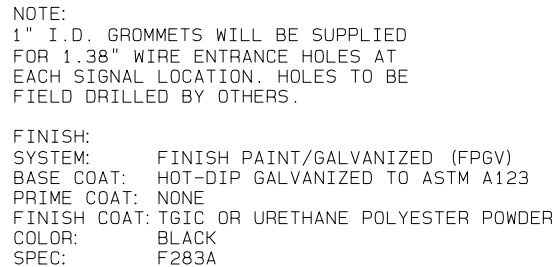


| MATERIAL DATA                            |                    |                  |  |                       |                  |                  |
|------------------------------------------|--------------------|------------------|--|-----------------------|------------------|------------------|
| COMPONENT                                | ASTM DESIGNATION   | MIN. YIELD (KSI) |  | COMPONENT             | ASTM DESIGNATION | MIN. YIELD (KSI) |
| TAPERED TUBES                            | A595 GR. A OR A572 | 55               |  | BASE PLATE            | A36              | 36               |
| ANCHOR BOLTS                             | F1554 GR.55        | 55               |  | SIGNAL ARM ATTACHMENT | A36              | 36               |
| NUTS AND BOLTS                           | A563, F436         |                  |  | SIG. ARM CONN. BOLTS  | A325             |                  |
| HARDWARE COATING                         | HOT DIP ZINC       |                  |  |                       |                  |                  |
|                                          |                    |                  |  |                       |                  |                  |
| HARDWARE $\leq$ 0.50" IS STAINLESS STEEL |                    |                  |  |                       |                  |                  |

THE MAJOR TRAFFIC STRUCTURES SHOWN ON THIS DRAWING HAVE BEEN DESIGNED IN ACCORDANCE WITH THE LRFD SPECIFICATIONS FOR STRUCTURAL SUPPORTS FOR HIGHWAY SIGNS, LUMINAIRES AND TRAFFIC SIGNALS, FIRST EDITION" SLTS-1. THE WIND LOADS WERE CALCULATED FROM AN ULTIMATE WIND VELOCITY OF 115 MPH WITH A MEAN RECURRENCE INTERVAL OF 700 YEARS, AND A FATIGUE CATEGORY OF 2. THE FATIGUE LOADS WERE CALCULATED ON THE REQUIREMENTS OF SECTION 11 OF THE CODE, AND THE FOLLOWING DESIGN CONDITIONS:

- STRUCTURES ARE DESIGNED TO RESIST NATURAL WIND GUSTS BASED ON THE YEARLY MEAN WIND VELOCITY OF 11.2 MPH.
- STRUCTURES ARE NOT DESIGNED TO RESIST GALLOPING-INDUCED CYCLIC LOADS.
- TRUCK-INDUCED GUST LOADS ARE NOT INCLUDED PER THE REQUIREMENTS OF THE CODE.

AASHTO 2015 SPECIFICATIONS

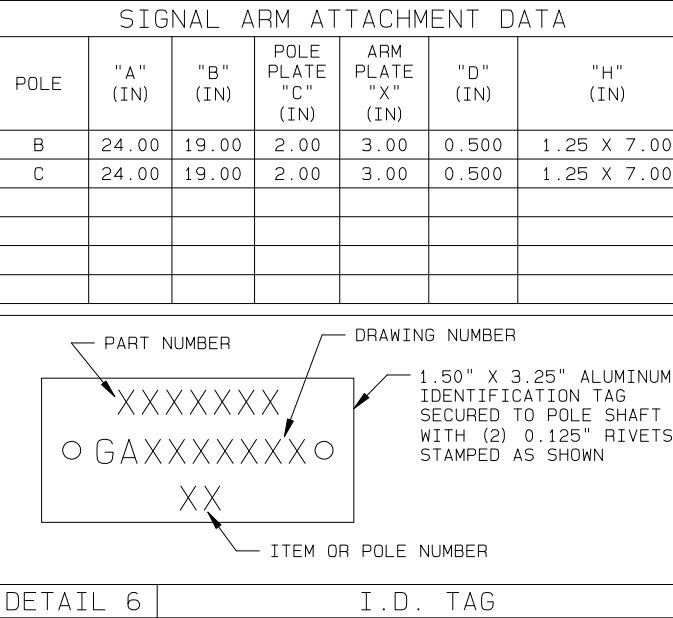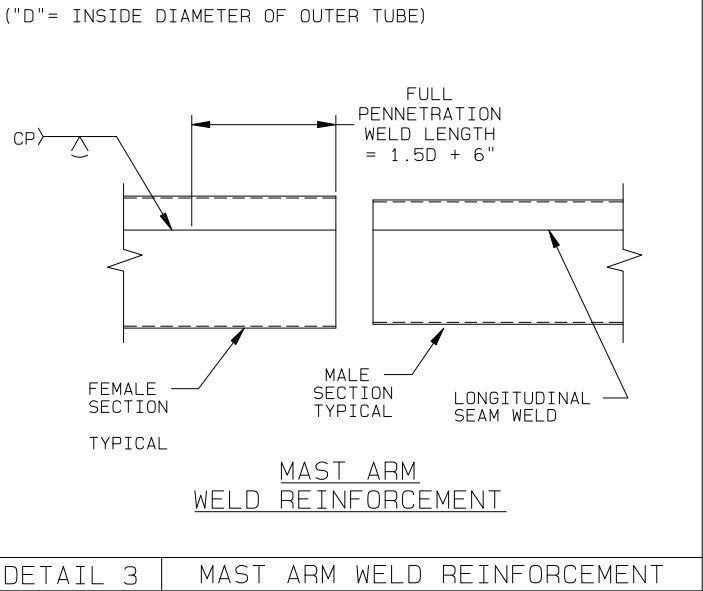

**SHOP DRAWING /  
SUBMITTAL REVIEW**

☒ NO EXCEPTION TAKEN  
☐ REVISE AND RESUBMIT  
☐ MAKE CORRECTIONS NOTED  
☐ REJECTED

SUBMITTAL WAS REVIEWED FOR DESIGN  
 CONFORMITY AND GENERAL CONFORMANCE TO  
 CONTRACT DOCUMENTS ONLY. THE CONTRACTOR IS  
 RESPONSIBLE FOR CONFIRMING AND CORRELATING  
 INFORMATION AT JOBSITE FOR TOLERANCE,  
 CLEARANCE, QUANTITIES, FABRICATION PROCESSES  
 AND TECHNIQUES OF CONSTRUCTION,  
 COORDINATION WITH WORK OF OTHER TRADES  
 AND FULL COMPLIANCE WITH CONTRACT  
 DOCUMENTS.

By: **Tucker Teague**  
 Date: **9/18/2026**

**Place Services, Inc**  
 Canton, GA 30115




Digitally signed by  
Nizam A Qassem  
Date: 2026-08-31  
16:11-05:00

|     |               |               |             |                                     |       |                                                         |   |   |                         |     |
|-----|---------------|---------------|-------------|-------------------------------------|-------|---------------------------------------------------------|---|---|-------------------------|-----|
|     |               |               |             | SOLD TO: DOT LIGHTING, LLC          | JOB   | GWINNETT COUNTY, GEORGIA<br>JIMMY CARTER BLVD/SHELBY DR | VALMONT INDUSTRIES, INC. RESERVES<br>THE RIGHT TO INSTALL VARIOUS,<br>ENGINEER APPROVED, MATERIAL HANGING<br>ACCOMMODATIONS TO FACILITATE THE<br>MANUFACTURING PROCESS. | <br>Valley.NE 68064<br>(402) 359-2201 | ORDER NUMBER: 672263-P1 |     |
|     |               |               |             | SHIP TO: R.J. HAYNIE AND ASSOCIATES |       |                                                         |   |   | PAGE NUMBER: 1 OF 2     |     |
|     |               |               |             | P.O. #: 2023                        | TITLE | TRAFFIC SIGNAL STRUCTURES                               |   |   | DRAWING NUMBER          | REV |
|     |               |               |             | AGENT: TRAFFIC & LIGHTING CORP      |       |                                                         |   |   | GA672263P1              |     |
| —   | NKL 08/25/26  | NKL 08/25/26  | -----       |                                     |       |                                                         |   |   |                         |     |
| REV | DRAWN BY-DATE | CHECK BY-DATE | DESCRIPTION |                                     |       |                                                         |   |   |                         |     |


[illegible]

3'-0" Dia x 14'-6" Deep - (8) #10 Rebar

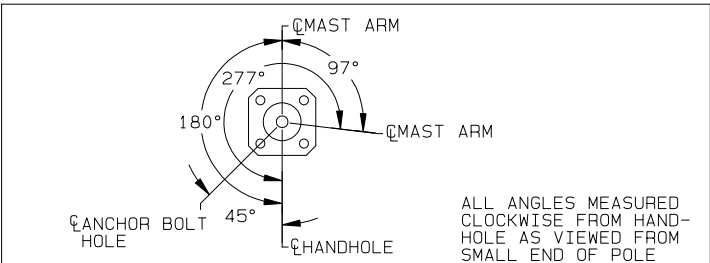

POLE C - RADIAL INDEX

| WELD SIZE TABLE |     |        |     |       |     |        |
|-----------------|-----|--------|-----|-------|-----|--------|
| TUBE THICKNESS  | a   |        | b   |       | c   |        |
| 11 GA (0.1196") | .12 | 7/64"  | .19 | 3/16" | .31 | 5/16"  |
| 7 GA (0.1793")  | .18 | 11/64" | .25 | 1/4"  | .44 | 7/16"  |
| 5 GA (0.2092")  | .21 | 13/64" | .31 | 5/16" | .56 | 9/16"  |
| 3 GA (0.2391")  | .24 | 15/64" | .31 | 5/16" | .56 | 9/16"  |
| 0.219"          | .22 | 7/32"  | .31 | 5/16" | .56 | 9/16"  |
| 0.250"          | .25 | 1/4"   | .31 | 5/16" | .56 | 9/16"  |
| 0.313"          | .31 | 5/16"  | .38 | 3/8"  | .69 | 11/16" |

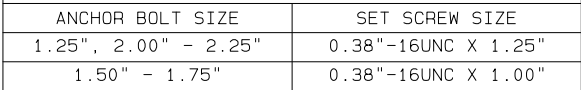

|       |                                                         |
|-------|---------------------------------------------------------|
| JOB   | GWINNETT COUNTY, GEORGIA<br>JIMMY CARTER BLVD/SHELBY DR |
| TITLE | TRAFFIC SIGNAL STRUCTURES                               |

**valmont**   
Valley, NE 68064  
(402) 359-2201

|                         |      |
|-------------------------|------|
| ORDER NUMBER: 672263-P1 |      |
| PAGE NUMBER: 2          | OF 2 |
| DRAWING NUMBER          | REV  |
| GA672263P1              |      |

T.S. #082

Jimmy Carter Blvd

Shelby Dr.

Gwinnett Co.

Anchor bolts in line  
with this mast arm




SS'

Jimmy Carter Blvd

SS'

65'

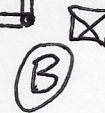

Shelby Dr

**SHOP DRAWING /  
SUBMITTAL REVIEW**

- ☒ NO EXCEPTION TAKEN
- ☐ REVISE AND RESUBMIT
- ☐ MAKE CORRECTIONS NOTED
- ☐ REJECTED

SUBMITTAL WAS REVIEWED FOR DESIGN  
CONFORMITY AND GENERAL CONFORMANCE TO  
CONTRACT DOCUMENTS ONLY. THE CONTRACTOR IS  
RESPONSIBLE FOR CONFIRMING AND CORRELATING  
DIMENSIONS AT JOBSITE FOR TOLERANCE,  
CLEARANCE, QUANTITIES, FABRICATION PROCESSES  
AND TECHNIQUES OF CONSTRUCTION,  
COORDINATION OF HIS WORK WITH OTHER TRADES  
AND FULL COMPLIANCE WITH CONTRACT  
DOCUMENTS.

By: Tucker Teague

Date: 9/18/2026

Place Services, Inc  
Canton, GA 30115