

NOTE: This is a standard symbol list and not all items listed may be used

Connections / Equipment

Connections / Equipment		Telephone Utility Pole	
	COMBINATION ADJUSTABLE FREQUENCY DRIVE WITH SAFETY DISCONNECT SWITCH		TELEPHONE TRANSFORMER PAD/VAULT
	COMBINATION MOTOR STARTER/FUSED DISCONNECT SWITCH	Raceways	
	CONTACTOR COIL		CABLE RUNWAY, WIRE MESH BASKET TYPE, WIDTH AS INDICATED
	HEAVY DUTY FUSED DISCONNECT SWITCH		EXISTING CONDUIT CONCEALED IN WALL OR CEILING SPACE
	MOTOR CONNECTION		EXISTING CONDUIT ROUTED BELOW FLOOR / GRADE
	NON-FUSED DISCONNECT SWITCH		OVERHEAD PRIMARY SERVICE
	RELAY		OVERHEAD TELEPHONE SERVICE
	REMOTE DRIVER FOR LED LUMINAIRES		SOLID BOTTOM CABLE RUNWAY (WHITE COLOR), WIDTH AS INDICATED
	TRANSFORMER		UNDERGROUND CABLE TELEVISION SERVICE
	FIRE SMOKE DAMPER		UNDERGROUND PRIMARY SERVICE
	SMOKE DAMPER		UNDERGROUND SECONDARY SERVICE
	CEILING MOUNTED JUNCTION BOX		UNDERGROUND TELEPHONE SERVICE
	FLOOR MOUNTED JUNCTION BOX		CONDUIT CONCEALED IN WALL OR CEILING SPACE
	WALL-MOUNTED JUNCTION BOX		CONDUIT ROUTED BELOW FLOOR / GRADE
Fire Alarm			CONDUIT ELLED DOWN
	FIRE ALARM CONTROL PANEL		CONDUIT ELLED UP
	NOTIFICATION APPLIANCE CIRCUIT PANEL		CONDUIT/WIRING CONTINUATION
	FIRE ALARM ANNUNCIATOR PANEL		CONDUIT/WIRING STUBBED OUT WITH END CAP OR INSULATED PLASTIC BUSHING
	PULL STATION		FLEXIBLE CONDUIT
	REMOTE TEST SWITCH	Switches and Receptacles	
	SMOKE DETECTOR		COMBINATION COMMUNICATIONS OUTLET AND DOUBLE DUPLEX RECEPTACLE, FLUSH FLOOR
	SMOKE DETECTOR, DUCT MOUNTED		DUPLEX RECEPTACLE (MULTIPLE LETTERS INDICATE MULTIPLE OPTIONS) G = GFCI PROTECTED WP = WEATHERPROOF CONTINUOUS USE COVER, GFCI PROTECTED, WITH- A = ABOVE COUNTER
	SPRINKLER FLOW SWITCH WITH INPUT MODULE		DUPLEX RECEPTACLE, FLUSH FLOOR
	SPRINKLER TAMPER SWITCH WITH INPUT MODULE		(G) DOUBLE DUPLEX RECEPTACLE, FLUSH FLOOR
	CEILING MOUNTED HORN/STROBE COMBINATION (# INDICATES MINIMUM C/		DOUBLE DUPLEX RECEPTACLE. SEE LETTER CODE LIST AT DUPLEX RECEPTACLE
	STROBE, CEILING MOUNTED (# INDICATES MINIMUM CANDELA RATING)		SINGLE RECEPTACLE, FLUSH FLOOR
	WALL MOUNTED HORN/STROBE COMBINATION		SINGLE RECEPTACLE. SEE LETTER CODE LIST AT DUPLEX RECEPTACLE FOR OPT
	ADDRESSABLE MONITOR MODULE		EQUIPMENT ELECTRICAL CONNECTION
	ADDRESSABLE RELAY MODULE		SPECIAL PURPOSE RECEPTACLE. LETTER CODE DENOTES RECEPTACLE CONFIGU X = COORDINATE RECEPTACLE CONFIGURATION WITH EQUIPMENT BEING
	WATER FLOW ALARM BELL FURNISHED BY DIV.13 WIRED TO FIRE ALARM S		PENDANT RECEPTACLE WITH CORD GRIPS. VERIFY PENDANT LENGTH. SEE LETTE
General			CEILING MOUNTED OCCUPANCY SENSOR V (LOWER CASE) = VACANCY CONTROL DESIGNATION
	DETAIL NUMBER AND SHEET LOCATION		WALL MOUNTED OCCUPANCY SENSOR V (LOWER CASE) = VACANCY CONTROL DESIGNATION
	EQUIPMENT IDENTIFICATION		WALL MOUNTED OCCUPANCY SENSOR/SWITCH V (LOWER CASE) = VACANCY CONTROL DESIGNATION
	FOOD SERVICE EQUIPMENT / CALCULATION TAG		MULTIPLE CHANNEL SURFACE METAL RECEPTACLE RACEWAY WITH LOW VOLTAGE
	KEYED NOTE		SURFACE METAL RECEPTACLE RACEWAY
	POINT OF CONNECTION		PHOTO ELECTRIC SWITCH S = SWITCHED PHOTOCELL
	SECTION NUMBER AND SHEET LOCATION		SINGLE POLE SWITCH K = KEYED SWITCH, OS = OCCUPANCY SENSOR SWITCH
	DEMOLISH		
	EXISTING WORK		
	NEW WORK		
Lighting			
	A TYPE LINEAR LIGHT FIXTURE		
	A TYPE SPOT/LIGHT FIXTURE		
	EXIT SIGN CEILING MOUNTED, ARROW(S) INDICATES DIRECTION IF SHOWN		
	EXIT SIGN WALL MOUNTED, ARROW(S) INDICATES DIRECTION IF SHOWN		
	WALL MOUNTED LUMINAIRE		

#10 B-27,29,31	BRANCH CIRCUIT WIRING. ARROW INDICATES HOME RUN TO PANEL WITH CIRCUITS AS NOTED. WIRE SIZE IS #12 AWG MINIMUM UNLESS NOTED OTHERWISE. SHORT TICK MARKS INDICATE PHASE CONDUCTORS. LONG TICK MARKS INDICATE NEUTRAL CONDUCTORS. A SINGLE CURVED TICK MARK INDICATES INSULATED GREEN GROUND CONDUCTOR. SECOND CURVED TICK MARK INDICATES "ISOLATED GROUND" (GREEN INSULATION WITH YELLOW STRIPE) CONDUCTOR.
	BRANCH PANEL
	CIRCUIT BREAKER
	DRY TYPE TRANSFORMER
	FLUSH MOUNT EQUIPMENT ENCLOSURE AS NOTED
	FLUSH WALL MOUNTED BRANCH PANEL
	GROUND BAR
	GROUNDING POINT
	MAIN DISTRIBUTION PANEL / SUB DISTRIBUTION PANEL
	POWER POLE
	SURFACE MOUNT EQUIPMENT ENCLOSURE AS NOTED

D. DO NOT COMMENCE INSTALLATION OF ELECTRICAL SYSTEMS AND EQUIPMENT WITHOUT RELATED SHOP DRAWING APPROVALS.

B. "FURNISH" MEANS TO "SUPPLY" AND USUALLY REFERS TO DELIVERY OF AN ITEM OF EQUIPMENT TO THE PROJECT SITE, READY FOR INSTALLATION. EQUIPMENT TO THE PROJECT SITE DOES NOT INCLUDE DELIVERY OR INSTALLATION OF THE EQUIPMENT TO ITS PLACE IN FULL OPERATIONAL ORDER. PROVIDE" MEANS TO "FURNISH" AND "INSTALL." "FUTURE," BY OTHERS, (REFER DISCIPLINE) DIVISION" AND SIMILAR EXPRESSIONS INDICATE WORK THAT MAY BE PERFORMED UNDER THE CONTRACT DOCUMENTS BUT, NOT NECESSARILY UNDER THE DIVISION OR DISCIPLINE ON WHICH THE NOTE APPEARS. THE CONTRACTOR SHALL BE RESPONSIBLE FOR COORDINATING THE WORK WITH SUPPLIERS, SUBCONTRACTORS, MANUFACTURERS, ETC. THE CONTRACTOR SHALL BE RESPONSIBLE FOR THE WORK TO BE REQUIRED, CONTACT THE ARCHITECT/ENGINEER PRIOR TO SUBMITTING BID.

C. THE WORK SHALL COMPLY WITH LATEST CODE. THIS WOULD INCLUDE, BUT IS NOT LIMITED TO THE INTERNATIONAL BUILDING CODE (IBC) AND THE NATIONAL BUILDING CODE (NEC), AMENDMENTS, NFPA, ANSI, OSHA, AND ALL OTHER LOCAL OR MUNICIPAL BUREAUS AND AGENCIES. THE CONTRACTOR SHALL VERIFY THE CODES AND SPECIFICATIONS OF THESE CONTRACT DOCUMENTS NOT WITHSTANDING. THIS SHALL NOT BE CONSTRUED AS WAIVING COMPLIANCE WITH ANY REQUIREMENTS OF THE PLANS AND SPECIFICATIONS WHICH MAY BE IN EXCESS OF ANY REQUIREMENTS OF THESE CODES.

D. PROVIDE SUITABLE ANCHORAGE AND SUPPORT FOR ELECTRICAL EQUIPMENT IN RATED WALLS, CEILING, FLOORS AND CEILING. PROVIDE DEVICES AND RACEWAYS IN ACCORDANCE WITH ESTABLISHED CODES AND SPECIFICATIONS.

E. REFER TO SPECIFICATIONS FOR ADDITIONAL REQUIREMENTS. DRAWINGS AND SPECIFICATIONS COMPLEMENT EACH OTHER. REQUIREMENT BY EITHER INFERS REQUIREMENT BY BOTH. CONTRACTOR SHALL CAREFULLY COMPARE THE DRAWINGS AND SPECIFICATIONS, CHECK FOR CONFLICTS AND DISCREPANCIES UNDER WHICH CONSTRUCTION IS TO BE IMPLEMENTED. FOR CLARIFICATION BETWEEN VARIOUS DRAWINGS AND/OR SPECIFICATIONS, THE DISPUTED ISSUE SHALL BE REFERRED TO THE ENGINEER BEFORE ANY WORK IS COMPLETED. THE CONTRACTOR SHALL BE RESPONSIBLE FOR ANY EXCEPTIONS NECESSARY TO MAKE THIS WORK A COMPLETE AND READY-TO-USE INSTALLATION. IF NOT SO-STATED IN THE CONTRACTOR'S PROPOSAL, ANY SUCH WORK WILL NOT BE CONSIDERED ADDITIONAL.

F. CONTRACTOR SHALL CAREFULLY EXAMINE THE CONTRACT DOCUMENTS, VISITING THE SITE, TAKE THE PREMISES AND MAKE A THOROUGH SURVEY OF THE CONDITIONS UNDER WHICH CONSTRUCTION WILL BE IMPLEMENTED. THE SUBMISSION OF A PROPOSAL WILL BE CONSTRUED AS EVIDENCE THAT SUCH AN EXAMINATION HAS BEEN MADE. FAILURE TO DO SO SHALL BE CONSIDERED ACCEPTANCE OF THE OBLIGATIONS OF THE CONTRACT. ANY LATER CLAIMS FOR LABOR, EQUIPMENT, OR MATERIALS REQUIRED FOR DIFFICULTIES ENCOUNTERED WHICH COULD HAVE BEEN FORESEEN HAD SUCH AN EXAMINATION BEEN MADE, WILL NOT BE RECOVERED.

G. THE CONTRACTOR SHALL CURRY, OBTAIN AND PAY FOR ALL PERMITS, INSPECTIONS, AXES, LICENSE, AND FEES TO ALL GOVERNMENT AGENCIES REQUIRED FOR THE EXECUTION AND COMPLETION OF THE ELECTRICAL WORK. SCHEDULING OF ALL REQUIRED INSPECTIONS SHALL BE THE RESPONSIBILITY OF THE CONTRACTOR. CONTRACTOR SHALL PREPARE AND SUBMIT ALL REQUIRED DRAWINGS AND PERMITS TO THE GOVERNMENTAL AGENCIES AND UTILITY COMPANIES FOR THEIR APPROVAL.

H. CONNECT EQUIPMENT AND DEVICES FURNISHED UNDER OTHER DIVISIONS OF THIS CONTRACT BY OWNER OR BY OTHER CONTRACTS.

I. UNLESS OTHERWISE NOTED, PROVIDE CONCEALED AND FLUSH MOUNTED INSTALLATION OF DEVICES AND EQUIPMENT IN AREAS.

J. ELECTRICAL DRAWINGS ARE DIAGRAMMATIC IN NATURE AND SHALL NOT BE SCALED. TO THIS EXTENT, DATA GIVEN ON THE DRAWINGS IS AS EXACT AS COULD BE SECURED. THE CONTRACTOR SHALL COORDINATE THE EXACT LOCATION OF ALL REQUIRED WORK AND EQUIPMENT WITH THE OTHER TRADES. WHERE THERE ARE POTENTIAL CONFLICTS, THE CONTRACTOR SHALL OBTAIN AND VERIFY EXACT LOCATIONS, MEASUREMENTS, LEVELS, SPACE REQUIREMENTS, ETC. AT THE SITE AND SHALL SATISFACTORILY ADAPT HIS WORK TO ACTUALLY EXISTING CONDITIONS. REFLECT THE ACTUAL POSITIONING OF ALL OTHER TRADES, ELEVATIONS AND DETAILS INDICATING THE LOCATIONS OF CEILING ELEMENTS (E.G., LIGHTS, SPRINKLERS, DIFFUSERS, ETC.) AND WALL ELEMENTS. CEILING MOUNTED ITEMS SHALL BE INSTALLED IN ACCORDANCE WITH THE ARCHITECTURAL REFLECTED CEILING PLANS. IF A LOCATION FOR AN ITEM IS NOT SHOWN ON THE ARCHITECTURAL DRAWINGS, VERIFY THE EXACT LOCATION OF THE ITEM WITH THE ARCHITECT PRIOR TO INSTALLATION. THESE REQUIREMENTS APPLY TO ALL CEILING ELEMENTS.

K. THE CONTRACTOR SHALL PROVIDE TEMPORARY POWER AND LIGHTING FOR THIS WORK DURING CONSTRUCTION. TEMPORARY LIGHTING SHALL AT LEAST BE THE EQUAL OF (1100-WATT FIXTURE EVERY 100 SQUARE FEET, WITH A MINIMUM ONE FIXTURE PER ROOM. TEMPORARY LIGHTING SHALL BE LEFT IN PLACE UNTIL PERMANENT LIGHTING IS COMPLETELY INSTALLED. THE CONTRACTOR SHALL COORDINATE TEMPORARY LIGHTING WITH OTHER TRADES AND PROVIDE ADEQUATE PROVISIONS. THE CONTRACTOR SHALL PERFORM ALL COORDINATION WITH THE OWNER AND/OR LANDLORD AND UTILITY COMPANY.

L. PROVIDE SEPARATE EQUIPMENT GROUNDING CONDUCTOR IN 120 VOLT, MULTI-WIRE CIRCUITS.

M. RUN ELECTRICAL CONDUIT CONCEALED AND PARALLEL TO BUILDING LINES. VERIFY WITH ARCHITECT.

N. INSTALL COMPLETE SYSTEM OF CONDUCTORS IN RACEWAY SYSTEM THROUGHOUT BUILDING FOR FEEDERS, BRANCH CIRCUITS, ETC.

O. INSTALLATION OF UTILITY TRANSFORMER, UTILITY SERVICE CONDUITS, VAULTS, GROUNDING, ETC., SHALL BE VERIFIED AND COORDINATED WITH UTILITY COMPANY PRIOR TO INSTALLATION. CONTRACTOR SHALL OBTAIN ALL NECESSARY PERMITS AND APPROVALS FROM THE UTILITY COMPANY. THE PROPOSED UTILITY COMPANY TRANSFORMER LOCATION, SERVICE FEEDER ROUTING, VAULT LOCATION AND SIZE ARE SUBJECT TO UTILITY COMPANY ENGINEERING. CONTRACTOR SHALL OBTAIN ALL NECESSARY PERMITS AND APPROVALS FROM THE UTILITY COMPANY. UTILITY REQUIREMENTS FOR THIS PROJECT WITH UTILITY COMPANY PRIOR TO COMMENCING WORK.

P. ALL WORK ON SERVICE CONDUCTORS, FEEDERS, AND OTHER SUCH EQUIPMENT SHALL BE DONE ONLY WHEN SUCH CONDUCTORS, FEEDERS, AND EQUIPMENT ARE DE-ENERGIZED. THE CONTRACTOR SHALL FOLLOW THE OSHA SAFETY AND LOCK-OUT/TAG-OUT PROCEDURE IN PLACE PRIOR TO COMMENCEMENT OF WORK.

Q. ELECTRICAL CONTRACTOR SHALL COORDINATE ALL CONDUIT TRENCHING WITH OTHER DISCIPLINES AND THE UTILITY COMPANY TO AVOID CONFLICT.

R. MINIMUM SIZE FOR EXTERIOR BELOW GRADE CONDUIT SHALL BE 1".

S. OCCUPANCY SENSOR NOTES:
1. SENSOR SHALL BE INSTALLED EARLY VIEW OF OCCUPANTS, WHERE SENSOR WILL BE BLOCKED, SUBSTITUTE WITH SMALL ROOM CEILING SENSOR.
2. SEE MANUFACTURER'S SPECIFICATION REGARDING PLACING SENSORS AWAY FROM STRONG AIR-FLOW, INDICATE PRECISE LOCATION OF EACH CEILING SENSOR WHERE DRAWINGS INDICATE AIR SUPPLIES.
3. IN DRAWING ROOMS WITH CEILING SENSORS AND DUAL-LEVEL LIGHTING, ASSUME TWO TOGGLE SWITCH OVERRIDES PER SENSITIVE.

T. PROVIDE MACHINE-PRINTED, PRESSURE SENSITIVE, ABRASION RESISTANT LABEL TAPE ON BACK OF ALL SWITCH AND RECEPTACLE PLATES TO IDENTIFY THE PANELBOARD AND CIRCUIT BREAKER FOR WHICH THE LABEL IS SERVED. FOR LABELING OF UPS CIRCUITS, USE 1/2" BLACK ON WHITE TAPE 14PT FONT.

5/27/2025 5:00:30 PM Autodesk Docs/179550191-Lidl 1517 Norcross GA/79550191 Lidl 1517 NORCROSS GA- ELEC-04

LIDL ELECTRICAL SITE PLAN


THIS DOCUMENT AND ITS CONTENTS ARE THE PROPERTY OF PROGRESSIVE ARCHITECTURE & PLANNING, LLC. NO PART OF THIS DOCUMENT MAY BE REPRODUCED OR TRANSMITTED IN ANY FORM OR BY ANY MEANS, ELECTRONIC OR MECHANICAL, WITHOUT PERMISSION IN WRITING FROM PROGRESSIVE ARCHITECTURE & PLANNING, LLC. ALL RIGHTS ARE RESERVED. OTHER RIGHTS MAY BE RESERVED BY THIRD PARTIES. OTHER RIGHTS RESERVED, INCLUDING THE COPYRIGHT NOTICE.

GENERAL SHEET NOTES

- REFER TO SHEET E000 FOR LEGENDS, ABBREVIATIONS AND GENERAL NOTES.
- ALL SITE LIGHTING AND STORE SIGNAGE SHALL BE CONTROLLED BY LIGHTING CONTACTOR VIA BMS.
- ALL UNDERGROUND CONDUIT SHALL BE 1" C SCHEDULE 40 PVC MINIMUM. INSTALLED BELOW FINISH GRADE.
- REFER TO CIVIL SITE LIGHTING DRAWINGS FOR LIGHT FIXTURE SCHEDULE, EXACT LOCATION, FIXTURE TYPE, MOUNTING HEIGHT, AND POLE REQUIREMENTS.
- REFER TO CIVIL SITE PLAN FOR TRANSFORMER EXACT LOCATION.
- ELECTRICAL CONTRACTOR SHALL COORDINATE WITH POWER UTILITY COMPANY AND AHJ IN ORDER TO COMPLY WITH TRANSFORMER CLEARANCE REQUIREMENTS.
- ALL EXTERIOR WIRING, CURRENT CARRYING CONDUCTORS SHALL BE #8 CU. AWG. MINIMUM.

SHEET KEYNOTES

- PYLON SIGNAGE. PROVIDE CONNECTION TO 1" RGS ELBOW IN SIGN FOUNDATION. MAKE FINAL CONNECTION TO SIGNAGE POWER IN POLE BASE.
- SIEMENS VERSICHARGE AC SERIES ELECTRIC VEHICLE CHARGER PROGRAMMED TO 32A CURRENT SETTING. 2 #4, #8 GND, 1" C.

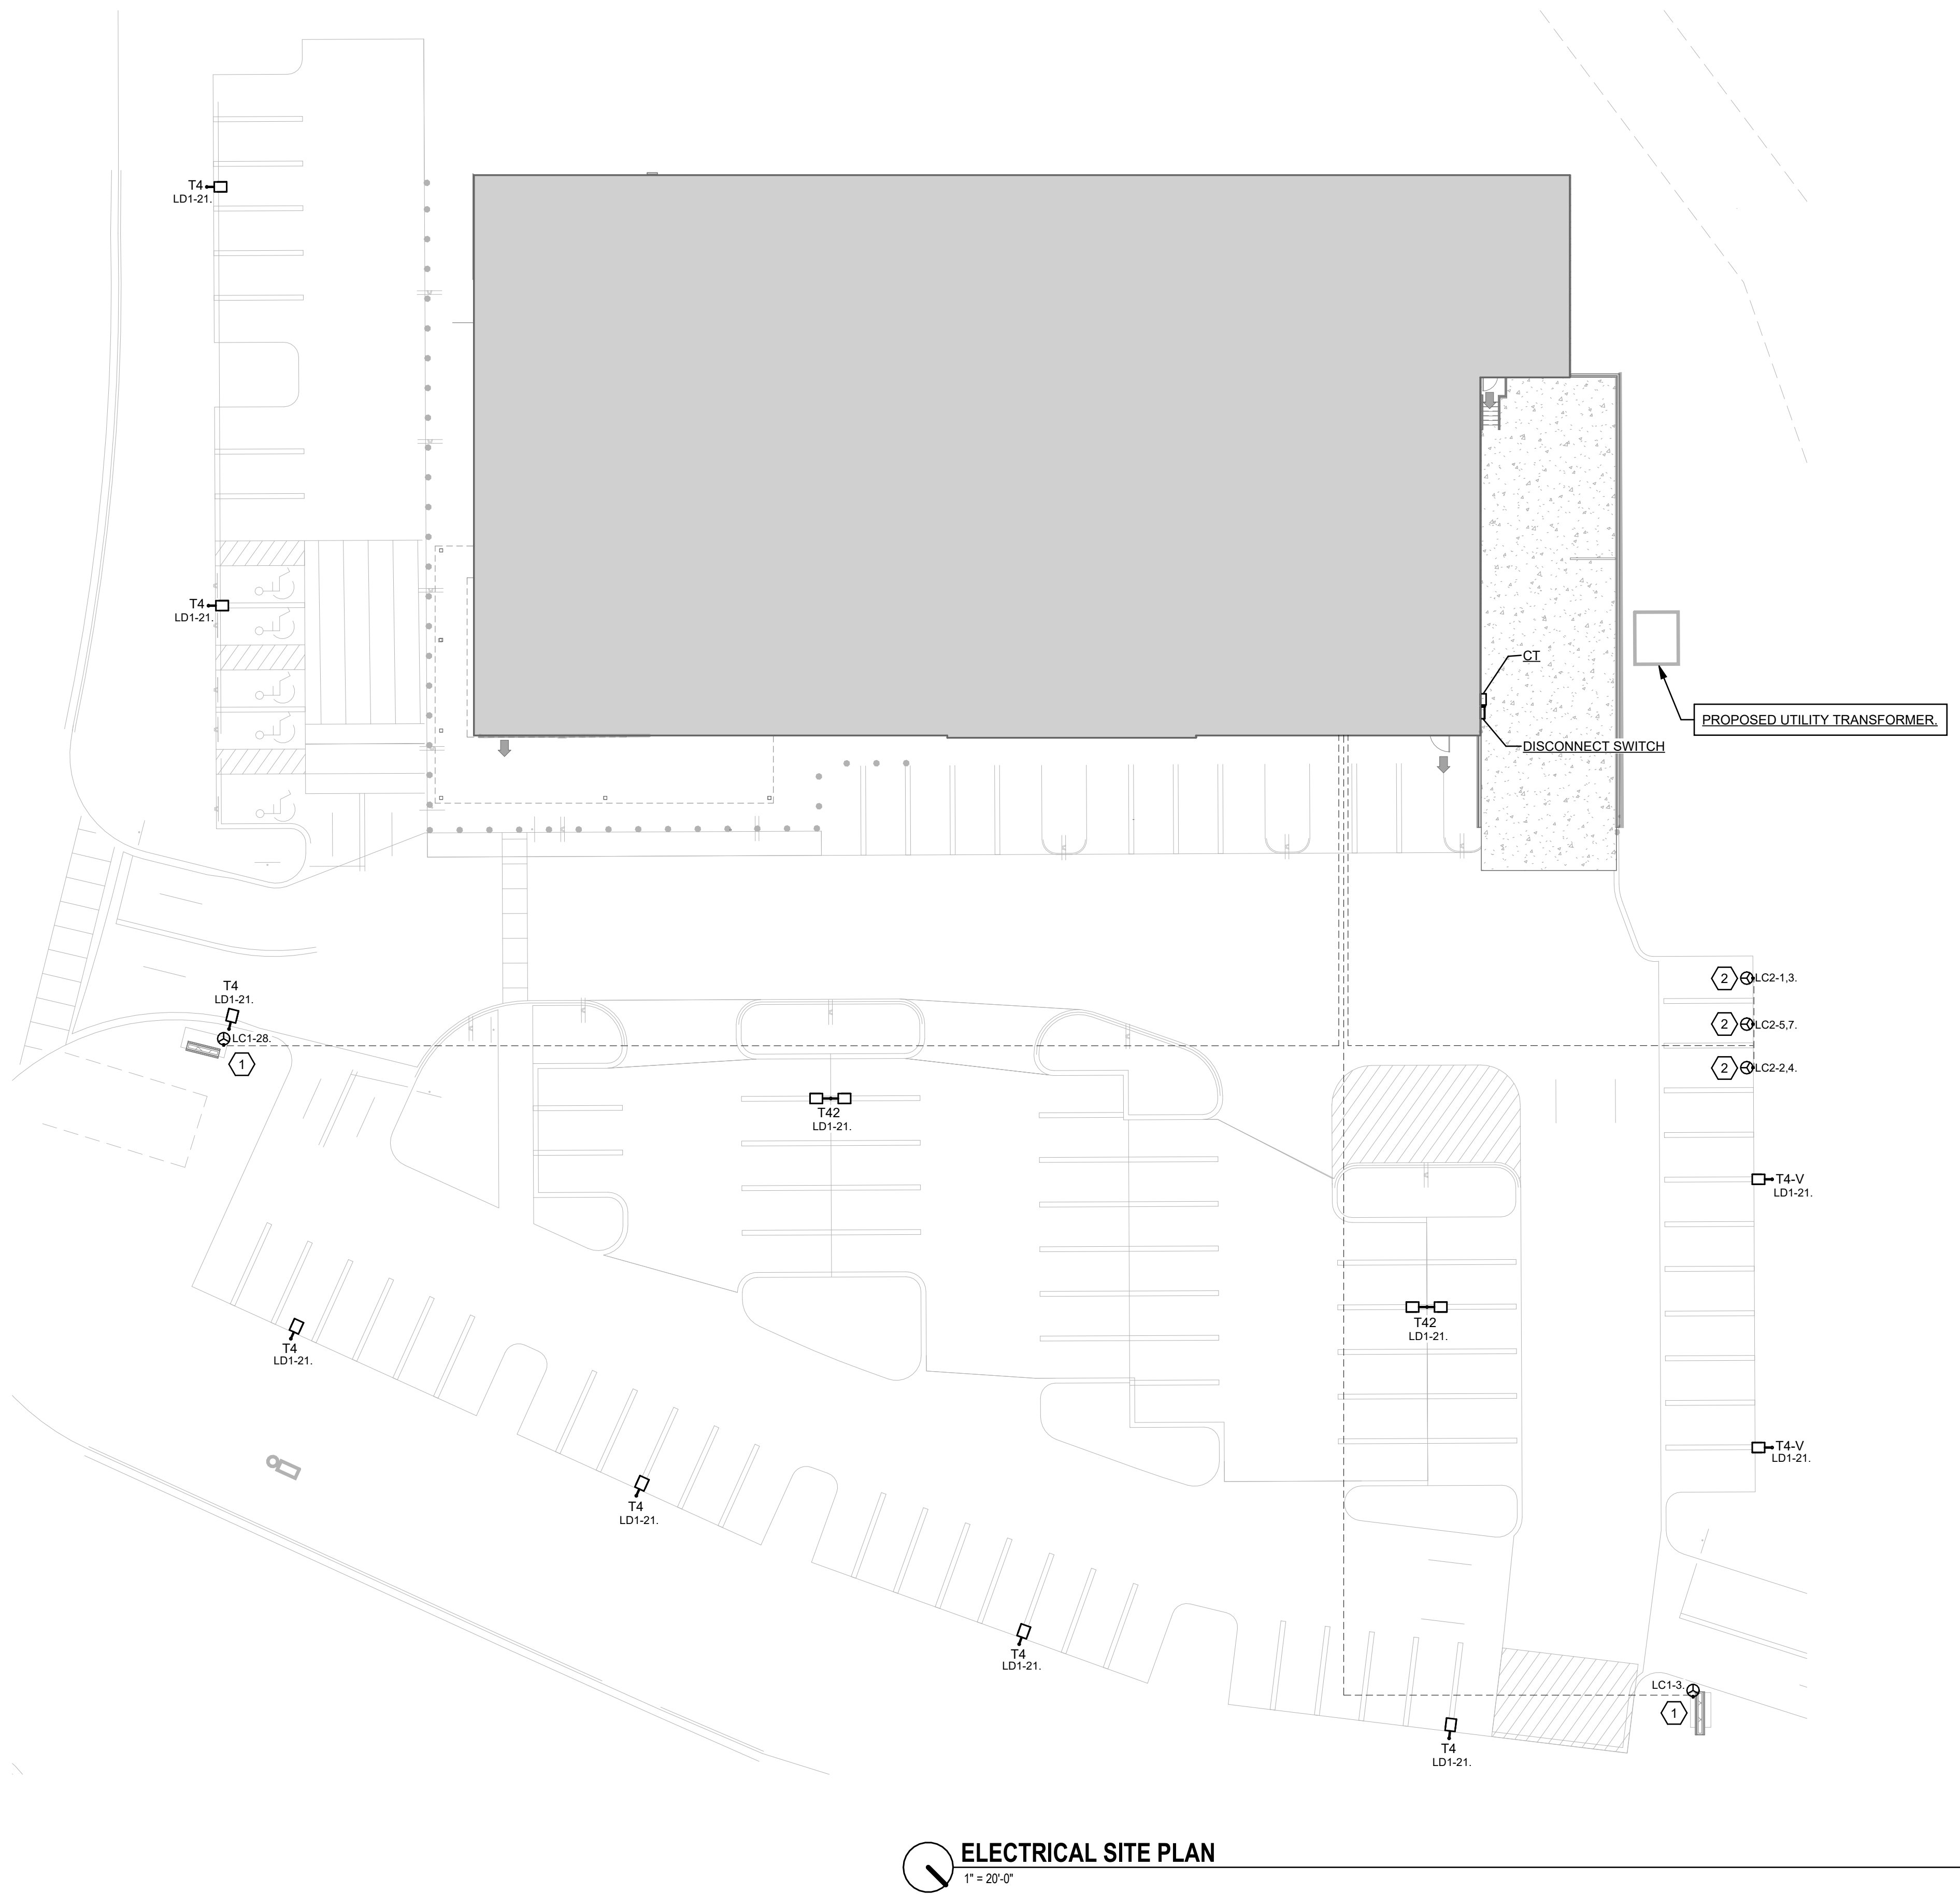

ELECTRICAL SITE PLAN
1" = 20'-0"

ISSUANCE		
1	12/18/2025	PERMIT CYCLE 2
2	01/14/2026	PERMIT CYCLE 3

PROJECT NUMBER
79550191
PROJECT MANAGER
A. HENGSTEBECK
PROFESSIONAL
D. HERSCHER
DRAWN BY
M. GONZALEZ
CHECKED BY
D. HERSCHER


ELECTRICAL SITE
PLAN
E001

LIDL US, LLC
LIDL 1517 NORCROSS, GA

499 JIMMY CARTER BLVD NORCROSS, GA 30993



PROGRESSIVE
ARCHITECTURE ENGINEERING & PLANNING, LLC
**PROGRESSIVE
COMPANIES**
Charlotte, NC | Detroit, MI | Grand Rapids, MI
weareprogressive.com

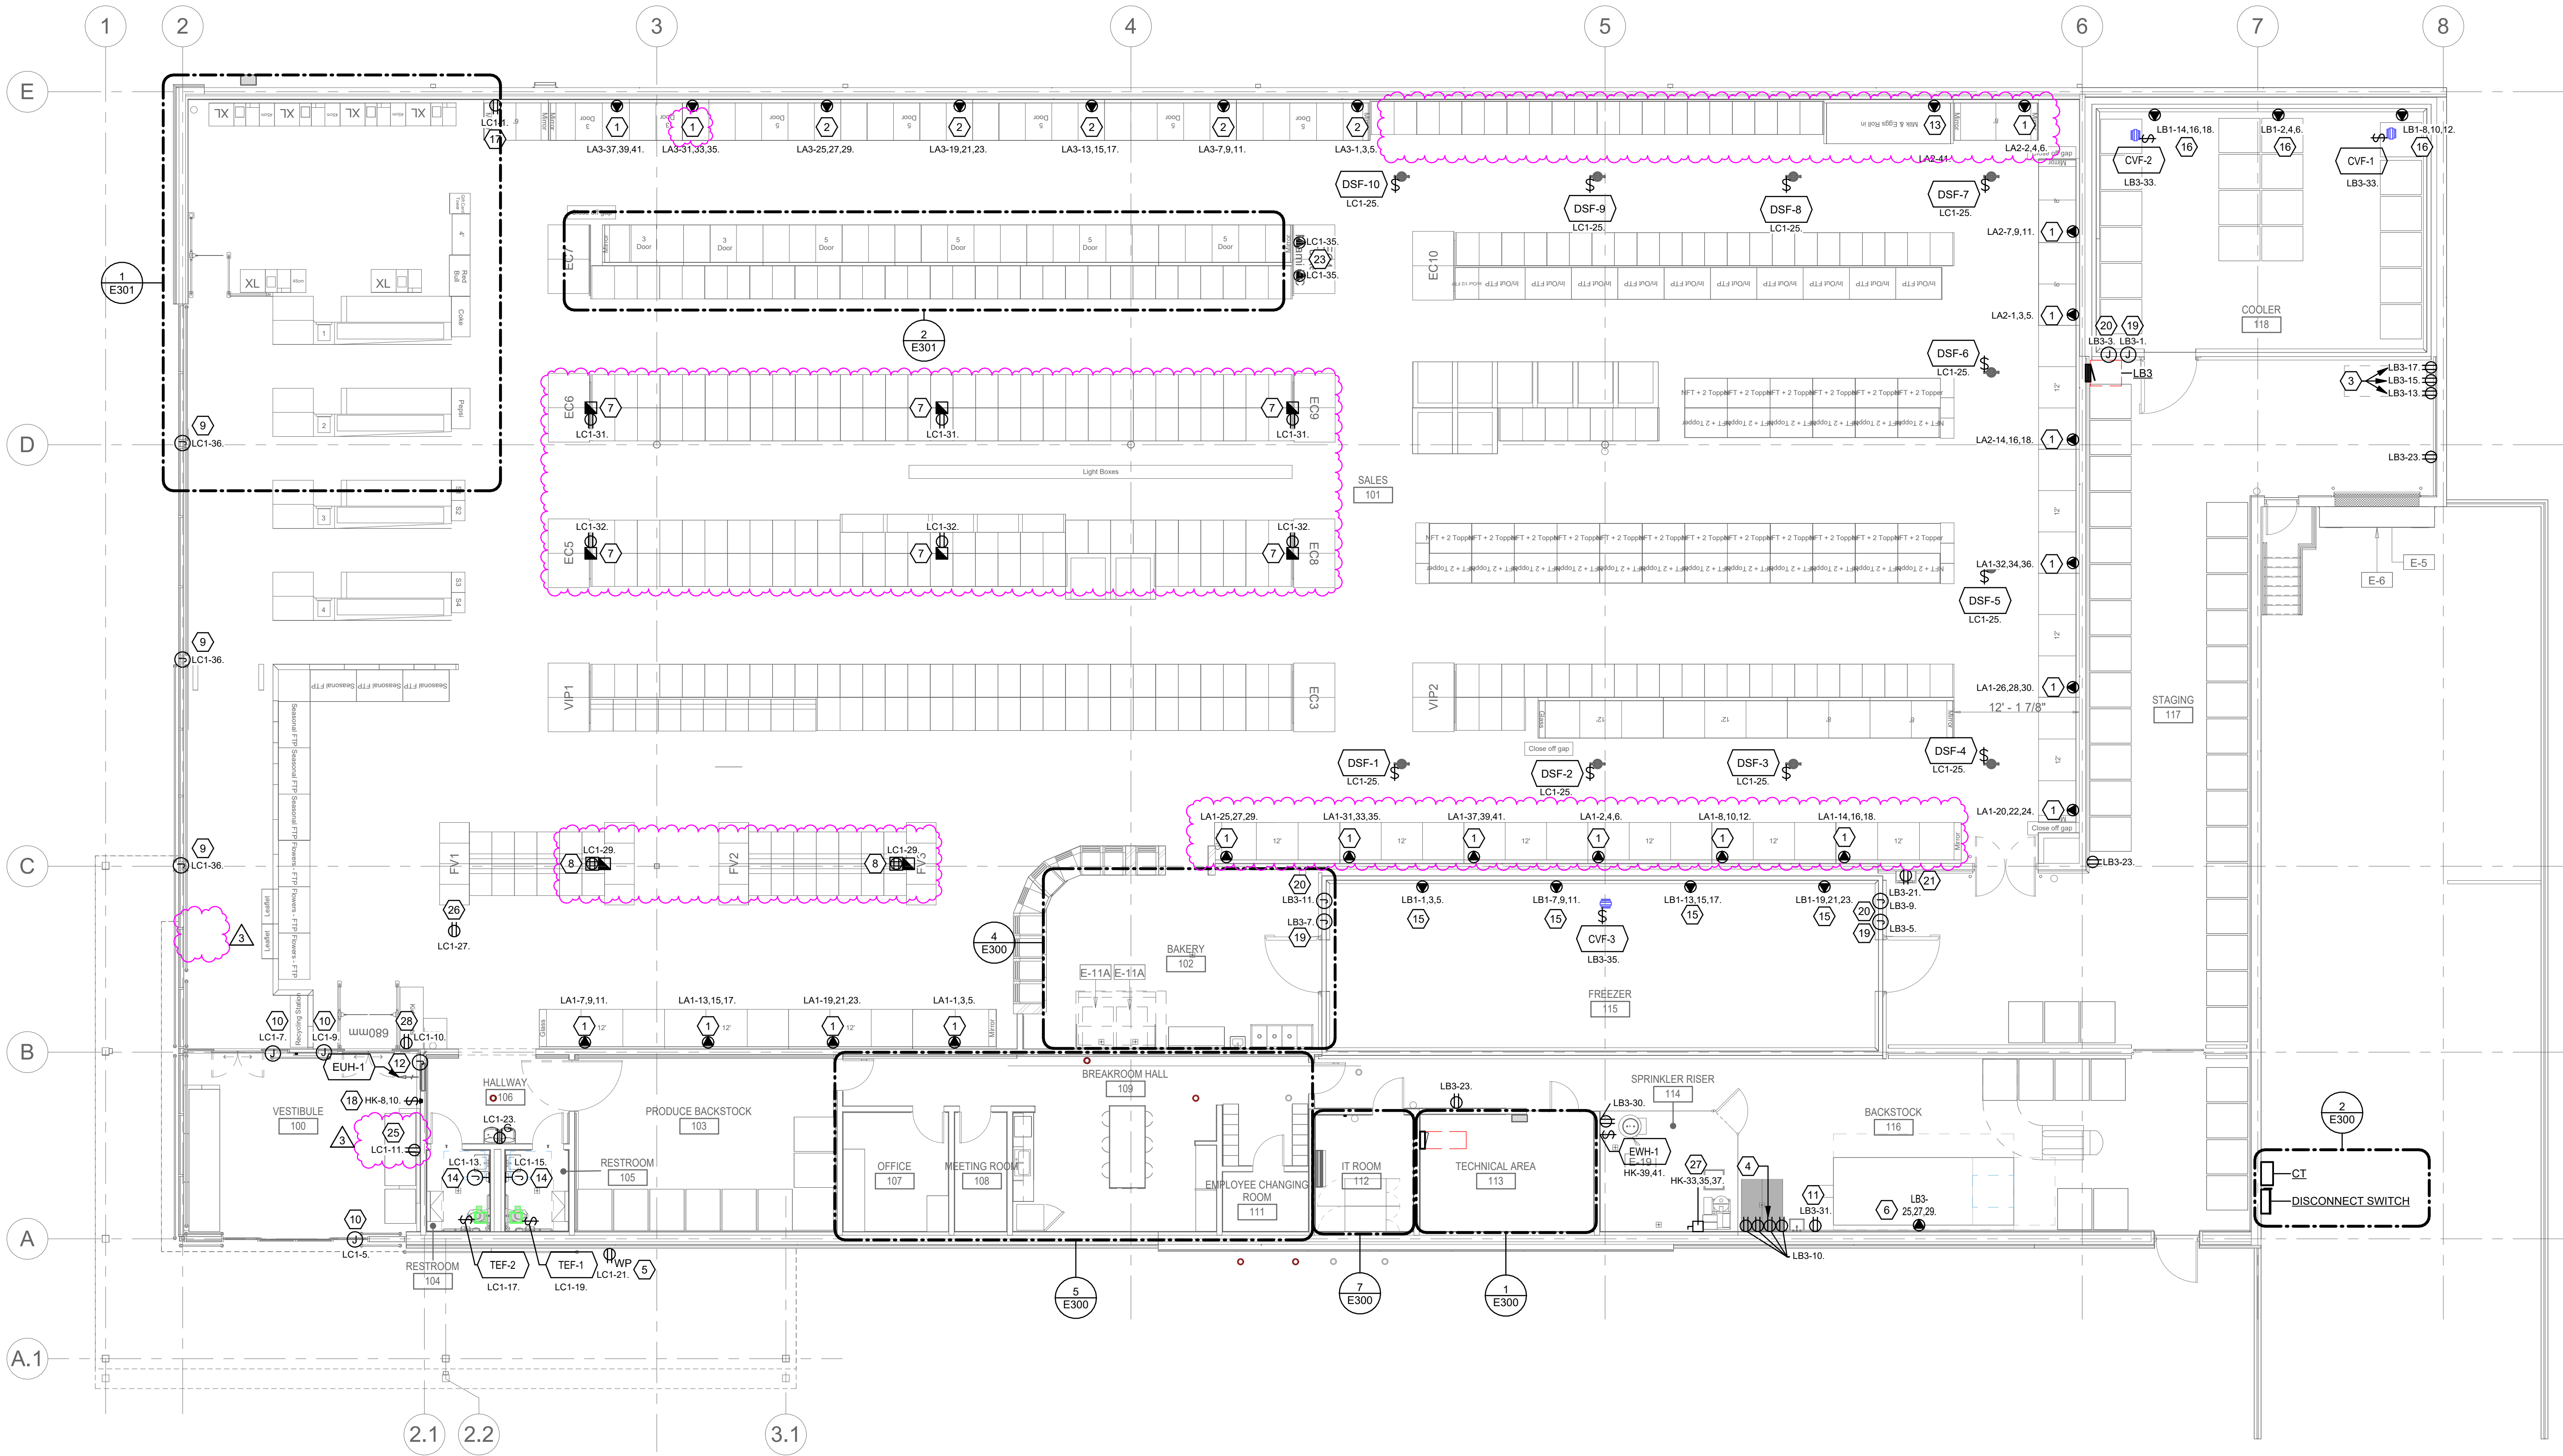

GROUND FLOOR - ELECTRICAL POWER PLAN
1/8" = 1'-0"

GENERAL SHEET NOTES

- REFER TO SHEET E000 FOR LEGENDS, ABBREVIATIONS AND GENERAL NOTES.
- REFER TO SHEET E000 FOR MECHANICAL EQUIPMENT CONNECTION REQUIREMENTS.
- CONTRACTOR SHALL PROVIDE FACTORY BLUE FINISH WIRING DEVICES FOR ALL UPS OUTLETS FED FROM PANEL 1E1T IN STORES FOR IDENTIFICATION PURPOSES. COORDINATE WITH ARCHITECTS FOR EXACT DEVICE FINISH PRIOR TO PURCHASE.

SHEET KEYNOTES

- PROVIDE NEMA L21-20R RECEPTACLES FOR RL-3W FREEZER UNITS, ID6SU-8 MEDIUM TEMP CASES & ID6SU-12 REFRIGERATION UNITS. ELECTRICAL CONTRACTOR TO COORDINATE HEIGHT AND FINAL LOCATION WITH REFRIGERATION MANUFACTURER DRAWINGS.
- PROVIDE NEMA L21-30R RECEPTACLES FOR RL-5W UNITS. ELECTRICAL CONTRACTOR TO COORDINATE HEIGHT AND FINAL LOCATION WITH REFRIGERATION MANUFACTURER DRAWINGS.
- PROVIDE NEMA 5-15R 120V RECEPTACLES FOR PALLET JACKS. ALL RECEPTACLE BACKBOXES SHALL BE RECESSED MOUNTED WITHIN WALL. CONDUIT SHALL BE CONCEALED WITHIN WALL.
- BUG ZAPPER RECEPTACLE.
- RECEPTACLE TO BE RECESSED IN BRICK.
- PROVIDE HUBBELL CS8369 RECEPTACLE FOR BALER.
- DUPLX RECEPTACLE FOR UNDER SHELF LIGHTING. MOUNT RECEPTACLE IN POWER POLE AFTER LIDL FM TEAM HAS COMPLETED INSTALLATION OF SHELVING AND MOUNT 0'-2" ABOVE TOP SHELF. SEE ARCHITECTURAL ELEVATIONS FOR EXACT LOCATION AND MOUNTING HEIGHTS. PROVIDE WIREMOLD WHITE POWERPOLE 250TC WITH EXTENSIONS AS REQUIRED.
- POWER FOR LED UNDERSHELF LIGHTING. 120V, 1-PHASE. PROVIDE RECEPTACLE IN JUNCTION BOX SURFACE MOUNTED TO THE FLOOR. ROUTE CIRCUIT THROUGH LIGHTING CONTRACTOR. REFER TO SHEET E-203 FOR LIGHTING CONTRACTOR DETAILS. SEE ARCHITECTURAL ELEVATIONS FOR EXACT LOCATION AND MOUNTING HEIGHTS. PROVIDE WIREMOLD WHITE POWERPOLE 250TC WITH EXTENSIONS AS REQUIRED.
- JUNCTION BOX FOR POWER TO ELECTRIC MOTOR FOR THE SHADES CONCEALED ON TOP OF STRUCTURE. INSTALL 3/4" CONDUIT FOR POWER CONCEALED WITHIN THE MULLIONS AND STRUCTURE. REFER TO SHEET A404 FOR EXACT LOCATION AND ELEVATION.
- POWER FOR MAIN ENTRANCE DOORS. JUNCTION BOX TO BE CONCEALED.
- PROVIDE RECEPTACLE FOR X-WEB.
- LOCATION OF FAAP. REFER TO ARCHITECTURAL ELEVATIONS FOR EXACT ELEVATION AND LOCATION.
- PROVIDE HUBBLE CS8361C OR EQUIVALENT 50A 125V UL/CSA RECEPTACLE FOR DDX5FWR REFRIGERATION UNIT. ELECTRICAL CONTRACTOR TO COORDINATE HEIGHT AND FINAL LOCATION WITH REFRIGERATION MANUFACTURER DRAWINGS.
- POWER FOR HAND DRYER. MOUNT AT 3'-0" AFF.
- CONTRACTOR TO PROVIDE AND INSTALL L15-30R RECEPTACLE IN BACK BOX AND MATCHING L15-30P CORD CAP. AFFIX BACK BOX TO METAL STUDS. REFER TO ARCHITECTURAL ELEVATIONS FOR FINAL LOCATION AND ELEVATIONS PRIOR TO ROUGH IN. CONTRACTOR TO CONFIRM CLOCKWISE PHASE ROTATION PRIOR TO WIRING/INSTALLATION AND MAKE FINAL CONNECTION BETWEEN RECEPTACLES AND AGGREGATE UNITS.
- CONTRACTOR TO PROVIDE AND INSTALL L15-20R RECEPTACLE IN BACK BOX AND MATCHING L15-20P CORD CAP. AFFIX BACK BOX TO METAL STUDS. REFER TO ARCHITECTURAL ELEVATIONS FOR FINAL LOCATION AND ELEVATIONS PRIOR TO ROUGH IN. CONTRACTOR TO CONFIRM CLOCKWISE PHASE ROTATION PRIOR TO WIRING/INSTALLATION AND MAKE FINAL CONNECTION BETWEEN RECEPTACLES AND AGGREGATE UNITS.
- POWER FOR STORE EQUIPMENT LED LIGHTS.
- POWER FOR ELECTRIC UNIT HEATER.
- PROVIDE A 120V/1P/20AMPS CIRCUIT FOR COOLER/FREEZER DOOR HEATER AND VENT HEATER. ELECTRICAL CONTRACTOR TO COORDINATE WITH MANUFACTURER FOR EXACT LOCATION AND MOUNTING HEIGHT OF JUNCTION BOXES FOR DOOR HEATER AND VENT HEATER.
- PROVIDE A 120V/1P/20AMPS CIRCUIT FOR COOLER/FREEZER DOOR ALARM. ELECTRICAL CONTRACTOR TO COORDINATE WITH MANUFACTURER FOR EXACT LOCATION AND MOUNTING HEIGHT OF JUNCTION BOX FOR ALARM.
- PROVIDE RECEPTACLE FOR SCALE.
- NOT USED.
- PROVIDE (2) 75' CORD REELS MOUNTED AT 13'-0" AFF. TERMINATE ONE CORD REEL WITH A NEMA 5-15R RECEPTACLE. TERMINATE ONE CORD REEL WITH A NEMA L5-15 TWIST LOCK RECEPTACLE. CORD ENDS SHOULD HANG AT 8'-0" AFF.
- NOT USED.
- PROVIDE DEDICATED DUPLX OUTLET AT 1'-4" FOR MOBILITY SCOOTER.
- JOIST MOUNTED RECEPTACLE FOR PVM.
- PROVIDE POWER TO EVAC SYSTEM. CIRCUIT WITH 4 #12, 1 #12 G, 3/4" C. DISCONNECTING MEANS FURNISHED WITH EQUIPMENT.
- PROVIDE DUPLX RECEPTACLE FOR ELECTRIC SECURITY GATES. WALL MOUNT AT 9'-0" AFF.

ISSUANCE

1	12/18/2025	PERMIT CYCLE 2
2	01/14/2026	PERMIT CYCLE 3
3	05/28/2026	CCD 01

PROJECT NUMBER

79650191

PROJECT MANAGER

A. HENGSTEBECK

PROFESSIONAL


D. HERSCHER

DRAWN BY

M. GONZALEZ

CHECKED BY

D. HERSCHER

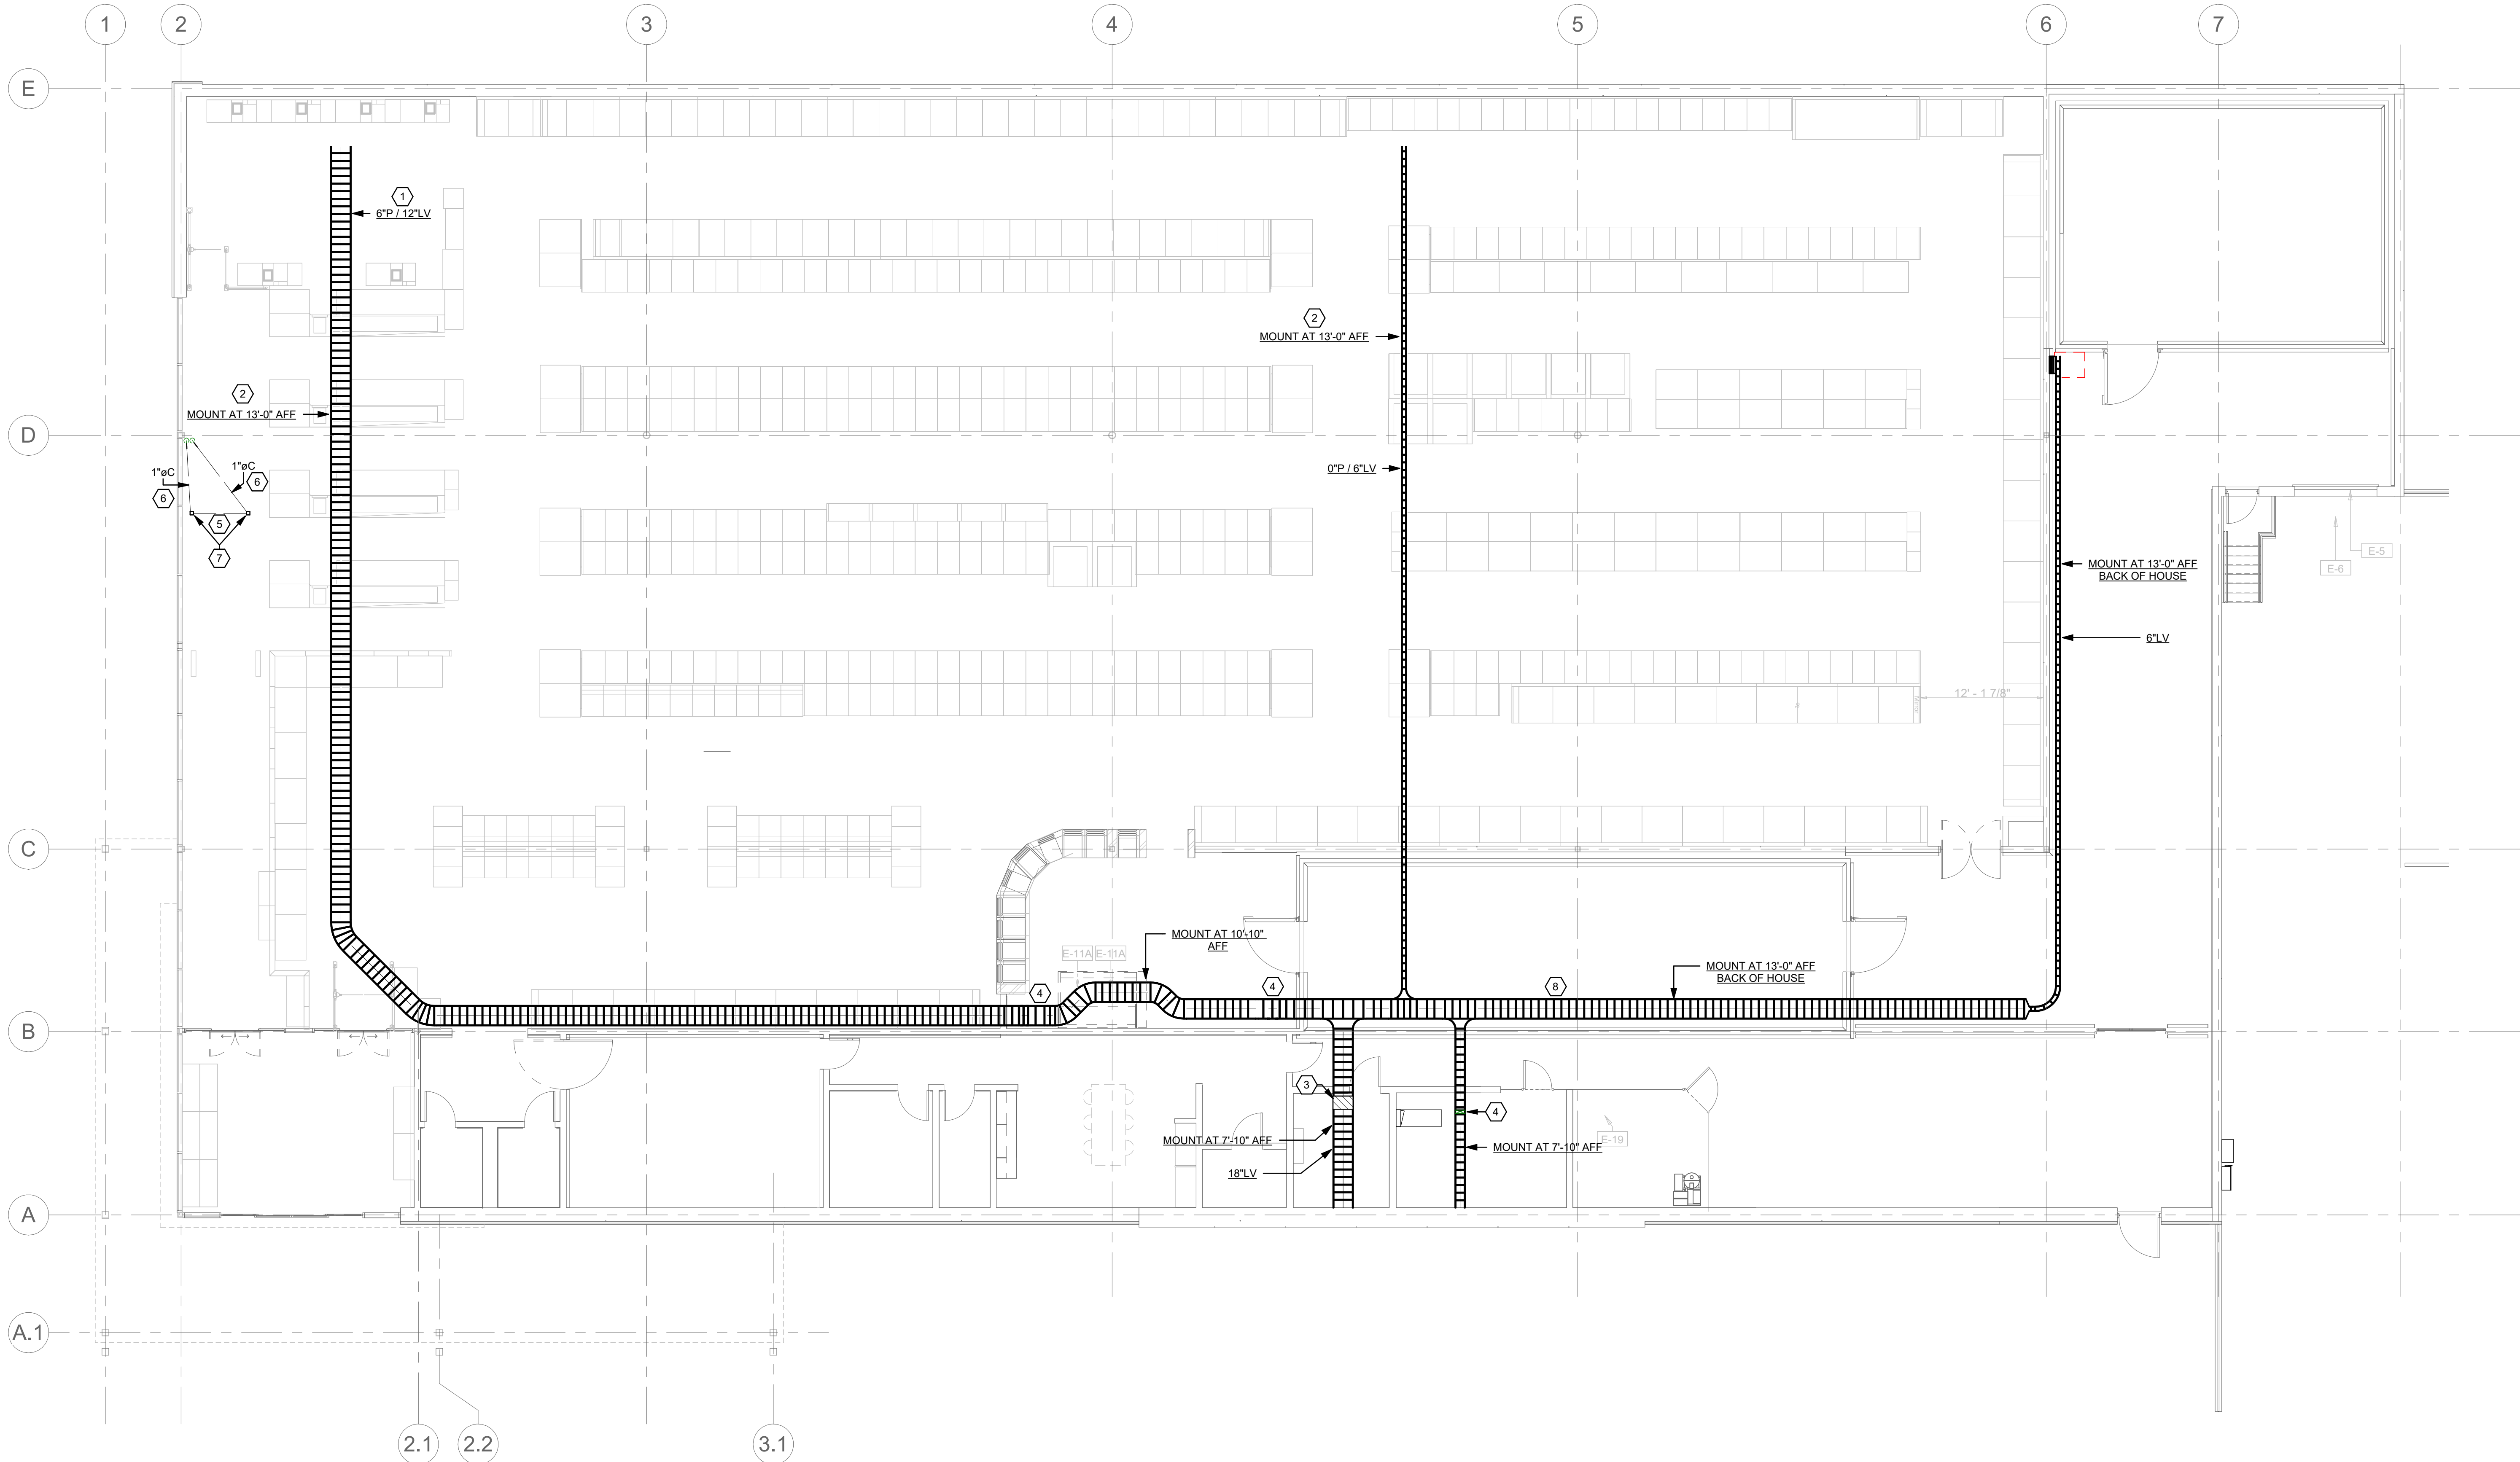

GROUND FLOOR - CABLE WIREWAY PLAN
1/8" = 1'-0"

GENERAL SHEET NOTES

- REFER TO SHEET E000 FOR LEGENDS, ABBREVIATIONS AND GENERAL NOTES.
- ALL CABLE WIREWAY SHALL RUN PARALLEL OR PERPENDICULAR TO BUILDING STRUCTURE. CABLES INSIDE CABLE WIREWAY SHALL BE INSTALLED IN A NEAT WORKMANLIKE MANNER. IF DEEMED NECESSARY BY OWNER, EXCESSIVE SAGGING AND OVER CROSSING OF CABLES SHALL BE RE-INSTALLED BY THE CONTRACTOR AT NO ADDITIONAL COST TO OWNER.
- ALL CABLE WIREWAYS AND CABLE WIREWAY CONNECTIONS AT SALES FLOOR SHALL BE WHITE.
- ELECTRICAL CONTRACTOR TO PROVIDE PROTECTION FOR RACEWAYS/CABLES/BOXES AT THE ROOF DECK AS PER NEC SECTION 300.4(E).
- ALL CABLE TRAY IN SALES AREA TO BE PROVIDED WITH WHITE LINER.

SHEET KEYNOTES

- WHERE LOW VOLTAGE AND LINE VOLTAGE POWER INTERSECT, ELECTRICAL CONTRACTOR TO PROVIDE BARRIER BRIDGE IN A MANNER THAT LOW AND HIGH VOLTAGE ARE KEPT SEPARATED. REFER TO DETAIL 3, SHEET E604.
- ADD CABLE TRAY LINERS FOR CUSTOMER FACING SPACES.
- EZ PATH THROUGH CEILING.
- CABLE WIREWAY VERTICAL TRANSITION. REFER TO DETAIL 4, SHEET E604 FOR CABLE WIREWAY VERTICAL TRANSITION DETAIL.
- CONDUIT WITH PULL STRING RUN BELOW FLOOR BETWEEN ELECTRONIC ALARM SYSTEM (EAS) PEDESTALS TO STUB UP LOCATIONS PRIOR TO SLAB POUR.
- CONDUIT WITH PULL STRING RUN BETWEEN ELECTRONIC ALARM SYSTEM (EAS) PEDESTAL AND POWER SUPPLY FROM STUB UP LOCATION PRIOR TO SLAB POUR.
- GENERAL LOCATION OF STUB UP IN FLOOR. EXACT LOCATION DETERMINED BY GC. HUBBELL "SystemOne" FLUSH FLOOR BOX WITH COVER TO BE INSTALLED IN CONCRETE AS PROVISION FOR FUTURE EAS PEDESTAL LOCATIONS.
- CABLE TRAY TO BE INSTALLED CLEAR OF AGGREGATES REQUIRED FOR COLDROOMS.

ISSUANCE
1 12/18/2025 PERMIT CYCLE 2

PROJECT NUMBER
77855191
PROJECT MANAGER
A. HENGSTEBECK
PROFESSIONAL
D. HERSCHER
DRAWN BY
M. GONZALEZ
CHECKED BY
D. HERSCHER


GROUND FLOOR -
CABLE WIREWAY
PLAN
E102

LIDL US, LLC
LIDL 1517 NORCROSS, GA

499 JIMMY CARTER BLVD NORCROSS, GA 30093



PROGRESSIVE ARCHITECTURE ENGINEERING & PLANNING, LLC
**PROGRESSIVE
COMPANIES**
Charlotte, NC | Detroit, MI | Grand Rapids, MI
weareprogressive.com

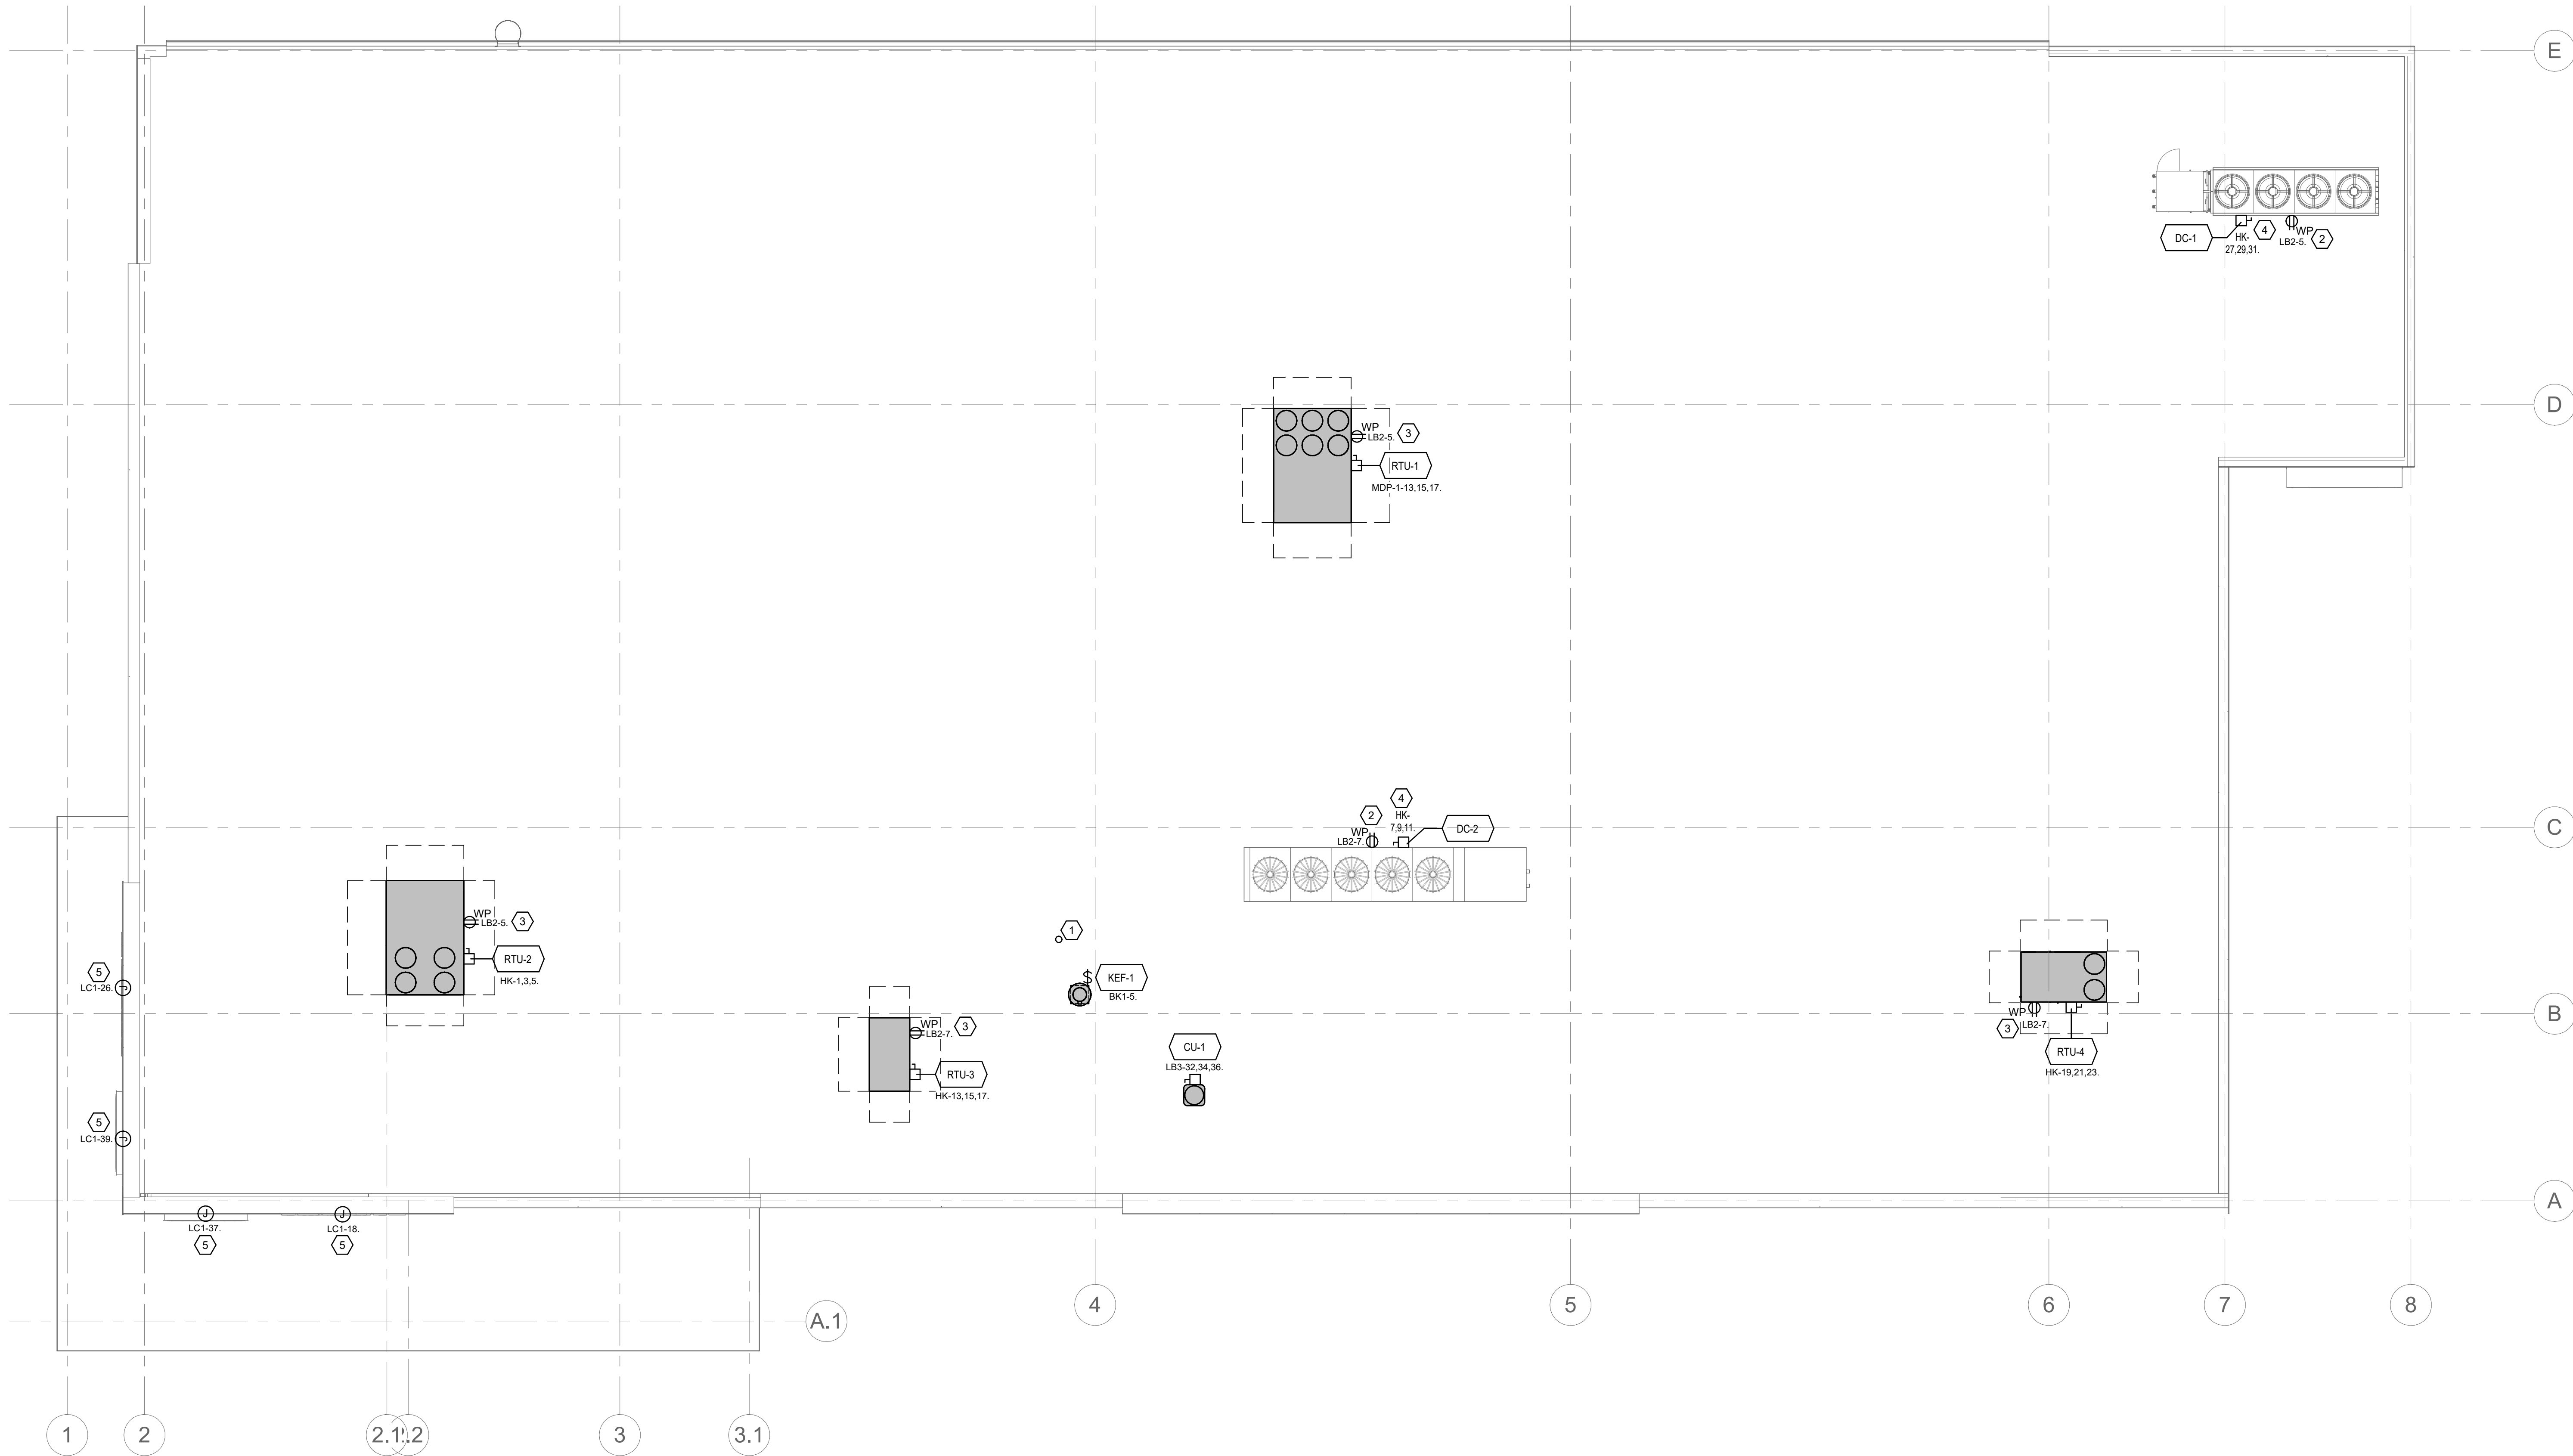

ROOF - POWER PLAN
1/8" = 1'-0"

GENERAL SHEET NOTES

- REFER TO SHEET E000 FOR LEGENDS, ABBREVIATIONS AND GENERAL NOTES.
- ELECTRICAL CONTRACTOR TO INSTALL NEMA 3R NON FUSED DISCONNECT SWITCH FOR ALL EQUIPMENT LOCATED IN ROOF. DISCONNECT PROVIDED BY MECHANICAL CONTRACTOR. LOCATE THEM WITHIN SIGHT OF EQUIPMENT NOT TO EXCEED 5FT AND INDEPENDENTLY MOUNTED ON UNISTRUT.
- LOCATION OF LOCAL DISCONNECT SWITCH SHALL BE COORDINATED WITH THE EQUIPMENT MANUFACTURER RECOMMENDATIONS/REQUIREMENTS PRIOR TO ROUGH-IN.
- REFER TO SHEET E500 FOR MECHANICAL EQUIPMENT CONNECTION REQUIREMENTS.

SHEET KEYNOTES

- PROVIDE 1" RIDGID CONDUIT THROUGH ROOF PENETRATION FOR GPS ANTENNA. REFER TO ARCHITECTURAL DRAWINGS. COORDINATE EXACT LOCATION WITH OWNER PRIOR TO PENETRATION AND CONDUIT INSTALLATION.
- MOUNT SERVICE RECEPTACLE ON STEEL DUNNAGE OF DRYCOOLER.
- ELECTRICAL CONTRACTOR TO WIRE GFCI RECEPTACLE INTEGRAL TO EACH UNIT ROOF TOP UNIT. RECEPTACLES IS INTERNALLY MOUNTED AND PROVIDED BY MANUFACTURER.
- DRY COOLER DISCONNECT INTERNALLY MOUNTED AND PROVIDED BY MANUFACTURER.
- FOR POWERED GROCERY SIGNAGE, PROVIDE A DEDICATED 20A 120V 1-PHASE CIRCUIT WITH 2#12 AND 1#12 GRD IN A 3/4" CONDUIT VIA THE LIGHTING CONTACTOR. CONTRACTOR SHALL PROVIDE A NEMA 3R RATED ENCLOSURE METAL TRANSFORMER BOX WITH LOCAL DISCONNECT AN INTEGRAL TOGGLE SWITCH AND AC-DC POWER PACK. ALL PRIMARY SIDE CABLING TO THE TRANSFORMER BOX SHALL BE IN CONDUIT. PROVIDE WHIP CONDUITS AS REQUIRED FOR TERMINATION AT THE METAL TRANSFORMER BOX. CONTRACTOR SHALL COORDINATE WITH MANUFACTURER FOR TRANSFORMER SECONDARY SIDE CABLING AND LED MODULE TERMINATIONS.

COMcheck Software Version COMcheckWeb

Interior Lighting Compliance Certificate

Project Information

Energy Code:
Project Title:
Project Type:

2015 IECC
Lidl Norcross GA
New Construction

Construction Site:
4990 JIMMY CARTER BLVD.
NORCROSS, Georgia 30093

Owner/Agent:
Lidl US Operations LLC
3500 S. Clark St.
Arlington, Virginia 22202

Designer/Contractor:
Progressive Architecture
Engineering & Planning I, LLC
1801 N. Graham Street
Charlotte, North Carolina 28206
704-731-8080

Additional Efficiency Package(s)

Credits: 1.0 Required 1.0 Proposed
Reduced Lighting Power, 1.0 credit

Allowed Interior Lighting Power

A Area Category	B Floor Area (ft ²)	C Allowed Watts / ft ²	D Allowed Watts
1-Retail	23352	1.13	26481
Total Allowed Watts =			26481

Proposed Interior Lighting Power

A Fixture ID : Description / Lamp / Wattage Per Lamp / Ballast	B Lamps/ Fixture	C # of Fixture	D Wattage (C X D)	E (C X D)
1-Retail				
LED-FP-2x2 LED: Other:	1	30	40	1200
LED-Df2-8: LINEAR LED: Other:	1	84	65	5460
LED-Df2-6: LINEAR LED: Other:	1	86	48	4128
LED-Df2-4: LINEAR LED: Other:	1	8	32	256
LED-Sk2: LED SPOT LIGHT: Other:	1	65	45	2925
LED-VI: LINEAR LED: Other:	1	9	38	342
LED-BB-6: LINEAR LED: Other:	1	10	48	480
LED-BB-4: LINEAR LED: Other:	1	3	32	96
LED-BB-2: LINEAR LED: Other:	1	1	16	16
LED-BB-MS: LINEAR LED: Other:	1	6	48	288
Total Proposed Watts =			15191	

Interior Lighting PASSES: Design 43% better than code

Statement

Compliance Statement: The proposed interior lighting design represented in this document is consistent with the building plans, specifications, and other calculations submitted with this permit application. The proposed interior lighting systems have been designed to meet the 2015 IECC requirements in COMcheck Version COMcheckWeb and to comply with any applicable mandatory requirements listed in the Inspection Checklist.

Project Title: Lidl Norcross GA

Report date: 05/27/26

Data filename: Page 1 of 8

COMcheck Software Version COMcheckWeb

Exterior Lighting Compliance Certificate

Project Information

Energy Code:
Project Title:
Project Type:
Exterior Lighting Zone

2015 IECC
Lidl Norcross GA
New Construction
2 (Residential mixed use area (LZ2))

Construction Site:
4990 JIMMY CARTER BLVD.
NORCROSS, Georgia 30093

Owner/Agent:
Lidl US Operations LLC
3500 S. Clark St.
Arlington, Virginia 22202

Designer/Contractor:
Progressive Architecture
Engineering & Planning I, LLC
1801 N. Graham Street
Charlotte, North Carolina 28206
704-731-8080

Allowed Exterior Lighting Power

A Area/Surface Category	B Quantity	C Allowed Watts /	D Tradable Wattage	E Allowed Watts (B X C)
LOADING DOCK (Drive-up windows/doors)	2 windows	400	No	800
EMPLOYEE ENTRANCE (Other door (not main entry))	4 ft of door	20	Yes	80
LOADING AREA (Driveway)	1284 ft ²	0.06	Yes	77
ILLUMINATED STORE FRONT (illuminated area of facade wall or surface)	661 ft ²	0.1	No	66
CANOPY (Entry canopy)	1247 ft ²	0.25	Yes	312
Total Tradable Watts (a) =			469	
Total Allowed Watts =			1335	
Total Allowed Supplemental Watts (b) =			600	

Proposed Exterior Lighting Power

A Fixture ID : Description / Lamp / Wattage Per Lamp / Ballast	B Lamps/ Fixture	C # of Fixture	D Wattage (C X D)	E (C X D)
LOADING DOCK (Drive-up windows/doors, 2 windows or doors): Non-tradable Wattage				
LED-WP-WALL PACK: Other:	1	2	37	74
EMPLOYEE ENTRANCE (Other door (not main entry), 4 ft. of door width): Tradable Wattage				
LED-WP-WALL PACK: Other:	1	1	37	37
LOADING AREA (Driveway, 1284 ft ²): Tradable Wattage				
LED-WP-WALL PACK: Other:	1	3	37	111
ILLUMINATED STORE FRONT (illuminated area of facade wall or surface, 661 ft ²): Non-tradable Wattage				
LED-WP-WALL PACK: Other:	1	2	37	74
CANOPY (Entry canopy, 1247 ft ²): Tradable Wattage				
LED-DLI-4 DOWNLIGHT: Other:	1	9	15	135
Total Tradable Proposed Watts =			283	

Project Title: Lidl Norcross GA

Report date: 05/27/26

Data filename: Page 3 of 8

COMcheck Software Version COMcheckWeb

Inspection Checklist

Requirements: 58.0% were addressed directly in the COMcheck software

Text in the "Comments/Assumptions" column is provided by the user in the COMcheck Requirements screen. For each requirement, the user certifies that a code requirement will be met and how that is documented, or that an exception is being claimed. Where compliance is itemized in a separate table, a reference to that table is provided.

Section # & Req.ID	Plan Review	Complies?	Comments/Assumptions
C103.2 [PR4] ¹	Plans, specifications, and/or calculations provide all information with which compliance can be determined for the interior lighting and electrical systems and equipment and document where exceptions to the standard are claimed. Information provided should include interior lighting power calculations, wattage of bulbs and ballasts, transformers and control devices.	☐ Complies ☐ Does Not ☐ Not Observable ☐ Not Applicable	
C103.2 [PR8] ¹	Plans, specifications, and/or calculations provide all information with which compliance can be determined for the exterior lighting and electrical systems and equipment and document where exceptions to the standard are claimed. Information provided should include exterior lighting power calculations, wattage of bulbs and ballasts, transformers and control devices.	☐ Complies ☐ Does Not ☐ Not Observable ☐ Not Applicable	
C406 [PR9] ¹	Plans, specifications, and/or calculations provide all information with which compliance can be determined for the additional energy efficiency package options.	☐ Complies ☐ Does Not ☐ Not Observable ☐ Not Applicable	

Additional Comments/Assumptions:

1 High Impact (Tier 1) 2 Medium Impact (Tier 2) 3 Low Impact (Tier 3)

Project Title: Lidl Norcross GA

Report date: 05/27/26

Data filename: Page 5 of 8

COMcheck Software Version COMcheckWeb

Inspection Checklist

Section # & Req.ID

Footing / Foundation Inspection

Complies?

Comments/Assumptions

C402.2.6 [FO12]¹

Radiant heating systems panels insulated to >=R-3.5 on face opposite space being heated

☐ Complies
☐ Does Not
☐ Not Observable
☐ Not Applicable

See the Envelope Assemblies table for values.

Additional Comments/Assumptions:

1 High Impact (Tier 1) 2 Medium Impact (Tier 2) 3 Low Impact (Tier 3)

Project Title: Lidl Norcross GA

Report date: 05/27/26

Data filename: Page 6 of 8

COMcheck Software Version COMcheckWeb

Inspection Checklist

Section # & Req.ID

Rough-In Electrical Inspection

Complies?

Comments/Assumptions

C405.2.1 [EL15]¹

Lighting controls installed to uniformly reduce the lighting load by at least 50%

☐ Complies
☐ Does Not
☐ Not Observable
☐ Not Applicable

C405.2.1 [EL18]¹

Occupancy sensors installed in required spaces.

☐ Complies
☐ Does Not
☐ Not Observable
☐ Not Applicable

C405.2.1, C405.2.2, 3 [EL23]¹

Independent lighting controls installed per approved lighting plans and all manual controls readily accessible and visible to occupants.

☐ Complies
☐ Does Not
☐ Not Observable
☐ Not Applicable

C405.2.2, 1 [EL22]¹

Automatic controls to shut off all building lighting installed in all buildings.

☐ Complies
☐ Does Not
☐ Not Observable
☐ Not Applicable

C405.2.3 [EL16]¹


Daylight zones provided with individual controls that control the lights independent of general area lighting.

☐ Complies
☐ Does Not
☐ Not Observable
☐ Not Applicable

C405.2.3, C405.2.3, 1 [EL20]¹

Primary sidedighted areas are equipped with required lighting controls.

☐ Complies
<

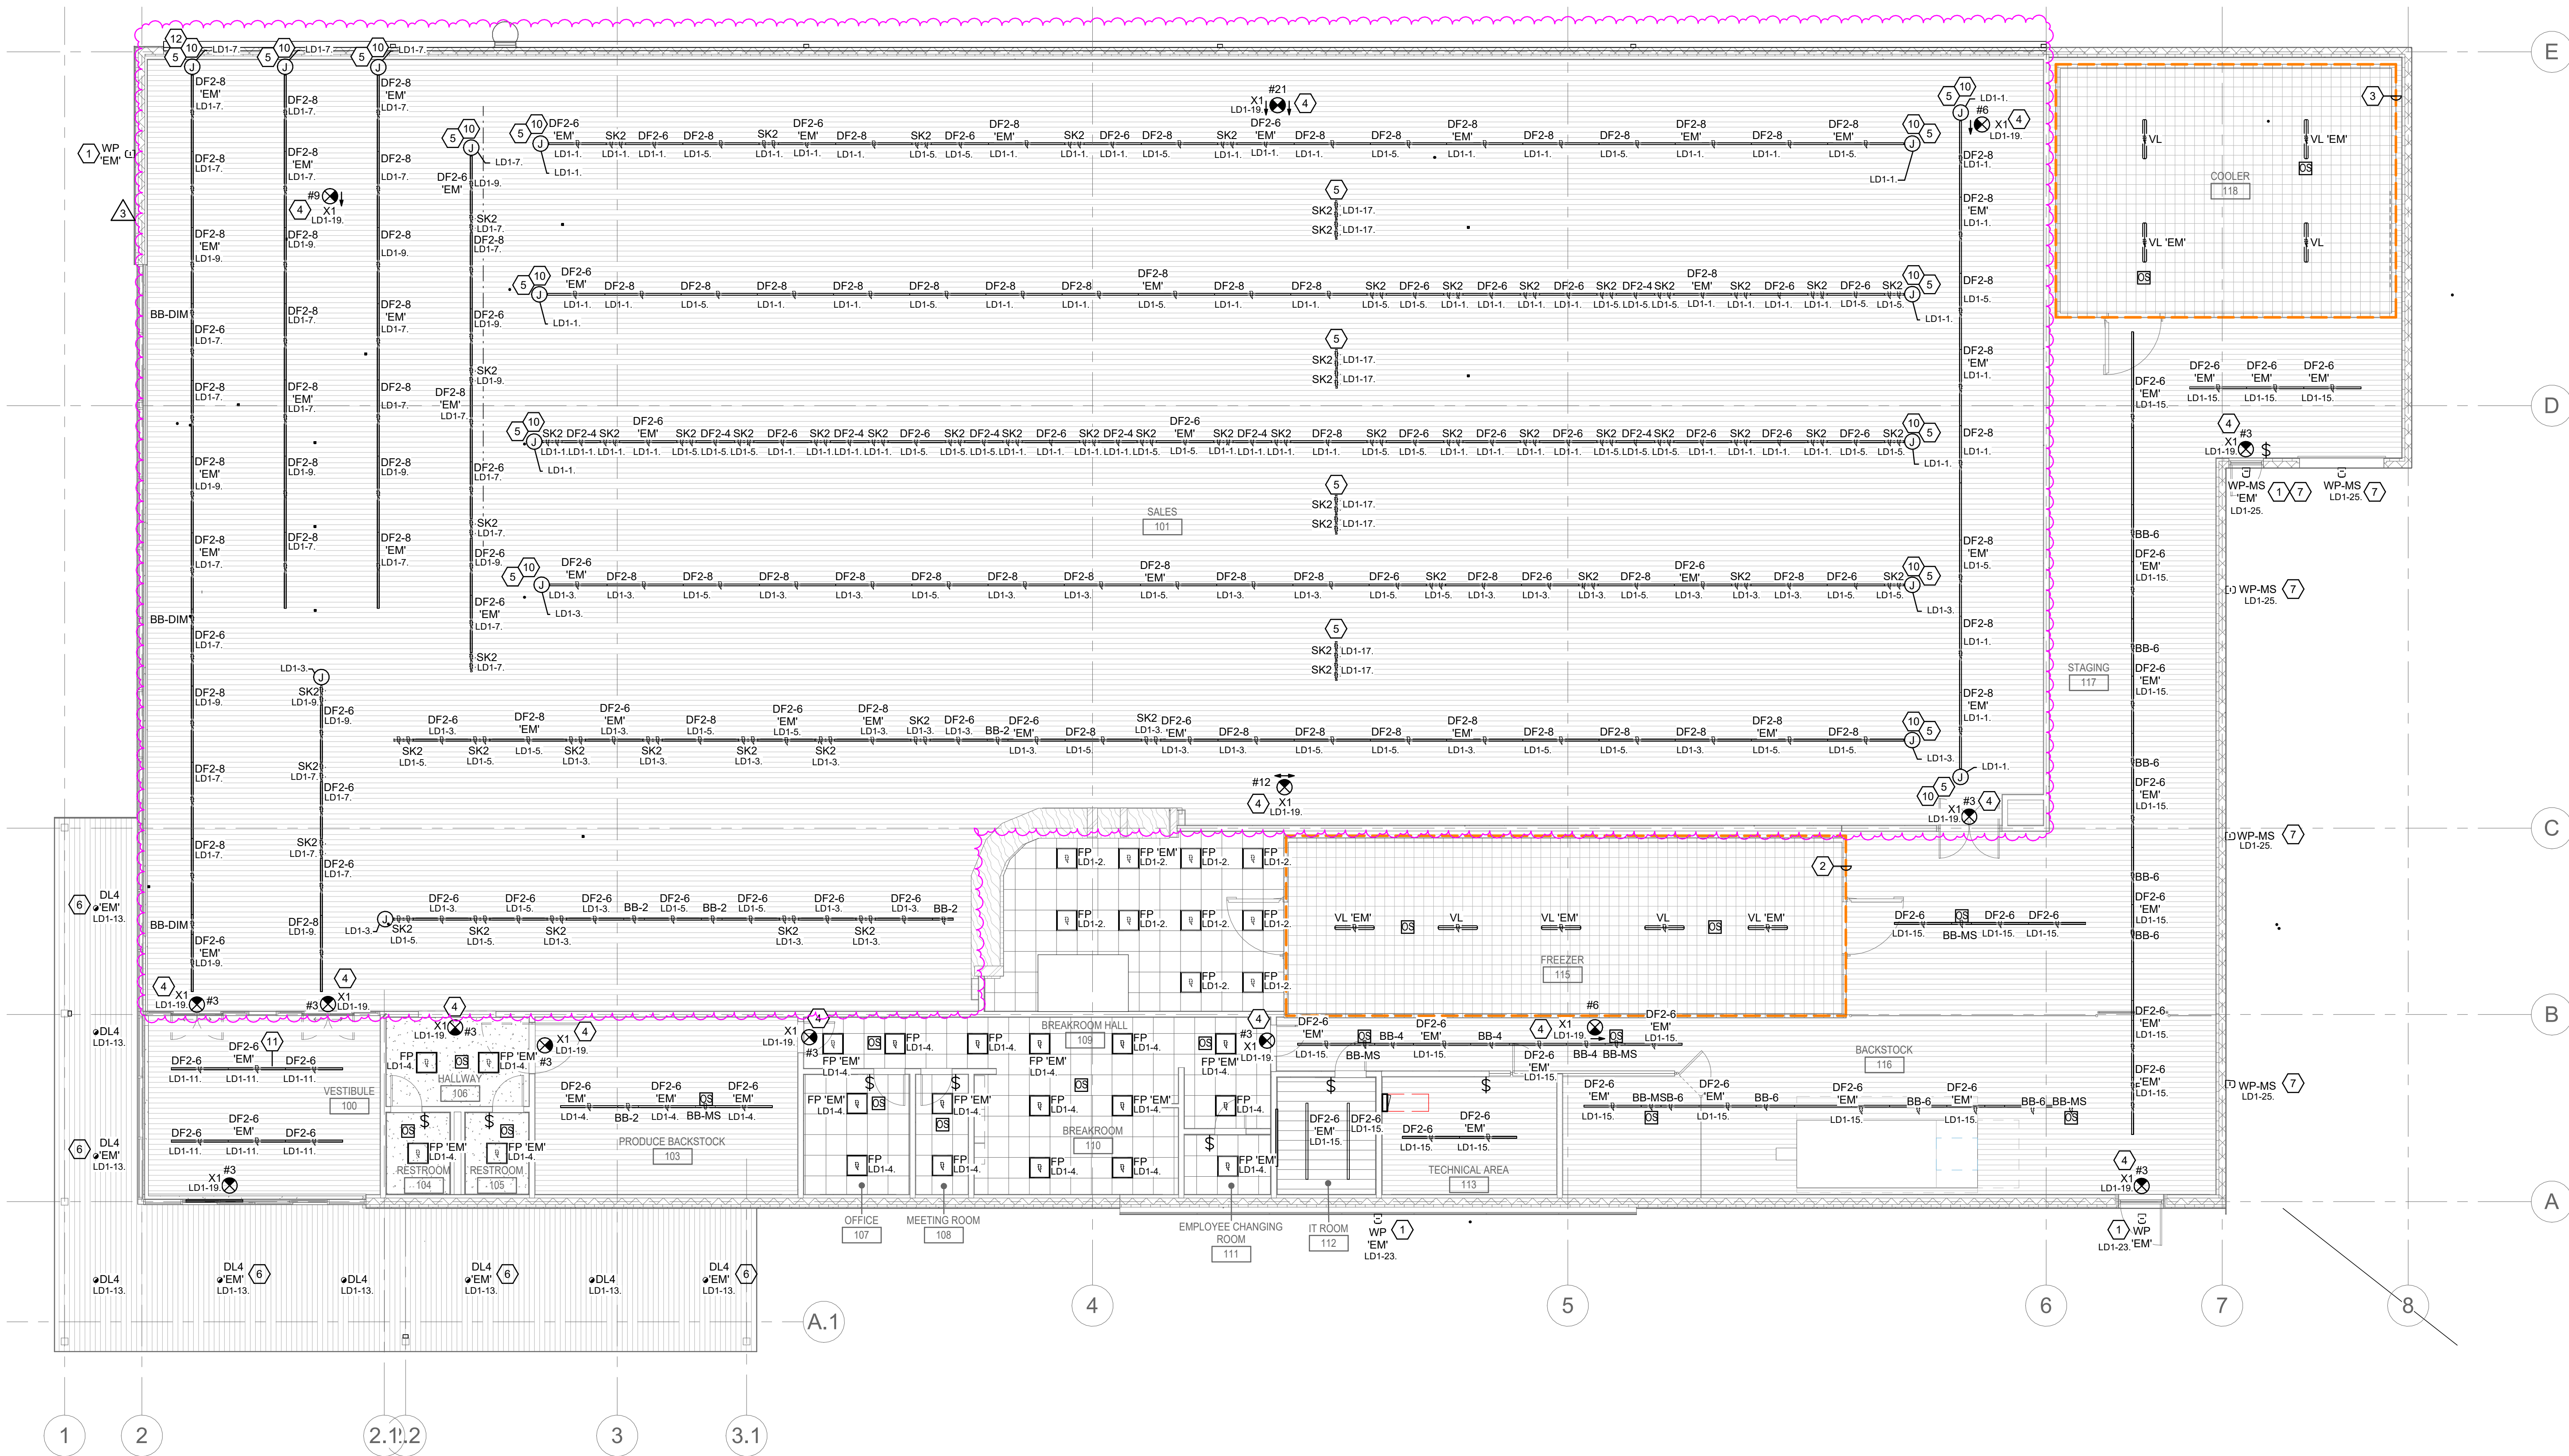

GROUND FLOOR - LIGHTING PLAN
1/8" = 1'-0"

GENERAL SHEET NOTES

- REFER TO SHEET E000 FOR LEGENDS, ABBREVIATIONS AND GENERAL NOTES.
- SPOTLIGHTS TO BE ADJUSTED BY ELECTRICAL CONTRACTOR AFTER LIDL FITS OUT STORE.
- REFER TO SHEET E202 FOR LIGHTING FIXTURE SCHEDULE AND CONTROL SEQUENCE.
- ALL LIGHT FIXTURES IN THE SALES FLOOR AREA SHALL BE MOUNTED AT 11'-6" AFF. LIGHT FIXTURE HANGER LENGTH SHALL BE 9'-0" UNLESS OTHERWISE NOTED. REFER TO ARCH DRAWINGS FOR ADDITIONAL INFORMATION.
- ALL LIGHTING IN THE SALES AREA IS CONTROLLED BY BMS AND ROUTED THROUGH LIGHTING CONTACTOR.
- ELECTRICAL CONTRACTOR TO PROVIDE ALL NECESSARY POWER FEEDS AND AIRCRAFT CABLE FOR FIXTURE RUNS.
- ALL VESTIBULE LIGHT FIXTURES SHALL BE MOUNTED AT 11'-6" AFF.
- ALL LIGHT FIXTURES WITHIN 15'-0" OF WINDOWS SHALL INTERFACE WITH DAYLIGHT SENSOR.
- SEE SHEET E202 FOR LIGHTING CONTROL SEQUENCE OF OPERATIONS AND LUMINAIRE SCHEDULE.
- ALL SPOTLIGHTS TO BE ADJUSTED BY ELECTRICAL CONTRACTOR AFTER LIDL FINISHES FIT OUT OF THE STORE.
- ALL SENSORS FOR BACK OF HOUSE LIGHTING SHALL BE INTEGRAL TO LIGHT FIXTURE.

SHEET KEYNOTES

- EXTERIOR LIGHTING FOR EMERGENCY AND NORMAL LIGHTING.
- LIGHTING AND CONTROLS FOR FREEZER SUPPLIED BY NATIONAL LIGHTING ACCOUNT VENDOR, INSTALLED BY ELECTRICAL CONTRACTOR.
- LIGHTING AND CONTROLS FOR COOLER SUPPLIED BY NATIONAL LIGHTING ACCOUNT VENDOR, INSTALLED BY ELECTRICAL CONTRACTOR.
- REFER TO SHEET E600, DETAIL #4 FOR INSTALLATION DETAILS OF PENDANT MOUNTED EXIT SIGNS.
- ALL FIXTURES IN THIS LINEAR ROW ARE INSTALLED TO BALDUR TRUNK - FOR TRUNK TYPES AND QUANTITIES, REFER TO NORDEON LIGHTING SUBMITTAL.
- INSTALL EMERGENCY BATTERIES FOR EM CANOPY FIXTURES ON THE INTERIOR OF THE BUILDING. INSTALL BATTERIES ABOVE BOTTOM OF JOISTS.
- LIGHTING FOR THE LOADING DOCK WILL BE CONTROLLED VIA MOTION SENSOR AND PHOTOCELL INTEGRAL TO THE FIXTURE WP WALL PACK. CIRCUIT FOR THESE LIGHTING FIXTURES SHALL NOT BE ROUTED THROUGH THE LIGHTING CONTACTOR.
- NOT USED.
- NOT USED.
- ALL LIGHTING CIRCUITRY SHALL BE WIRED BY ELECTRICAL CONTRACTOR SUCH THAT LIGHTING CONNECTORS INSIDE THE ROW ARE NOT EXCEEDING 6A LOAD AT 277V. CONTRACTOR TO COORDINATE POWER DROP LOCATIONS WITH NORDEON.
- LIGHTING FIXTURE IS UNSWITCHED AND STAYS ON 24 HOURS A DAY. EXTEND THE LIGHTING POWER CIRCUITRY AHEAD OF THE CONTROLS FOR THE IDENTIFIED NITE LITE.
- ALL FIXTURES IN THE LINEAR ROW SHALL BE DALI-DIMMABLE DF2 FIXTURE TYPES. THESE FIXTURES SHALL BE CONTROLLED VIA THE LOCAL DAYLIGHT SENSORS VIA A 7LV POWER CABLE AND A DALI CAPABLE BMS. REFER THE WIRING DIAGRAM DETAIL #4 IN SHEET E601.

ISSUANCE

- | NO. | DATE | DESCRIPTION |
|-----|------------|----------------|
| 1 | 12/18/2025 | PERMIT CYCLE 2 |
| 2 | 01/14/2026 | PERMIT CYCLE 3 |
| 3 | 05/28/2026 | CCD 01 |

PROJECT NUMBER

79650191

PROJECT MANAGER

A. HENGSTEBECK

PROFESSIONAL

D. HERSCHER

DRAWN BY

M. GONZALEZ

CHECKED BY

D. HERSCHER



LIGHTING CONTROL SEQUENCE OF OPERATIONS									
ROOM TYPE	SENSOR TYPE	TIMEOUT	TECHNOLOGY	PHOTOCELL	CONTROLLED VIA BMS	SWITCH	EMERGENCY SWITCHED	SWITCHED RECEPTACLES	NOTES
SALES FLOOR	N/A	N/A	N/A	AS REQUIRED BY LOCAL CODE IN DAYLIGHT ZONES.	YES	BMS	SWITCHED	NO	BUILDING MANAGEMENT SYSTEM (BMS) CONTROLS ALL LIGHTS IN SALES FLOOR THROUGH LIGHTING RELAY PANEL. LIGHTS TURN ON AND OFF BASED ON OWNER DEFINED SCHEDULE.
									WHERE REQUIRED BY CODE. DAYLIGHT CONTROL ZONE AUTOMATICALL DIMS BAED ON DAYLIGHT CONTRIBUTION.
BAKERY	N/A	N/A	N/A	NO	YES	BMS	SWITCHED	NO	BUILDING MANAGEMENT SYSTEM (BMS) CONTROLS ALL LIGHTS IN BAKING AREA THROUGH LIGHTING RELAY PANEL. LIGHTS TURN ON AND OFF BASED ON OWNER DEFINED SCHEDULE.
FREEZERS	OCCUPANCY	20	PIR	NO	NO	INTEGRAL TO EQUIPMENT	N/A	N/A	SENSOR PROVIDED BY MANUFACTURER, INSTALLED BY EC.
OFFICE	VACANCY	15	DUAL	NO	NO	TOGGLE	SWITCHED	IF REQ. BY CODE	MANUAL ON, AUTOMATIC OFF.
ELEC/MECH	N/A	N/A	N/A	NO	NO	TOGGLE	SWITCHED	NO	MANUAL ON, AUTOMATIC OFF OPERATION WITH MANUAL DIMMING.
STAGING, STOCKROOM	OCCUPANCY	20	PIR - INTEGRAL TO LUMINAIRE	NO	NO	TOGGLE	SWITCHED	N/A	AUTOMATIC ON/ AUTOMATIC OFF BASED ON OCCUPANCY, WITH LOCAL OVERRIDE TO OFF.
AMENITY HALLWAY	OCCUPANCY	15	PIR	NO	YES	N/A	SWITCHED	NO	AUTOMATIC ON/ AUTOMATIC OFF BASED ON OCCUPANCY. NO LOCAL SWITCH.
RESTROOMS	OCCUPANCY	20	DUAL	NO	NO	KEYED	SWITCHED	NO	AUTOMATIC ON/ AUTOMATIC OFF WITH LOCAL KEYED SWITCH
EXTERIOR LOADING DOCK	OCCUPANCY	20	PIR - INTEGRAL TO LUMINAIRE	INTEGRAL TO LUMINAIRES	NO	SWITCH	NO	NO	AUTOMATIC ON/ AUTOMATIC OFF BASED ON OCCUPANCY, WITH PHOTOCELL OVERRIDE TO OFF DURING DAYTIME HOURS.
EXTERIOR BUILDING MOUNTED	OCCUPANCY	20	N/A	INTEGRAL TO LUMINAIRES	YES	SWITCH	SWITCHED	NO	TIMECLOCK CONTROL THROUGH BMS WITH PHOTOCELL OVERRIDE. ALLOWABLE HOURS OF OPERATION AND SCHEDULING REQUIREMENTS BASED ON LOCAL CODE REQUIREMENTS. DIM LIGHTS 30% WHEN OCCUPANCY NOT DETECTED.
NOTES: 1. FOR ALL SENSOR AND SWITCH DEVICES, PROVIDE QUANTITIES AS SHOWN ON LIGHTING PLANS 2. PROVIDE ONE SWITCH PER ONE CONTROL ZONE, AS SHOWN ON THE LIGHTING PLANS. 3. ALL COMPONENTS SHOWN AND INDICATED ON THIS SCHEDULE, BUT NOT SHOWN ON THE PLAN OR VICE VERSA, SHALL BE INCLUDED AS IF SHOWN ON BOTH. 4. PROVIDE LIGHTING CONTROL PANELS / RELAYS, CABLES, WIRES AND ACCESSORIES AS REQUIRED TO FULFILL THE CONTROL REQUIREMENTS SHOWN ABOVE. 5. CONTROLS ARE BASED ON IECC 2015, WHERE REQUIRED BY CODE. ALL AUTOMATIC DIMMING SHALL BE CONTINUOUS 6. FOR AREAS ON BMS TIMECLOCK, OVERRIDE SWITCHING CAPABLE OF OVERRIDING TIMECLOCK FOR 2 HOURS MAXIMUM. 7. SWITCHED EMERGENCY LIGHTS SHALL BE CONNECTED TO AN EMERGENCY LIGHTING RELAY AND CONTROLLED BY SPACE KEYPAD / SWITCH WHERE APPLICABLE. 8. THIS SEQUENCE OF OPERATIONS IS BASED ON A CENTRAL RELAY PANEL CONTROL OF MAIN SALES FLOOR AND SUPPORT AREAS, WITH STAND ALONE CONTROLS IN TYPICAL BACK OF HOUSE SPACES. GENERAL COMPONENTS INCLUDE TIMECLOCK WITH INTEGRAL OVERRIDE, MANUAL WIRED AND WIRELESS CONTROL POINTS, PHOTOCELLS IN DAYLIT AREAS, OCCUPANCY SENSORS, AND LOAD CONTROLLERS (CONTROL PANELS, OR DISTRIBUTED LOAD CONTROLLERS). CONTROL POINTS AND SENSING DEVICES TO BE LOW VOLTAGE, WITH THE EXCEPTION OF INTEGRATED WALLSWITCH SENSORS.									

LUMINAIRE SCHEDULE							
TYPE	DESCRIPTION	VOLTAGE	MOUNTING	UL/ETL JP Rating	WATTS	MANUFACTURER	CATALOG ORDER NUMBER
BB-2	BALDUR BLIND PLATE <varies>		SUSPEND			NORDEON	BBP-M1.8-WH-BALDUR BLIND PLATE
BB-4	BALDUR BLIND PLATE	0	SUSPEND			NORDEON	BBP-M3.7-WH-BALDUR BLIND PLATE
BB-6	BALDUR BLIND PLATE	0	SUSPEND			NORDEON	BBP-M5.5-WH-BALDUR BLIND PLATE
BB-DIM	BALDUR PHOTOCELL-DAYLIGHT SENSOR	0	SUSPEND			NORDEON	BBP-MINICLIP PHOTOCELL-DAYLIGHT SENSOR
BB-MS	BALDUR MOTION SENSOR	0	SUSPEND			NORDEON	BBP-MINI-P-PP-A-FC-MOTION SENSOR
DF2-4	LINEAR LED	277	SUSPEND			NORDEON	BL 4000LM UNV DF2 3_7FT
DF2-6	LINEAR LED	277	SUSPEND			NORDEON	BL 7000LM UNV DF2 5_5FT
DF2-6 'EM'	LINEAR LED W/ BATTERY BACKUP	277	SUSPEND			NORDEON	BL 7000LM UNV DF2 5_5FT-EMERGENCY BATTERY BACKUP
DF2-8	LINEAR LED	277	SUSPEND			NORDEON	BL 9000LM UNV DF2 7_4FT
DF2-8 'EM'	LINEAR LED W/ BATTERY BACKUP	277	SUSPEND			NORDEON	BL 9000LM UNV DF2 7_4FT-EMERGENCY BATTERY BACKUP
DL4	ROUND LED DOWNLIGHT	277	SURFACE			NORDEON	NCAH2-430/15LE3
DL4 'EM'	ROUND LED DOWNLIGHT W/ BATTERY BACKUP	277	SURFACE			NORDEON	NCAH2-430/15LE3-EMERGENCY BATTERY BACKUP
FP	LED FLATPANEL	277	SURFACE			NORDEON	NFP1-2x2/40W-40K-UNV-WH
FP 'EM'	LED FLATPANEL	277	SURFACE			NORDEON	NFP1-2x2/40W-40K-UNV-WH-EMERGENCY BATTERY BACKUP
SK2	DIRECTIONAL SPOTLIGHT	<varies>	SUSPEND			NORDEON	SK2-45W-UNV-830-WB-BL-DIM
T4	SITE/ROADWAY LUMINAIRE	277	POLE MOUNTED 24'-0" AFF			NORDEON	PAF3-136W-50K-T4-C
T4-V	SITE/ROADWAY LUMINAIRE	277	POLE MOUNTED 24'-0" AFF			NORDEON	PAF3-136W-50K-T4-VISOR
T42	SITE/ROADWAY LUMINAIRE	277	POLE MOUNTED 24'-0" AFF			NORDEON	2@180-PAF3-136W-50K-T4-C
VL	COOLER/FREEZER LIGHTING	277	SURFACE			NORDEON	NVT1-LED-40K-UNV
VL 'EM'	COOLER/FREEZER LIGHTING W. EM BATTERY	277	SURFACE			NORDEON	NVT1-LED-40K-UNV-EMERGENCY BATTERY BACKUP
WP	WALLPACK	277	WALL			NORDEON	PWP1-S/37W-50K-UNV-T4
WP 'EM'	WALLPACK W/ EM BATTERY	277	WALL			NORDEON	PWP1-S/37W-50K-UNV-T4-EMERGENCY BATTERY BACKUP
WP-MS	WALLPACK WITH MOTION SENSOR	277	WALL			NORDEON	PWP1-S/37W-50K-UNV-T4-MSD-MOTION SENSOR
WP-MS 'EM'	WALLPACK W/ EM BATTERY AND MOTION SENSOR	277	WALL			NORDEON	PWP1-S/37W-50K-UNV-T4-MSD-MOTION SENSOR-EMERGENCY BATTERY BACKUP
X1	EXIT SIGN W/ EM BATTERY	277	SURFACE-MOUNTING/ SUSPENSION	YES		NORDEON	NX-812-LED

- NOTES
- 1

THIS LUMINAIRE SCHEDULE IS NOT COMPLETE WITHOUT A COPY OF THE PROJECT MANUAL CONTAINING THE ELECTRICAL SPECIFICATIONS.
- 2

DIMMING CONTROL PROTOCOL (0-10VDC, LINE VOLTAGE, DALI, ETC.) COMPATIBLE WITH LIGHTING CONTROL SYSTEM AS SPECIFIED AND SHOWN ON DRAWINGS.
- 3

PROVIDE +/- 12 INCH ADJUSTABILITY IN AIRCRAFT CABLE LENGTH WHERE USED.
- 4

COORDINATE ALL CEILING TYPES WITH LUMINAIRE LOCATIONS PRIOR TO ORDERING LUMINAIRES. COORDINATE INSTALLATION WITH REFLECTED CEILING PLAN.
- 5

SPECIFIED MANUFACTURERS ARE APPROVED TO SUBMIT BID. INCLUSION DOES NOT RELIEVE MANUFACTURER FROM SUPPLYING PRODUCT AS DESCRIBED.
- 6

PROVIDE SUBMITTALS THAT INCLUDE THE LUMINAIRE, LAMP AND BALLAST INFORMATION OF EACH LUMINAIRE, WITH APPLICABLE OPTIONS CLEARLY CHECKED OR HIGHLIGHTED. SUBMITTALS NOT INCLUDING THIS INFORMATION WILL BE RETURNED AS REJECTED BY THE ENGINEER OF RECORD.
- 7


REMOTE BALLASTS/DRIVERS: UL LISTED FOR THEIR APPLICATION. BALLASTS/DRIVERS MARKED AS UL RECOGNIZED COMPONENT BUT NOT UL LISTED ARE SUBJECT TO REMOVAL AND REPLACEMENT AT NO COST TO OWNER.



5/27/2025 5:00:35 PM Autodesk Docs/77955191 - Lbl 1517 Norcross GA/7955191 Lbl 1517 NORCROSS GA - ELEC-M

LDL US, LLC - LIGHTING CONTACTOR DETAIL

THIS DOCUMENT AND ITS CONTENTS ARE THE PROPERTY OF PROGRESSIVE ARCHITECTURE & PLANNING, LLC. NO PART OF THIS DOCUMENT MAY BE REPRODUCED OR TRANSMITTED IN ANY FORM OR BY ANY MEANS, ELECTRONIC OR MECHANICAL, INCLUDING PHOTOCOPYING, RECORDING, OR BY ANY INFORMATION STORAGE AND RETRIEVAL SYSTEM, WITHOUT PERMISSION IN WRITING FROM PROGRESSIVE ARCHITECTURE & PLANNING, LLC. ALL RIGHTS ARE RESERVED. OTHER RIGHTS MAY BE IN THE COPYRIGHTED MATERIALS.

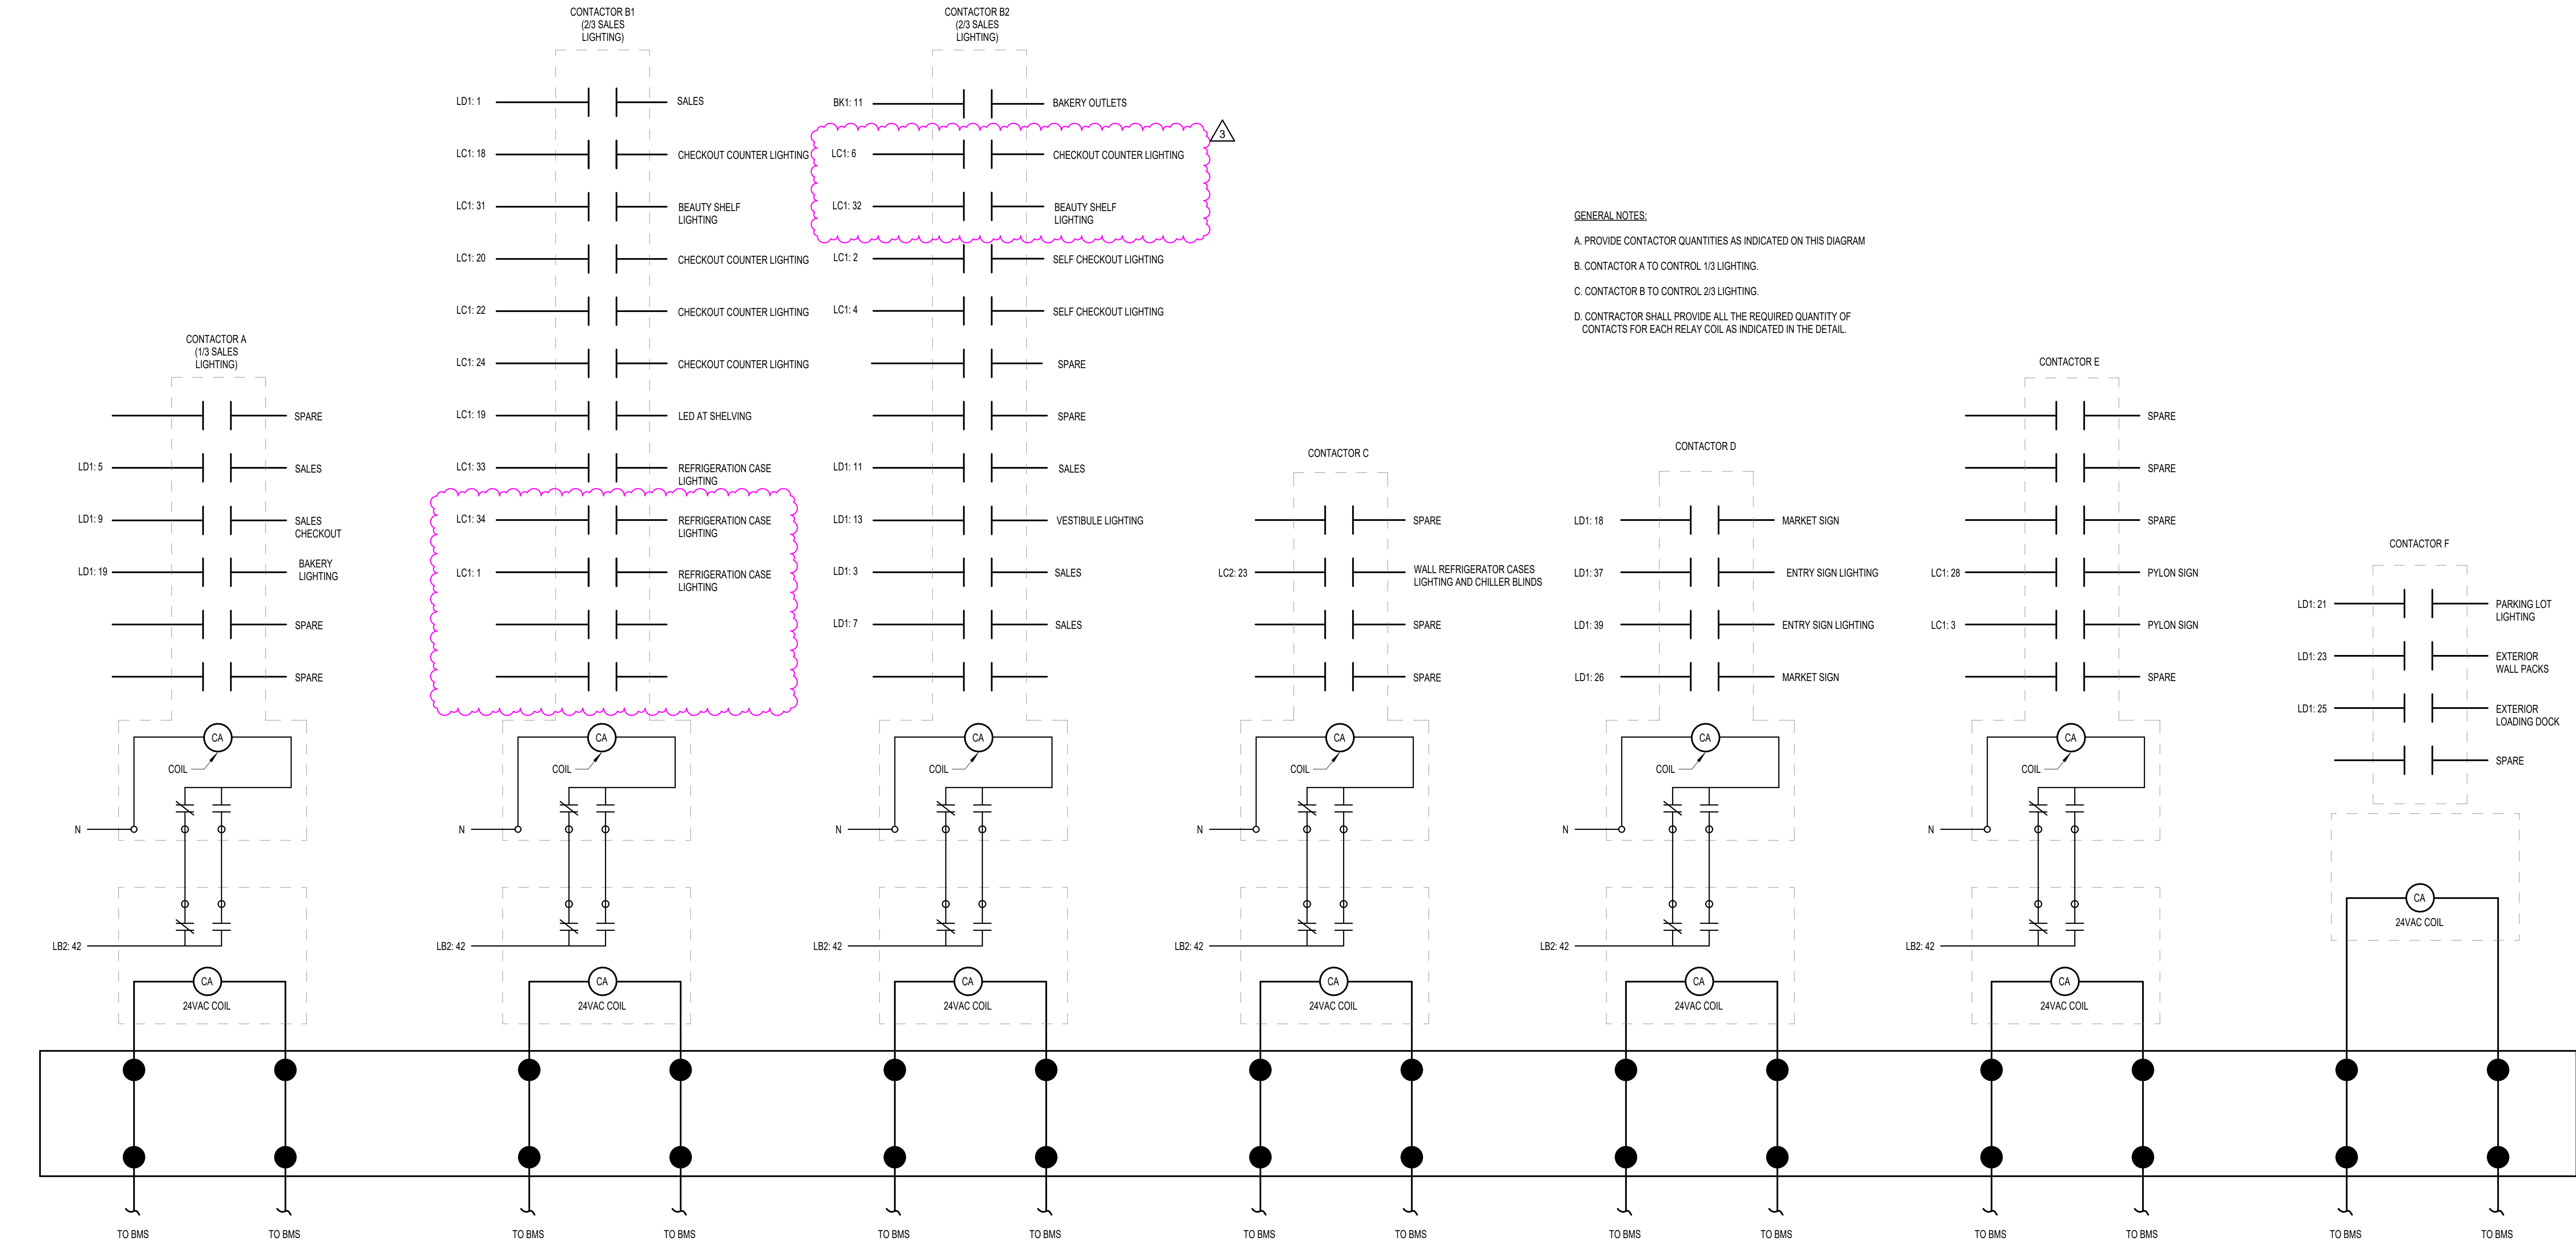

1 LIGHTING CONTACTOR DETAIL

NTS

ISSUANCE		
1	12/18/2025	PERMIT CYCLE 2
2	01/14/2026	PERMIT CYCLE 3
3	05/28/2026	CCD 01

PROJECT NUMBER
7955191
PROJECT MANAGER
A. HENGSTEBECK
PROFESSIONAL
D. HERSCHER
DRAWN BY
M. GONZALEZ
CHECKED BY
D. HERSCHER


ELECTRICAL -
LIGHTING
CONTACTOR
DETAIL
E203

LIDL US, LLC
LIDL 1517 NORCROSS, GA

499 JIMMY CARTER BLVD NORCROSS, GA 30903



PROGRESSIVE ARCHITECTURE ENGINEERING & PLANNING, LLC
**PROGRESSIVE
COMPANIES**
Charlotte, NC | Detroit, MI | Grand Rapids, MI
weareprogressive.com

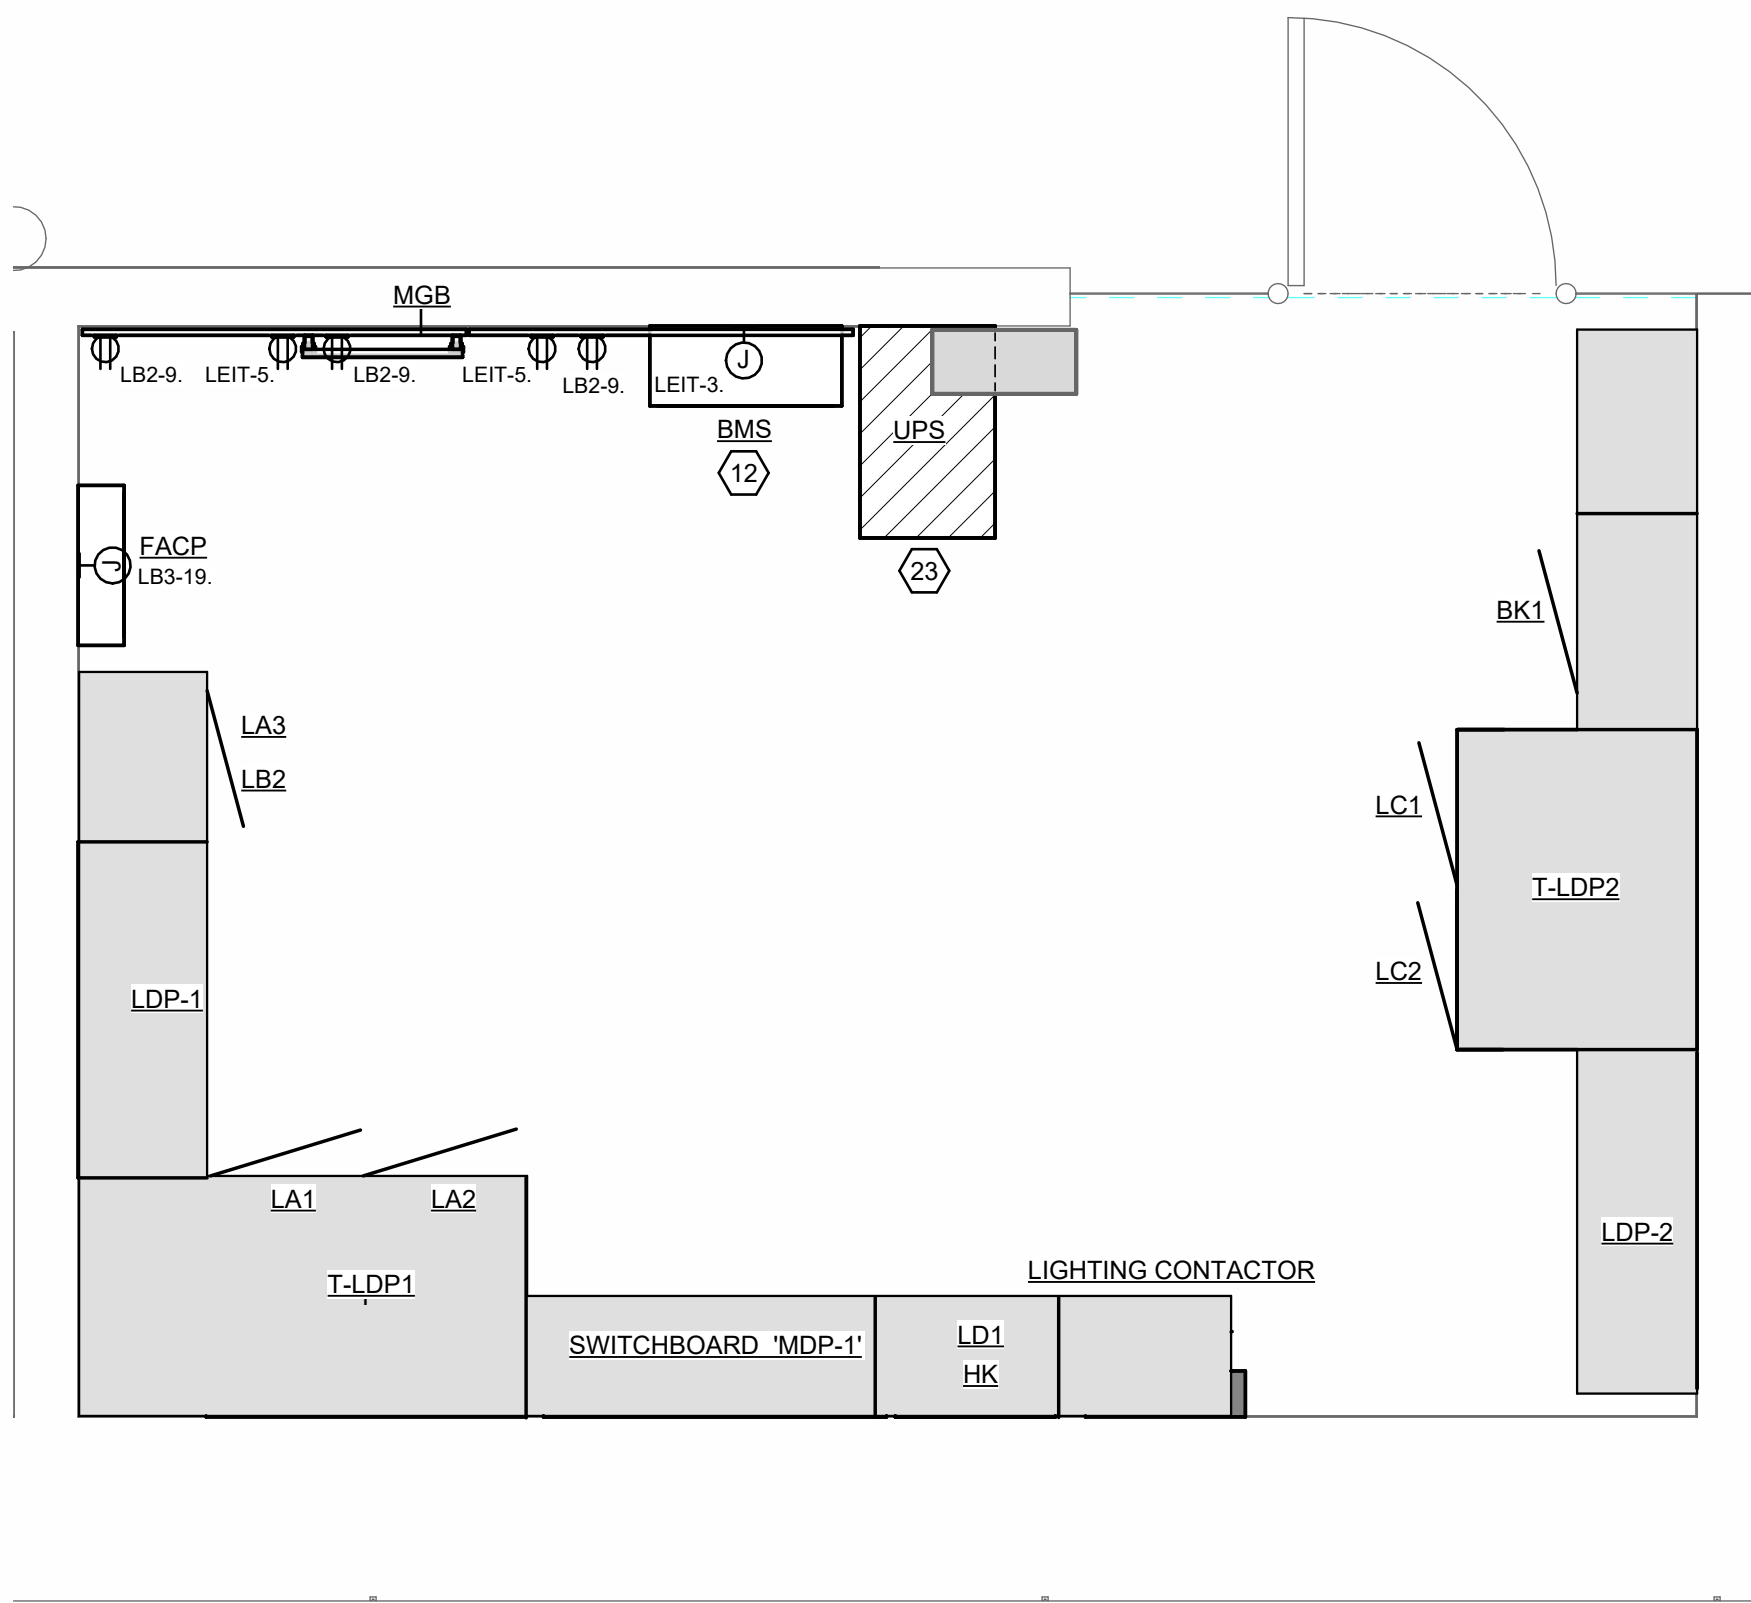


1 TECHNICAL ROOM

0' 4' 8' 16'
1/2" = 1'-0"


3 3D TECHNICAL ROOM

0' 4' 8' 16'
1/4" = 1'-0"

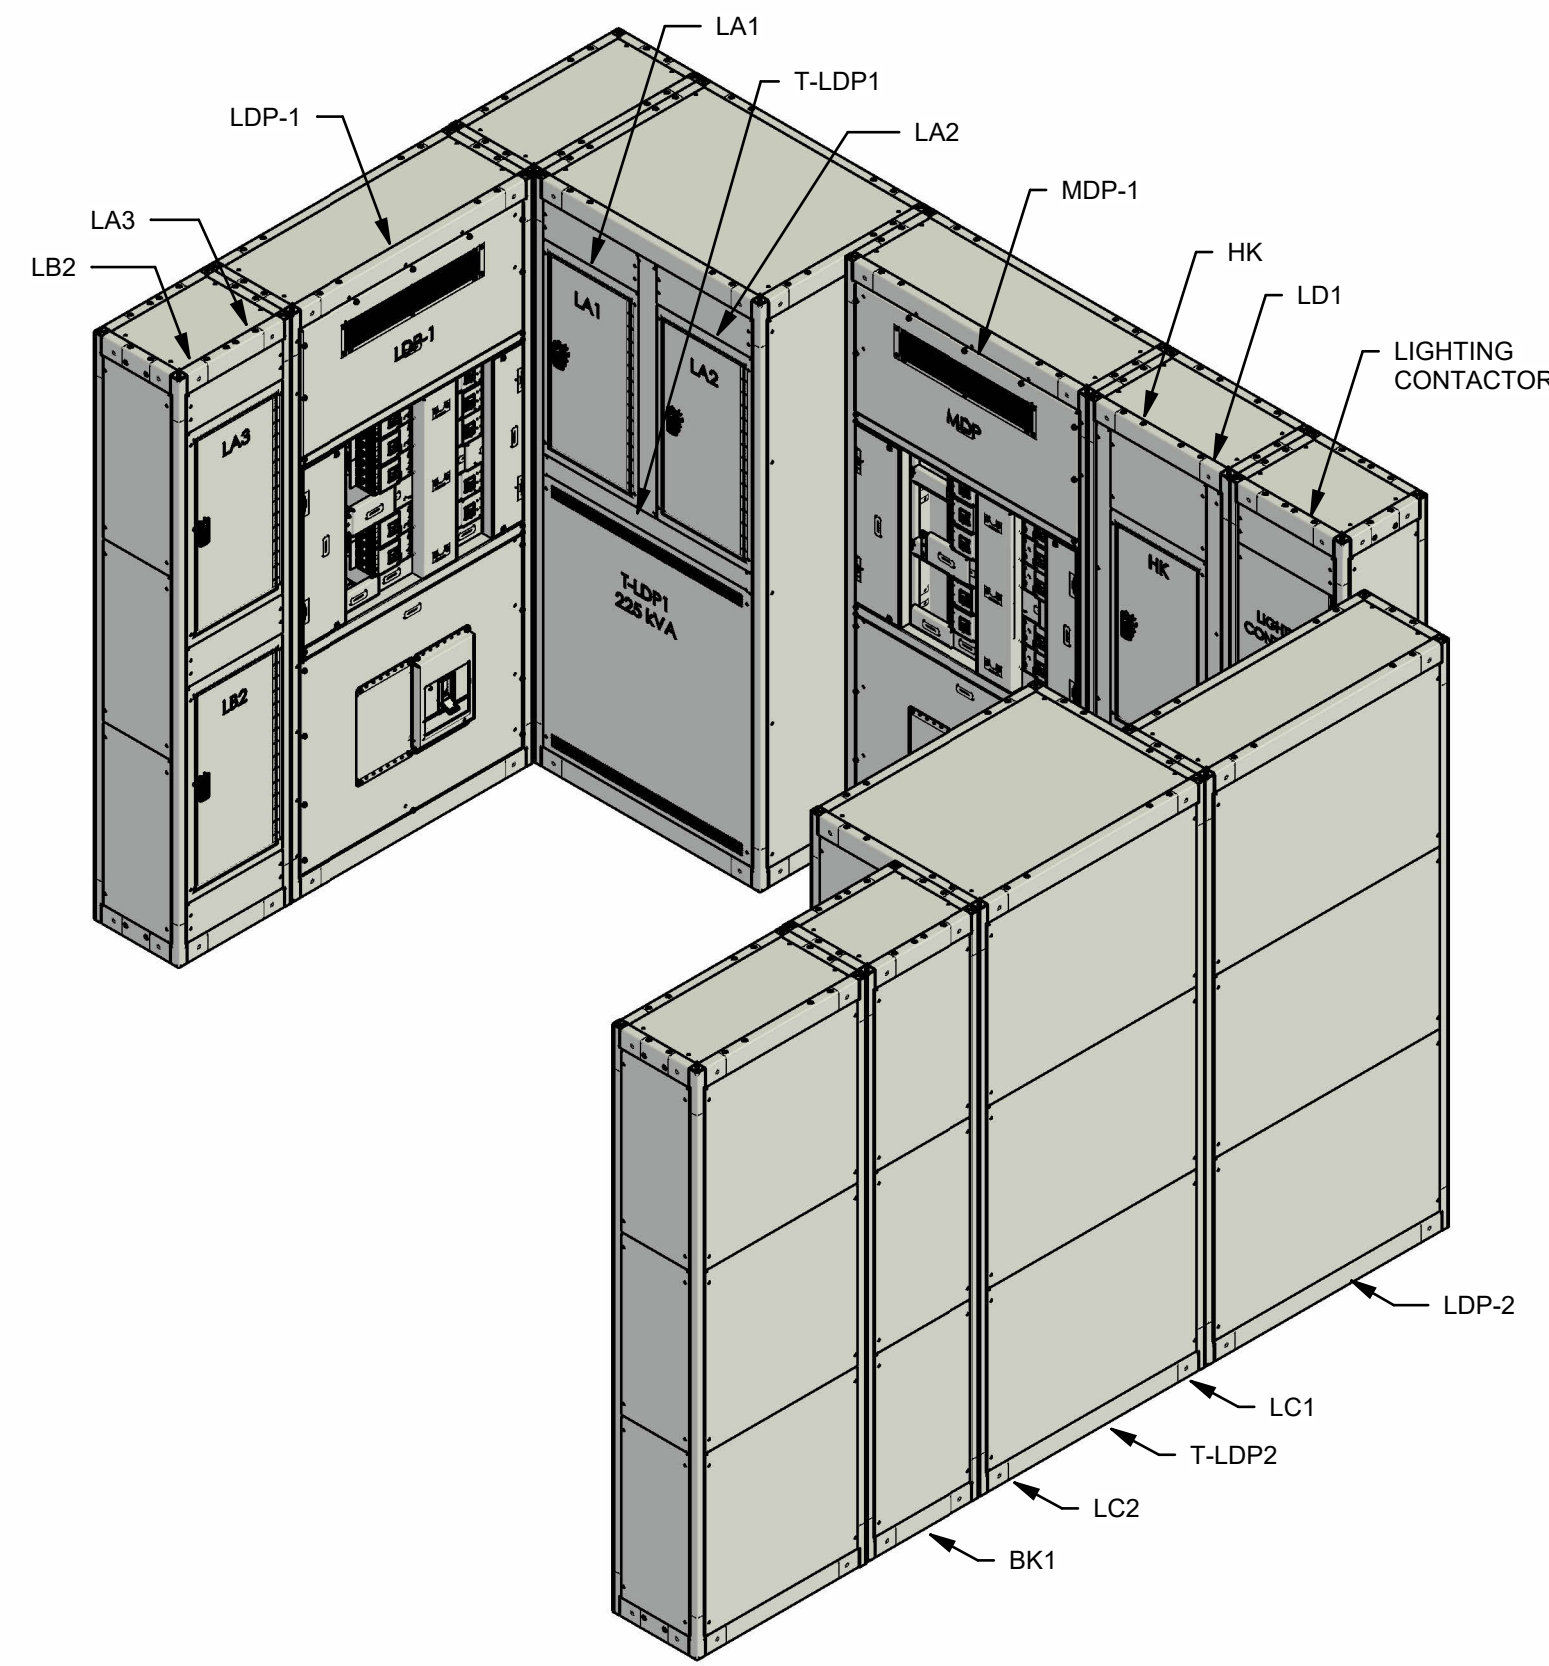


5 GROUND FLOOR - OFFICE/BREAKROOM POWER PLAN

0' 2' 4' 8'
1/4" = 1'-0"

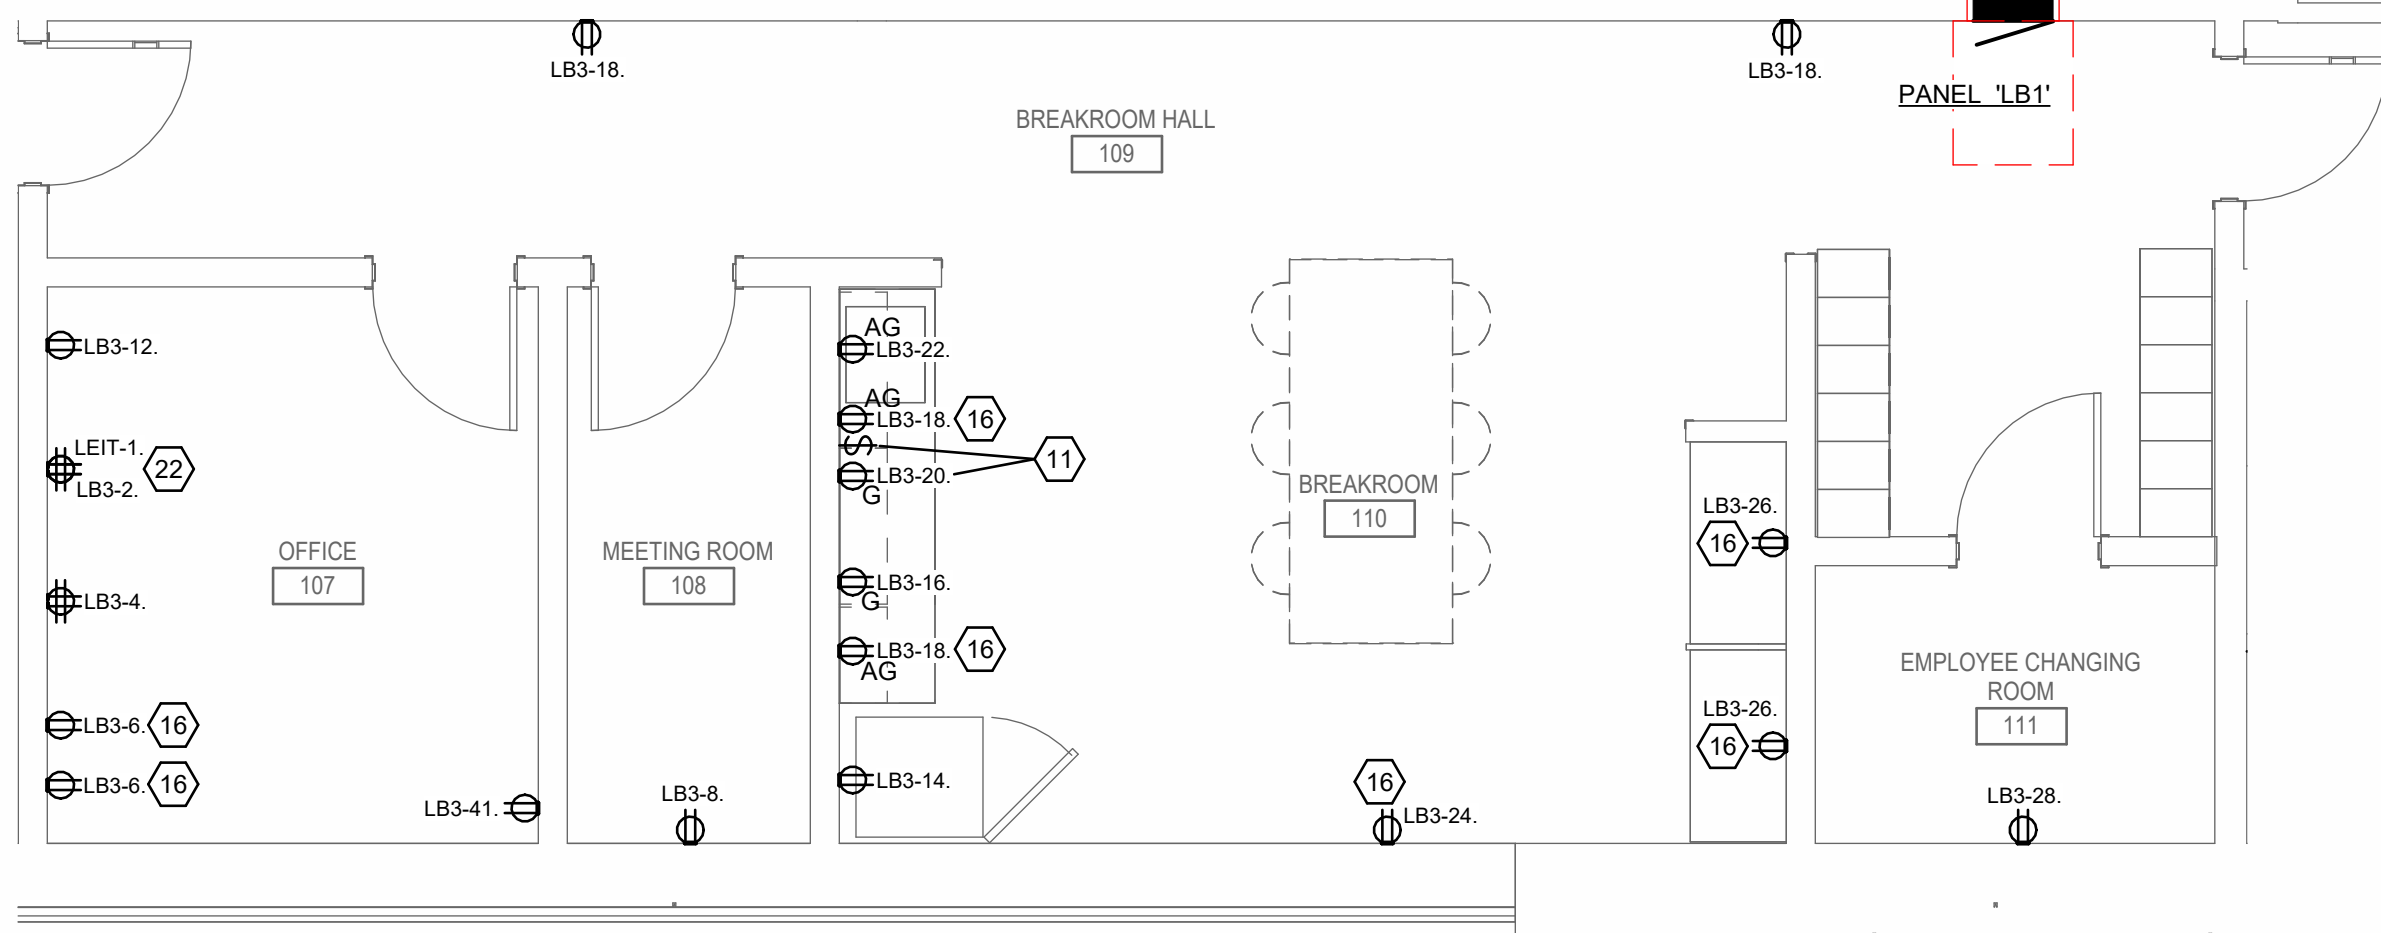


7 IT ROOM

0' 4' 8' 16'
1/2" = 1'-0"

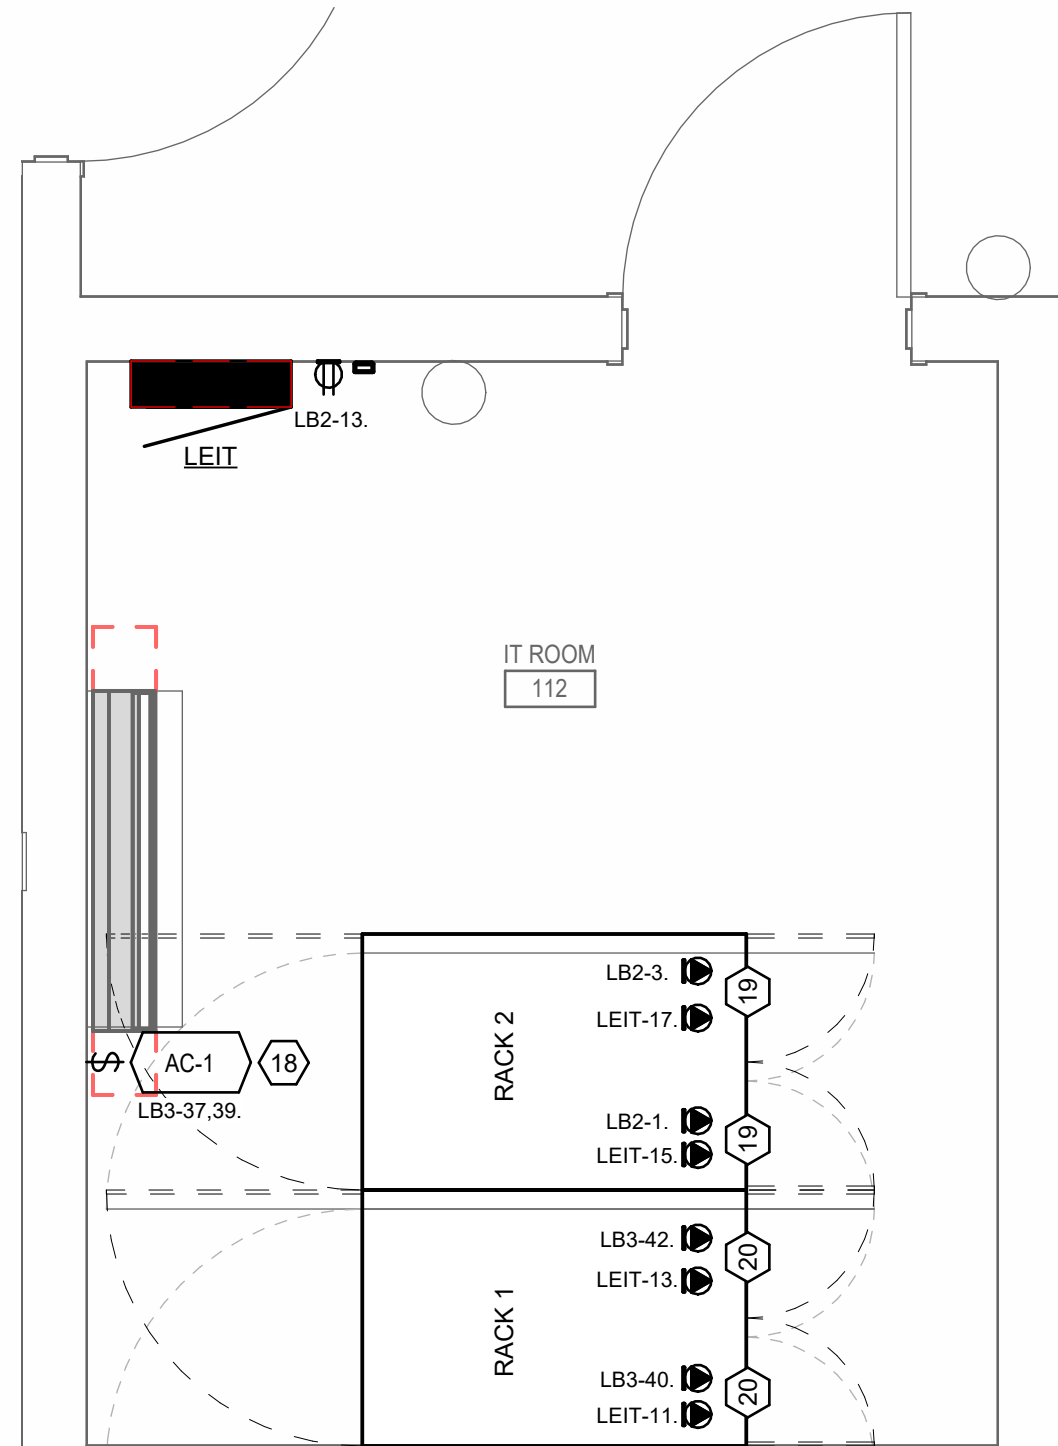


2 SERVICE DISCONNECT AREA

0' 4' 8' 16'
1/4" = 1'-0"

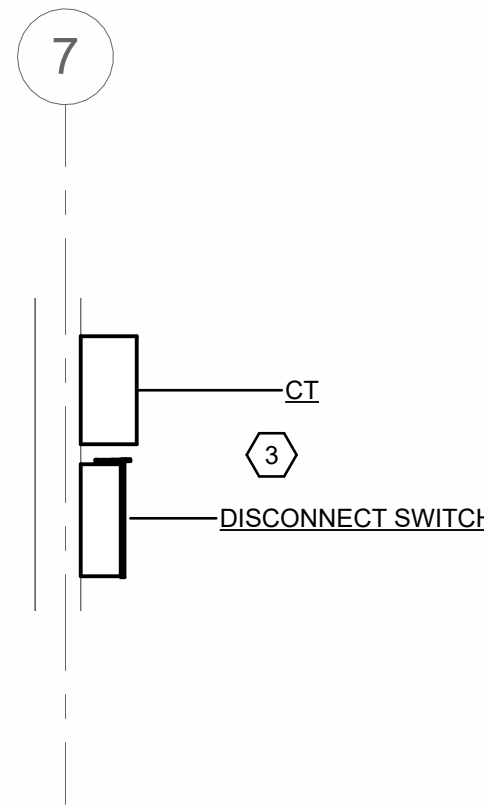

4 BAKERY - ENLARGED POWER PLAN

0' 2' 4' 8'
1/4" = 1'-0"

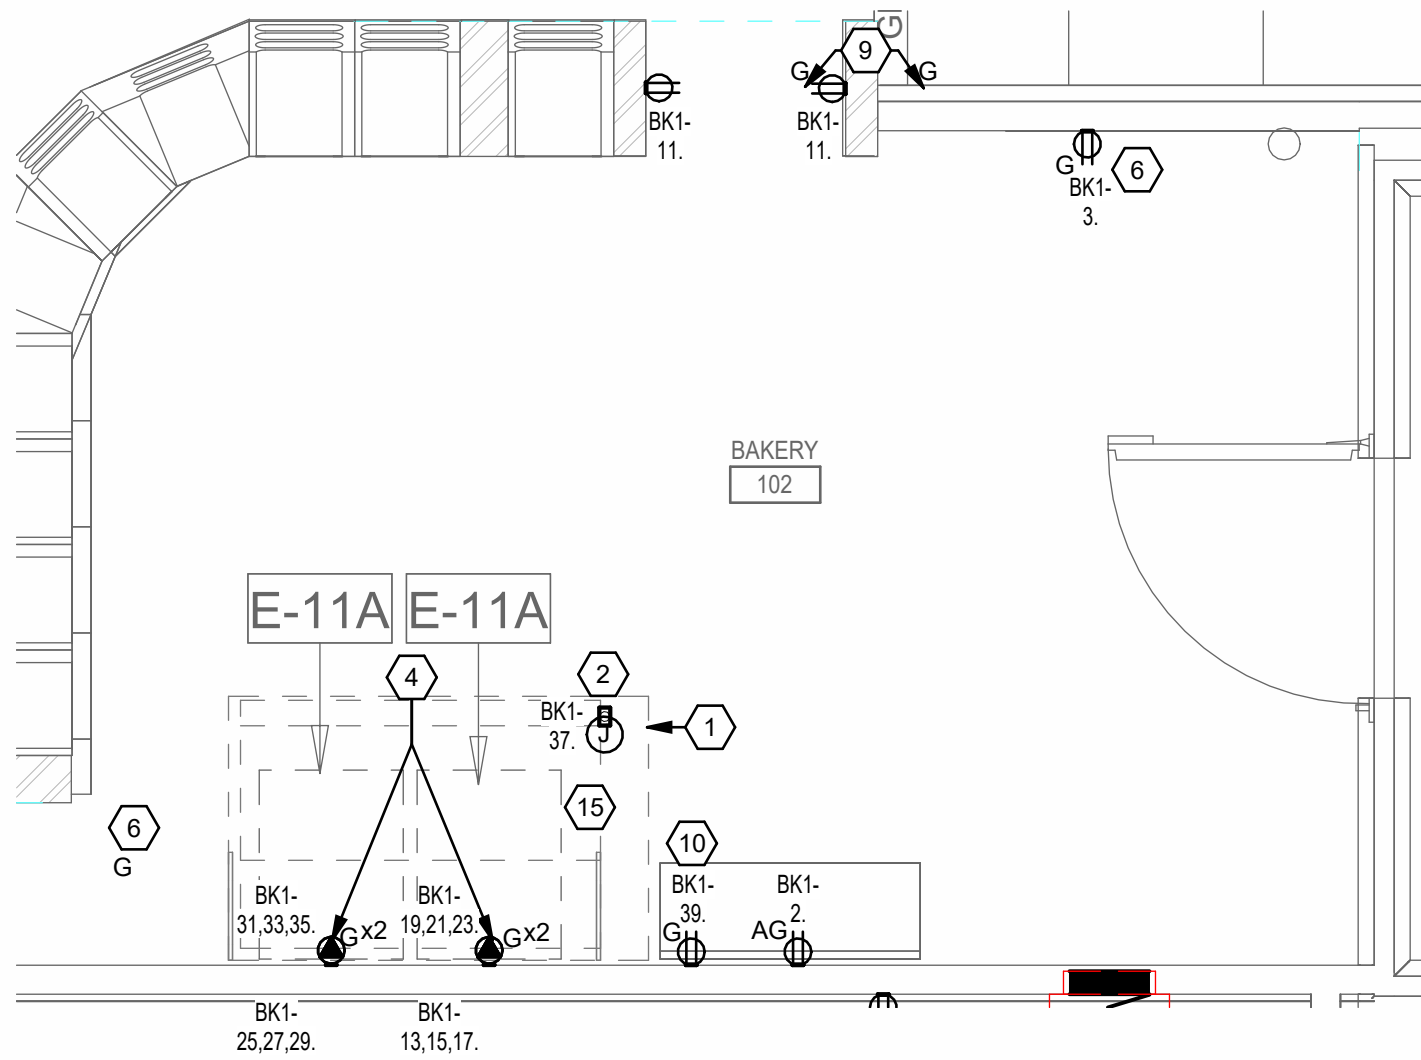

GENERAL SHEET NOTES

- REFER TO SHEET E000 FOR LEGENDS, ABBREVIATIONS AND GENERAL NOTES.
- CONTRACTOR SHALL PROVIDE FACTORY BLUE FINISH WIRING DEVICES FOR ALL UPS OUTLETS FED FROM PANEL "LEIT" IN STORES FOR IDENTIFICATION PURPOSES. COORDINATE WITH ARCHITECTS FOR EXACT DEVICE FINISH PRIOR TO PURCHASE.
- CONTRACTOR SHALL PROVIDE AND INSTALL STAINLESS STEEL COVER PLATES FOR ALL BAKERY OUTLETS. COORDINATE WITH ARCHITECTS FOR COVERPLATE FINISH.
- PROVIDE HOUSEKEEPING PADS FOR ALL FLOOR MOUNTED AND GRADE MOUNTED ELECTRICAL EQUIPMENT.
- SEE SHEET E006 FOR HOOD DETAILS.
- PROVIDE JUNCTION BOX FOR HOOD LIGHTING AND CONTROLS.
- PROVIDE NEMA 3R ENCLOSURES FOR THE CT CABINET AND THE SERVICE DISCONNECT.
- PROVIDE FOUR (4) NEMA 15-60R 250V RECEPTACLES FOR OVEN POWER. ALL RECEPTACLES SHOULD BE CLEARLY LABELED WITH PANEL AND CIRCUIT ID AND AMPERAGE.
- NOT USED.
- PROVIDE RECEPTACLE FOR BUG ZAPPER.
- NOT USED.
- NOT USED.
- CONTROLLED RECEPTACLES IDENTIFIED IN BAKERY SHALL BE POWERED FROM PANEL "BK" VIA RELAY COIL/CONTACTOR -B DEDICATED FOR 2/3 LIGHTING CIRCUITRY.
- POWER FOR BAKERY PRINTER.
- PROVIDE POWER DUPLEX AND ABOVE COUNTER SWITCH FOR GARBAGE DISPOSAL SYSTEM.
- PROVIDE JUNCTION BOX TO POWER BMS PANEL.
- PROVIDE QUADRECEPT FOR HEADSET CHARGING STATION.
- NOT USED.
- PROVIDE A SHUNT TRIP DEVICE FOR ALL RECEPTACLES AND EQUIPMENT LOCATED UNDER THE HOOD.
- PROVIDE QUAD RECEPTACLE IN PLACE OF DUPLEX. ONE HALF OF QUAD TO BE CONTROLLED BY OCCUPANCY SENSOR. PROVIDE DARK GREY DUPLEX RECEPTACLES TO DIFFERENTIATE FROM NON-SWITCHED RECEPTACLES OF CONTROLLED QUADRAPLEX RECEPTACLES.
- NOT USED.
- FLUSHMOUNT TOGGLE SWITCH FOR AC UNIT ON DRYWALL.
- MOUNT FOUR NEMA L5-20 TWISTLOCK RECEPTACLES FOR IT RACK-1 ON UNISTRUT SUPPORTS 0'-8" FROM CABLE TRAY AT MATCHED ELEVATION OF CABLE TRAY ABOVE RACKS. CIRCUIT (2) RECEPTACLES ON UPS POWER, AND (2) RECEPTACLES ON NORMAL POWER AS INDICATED ON PLAN.
- MOUNT FOUR NEMA L5-30 TWISTLOCK RECEPTACLES FOR IT RACK-2 ON UNISTRUT SUPPORTS 0'-8" FROM CABLE TRAY AT MATCHED ELEVATION OF CABLE TRAY ABOVE RACKS. CIRCUIT (2) RECEPTACLES ON UPS POWER, AND (2) RECEPTACLES ON NORMAL POWER AS INDICATED ON PLAN.
- NOT USED.
- MOUNT (1) UPS POWER QUADRAPLEX ABOVE COUNTER AT 3'-6" AND (1) UTILITY POWER DUPLEX BELOW COUNTER AT 1'-6".
- SO CORD TO BE USED IN LIEU OF METAL CONDUIT.

ISSUANCE
1 12/18/2025 PERMIT CYCLE 2

PROJECT NUMBER
7955101
PROJECT MANAGER
A. HENGSTEBECK
PROFESSIONAL
D. HERSCHER
DRAWN BY
M. GONZALEZ
CHECKED BY
D. HERSCHER

ENLARGED
ELECTRICAL
DRAWINGS
E300

LIDL US, LLC
LIDL 1517 NORCROSS, GA

499 JIMMY CARTER BLVD. NORCROSS, GA 30093

PROGRESSIVE ARCHITECTURE ENGINEERING & PLANNING, LLC
PROGRESSIVE
COMPANIES
Charlotte, NC | Detroit, MI | Grand Rapids, MI
weareprogressive.com




GENERAL SHEET NOTES

- A. REFER TO SHEET E000 FOR LEGENDS, ABBREVIATIONS AND GENERAL NOTES.


SHEET KEYNOTES

- PROVIDE WHITE 2X2 POWER POLE AS MANUFACTURED BY WIREMOLD. CATALOG NUMBER 25DTC. WITH EXTENSIONS 25DTC AS REQUIRED. SECURE POWER POLE TO JOIST ABOVE. REFER TO CONDUIT ROUTING DRAWING E102 FOR CONNECTION TO POWER AND TECHNOLOGY INFRASTRUCTURE.
- POWER FOR TV MONITORS. INSTALL 3/4" FLEXIBLE CONDUIT THROUGH MULLION FOR POWER UNLESS OTHERWISE NOTED. INSTALL JUNCTION BOXES AND CONDUIT ON TOP OF STRUCTURE. COORDINATE EXACT LOCATION WITH ARCHITECT.
- ELECTRICAL CONTRACTOR TO PROVIDE WIRING FOR (3) FACTORY INSTALLED SURFACE MOUNTED RECEPTACLES PROVIDED WITH CHECKLANES. (1) DUPLEX & (1) QUAD. ARE COLORED ORANGE AND SHALL BE CONNECTED TO UPS POWER. (1) DUPLEX IS COLORED BROWN AND SHALL BE CONNECTED TO UTILITY POWER. CONTRACTOR TO PROVIDE WHITE COLORED SURFACE MOUNTED QUAD RECEPTACLE FOR LIGHTING IN POS CONSOLE - POWER WIRING FOR WHITE COLORED QUAD RECEPTACLE. UTILIZE TYPE "MC" CABLE
- PROVIDE (1) DUPLEX RECEPTACLE ON UPS POWER AND (1) RECEPTACLE ON UTILITY POWER FOR 2/3 LIGHTING WHEN SHOWN. ALL RECEPTACLES SHALL BE INTEGRAL TO THE 4000 WIREMOLD AT EACH SELF-CHECKOUT POS. FLEXIBLE CONDUIT TO FEED CABLES FROM CABLE TRAY TO POWER POLE WHEN NEEDED. REFER TO ARCH DRAWINGS DETAIL FOR ADDITIONAL INFORMATION.
- CONNECTION BETWEEN RECEPTACLES TO BE MADE WITH RIGID CONDUIT.
- CONNECTION BETWEEN RECEPTACLES TO BE MADE WITH FLEX CONDUIT.
- PROVIDE NEMA L21-20R RECEPTACLES FOR INSIGHT ID6SU-8W AND ID6SU-12W REFRIGERATION UNITS. PROVIDE NEMA L21-20P PLUG CORDS FOR FIELD WIRING OF REFRIGERATION UNITS.
- WALL MOUNTED WIREMOLD 4000 RACEWAY AT FLOOR LEVEL. POWER ROUTED FROM WALL CAVITY AND OUT TO HORIZONTAL RACEWAY. PROVIDE WIREMOLD FITTING TO CAVITY WITHIN FINISH WALL.
- WIREMOLD WHITE POWERPOLE 25DTC. POLES INSTALLED AFTER CHECKOUTS & SELF CHECKOUT ATTENDANT STATION ARE IN PLACE.


- CONTRACTOR TO PROVIDE WIREMOLD WHITE POWERPOLE 25DTC AND RECEPTACLE FOR DRINK CHILLER.
- PROVIDE NEMA L21-20R RECEPTACLES FOR RL-3W FREEZER UNITS. PROVIDE NEMA L21-20P PLUG CORDS FOR FIELD WIRING OF FREEZER UNITS. ELECTRICAL CONTRACTOR TO COORDINATE FINAL LOCATION WITH REFRIGERATION MANUFACTURER DRAWINGS.
- PROVIDE NEMA L21-30R RECEPTACLES FOR RL-5W FREEZER UNITS. PROVIDE NEMA L21-30P PLUG CORDS FOR FIELD WIRING OF FREEZER UNITS. ELECTRICAL CONTRACTOR TO COORDINATE FINAL LOCATION WITH REFRIGERATION MANUFACTURER DRAWINGS.
- PROVIDE WALL MOUNTED DUPLEX RECEPTACLE FOR ELECTRIC SECURITY GATES. MOUNT AT 12'-8" AFF.
- JOIST MOUNTED RECEPTACLE FOR PVM.
- FLOOR RECEPTACLES FOR STORE EQUIPMENT LED LIGHTS.
- PROVIDE (1) DUPLEX RECEPTACLE ON UPS POWER AND (1) RECEPTACLE ON UTILITY POWER FOR 2/3 LIGHTING WHEN SHOWN. ALL RECEPTACLES SHALL BE RECESSED INTO WALL AND MOUNTED AT 0'-8" AFF. REFER TO ARCH DRAWINGS DETAIL FOR ADDITIONAL INFORMATION.
- PROVIDE (1) DUPLEX RECEPTACLE ON UPS POWER FOR SELF CHECKOUT STATION ATTENDANT. RECEPTACLE SHALL BE INTEGRAL TO THE 4000 WIREMOLD AT EACH SELF CHECKOUT STATION ATTENDANT STATION. FLEXIBLE CONDUIT TO FEED CABLES FROM CABLE TRAY TO POWER POLE WHEN NEEDED.
- WIREMOLD 4000 RACEWAY MOUNTED TO PARTITION WALL. PROVIDE WIREMOLD FITTING TO CONNECT TO POWER POLE.

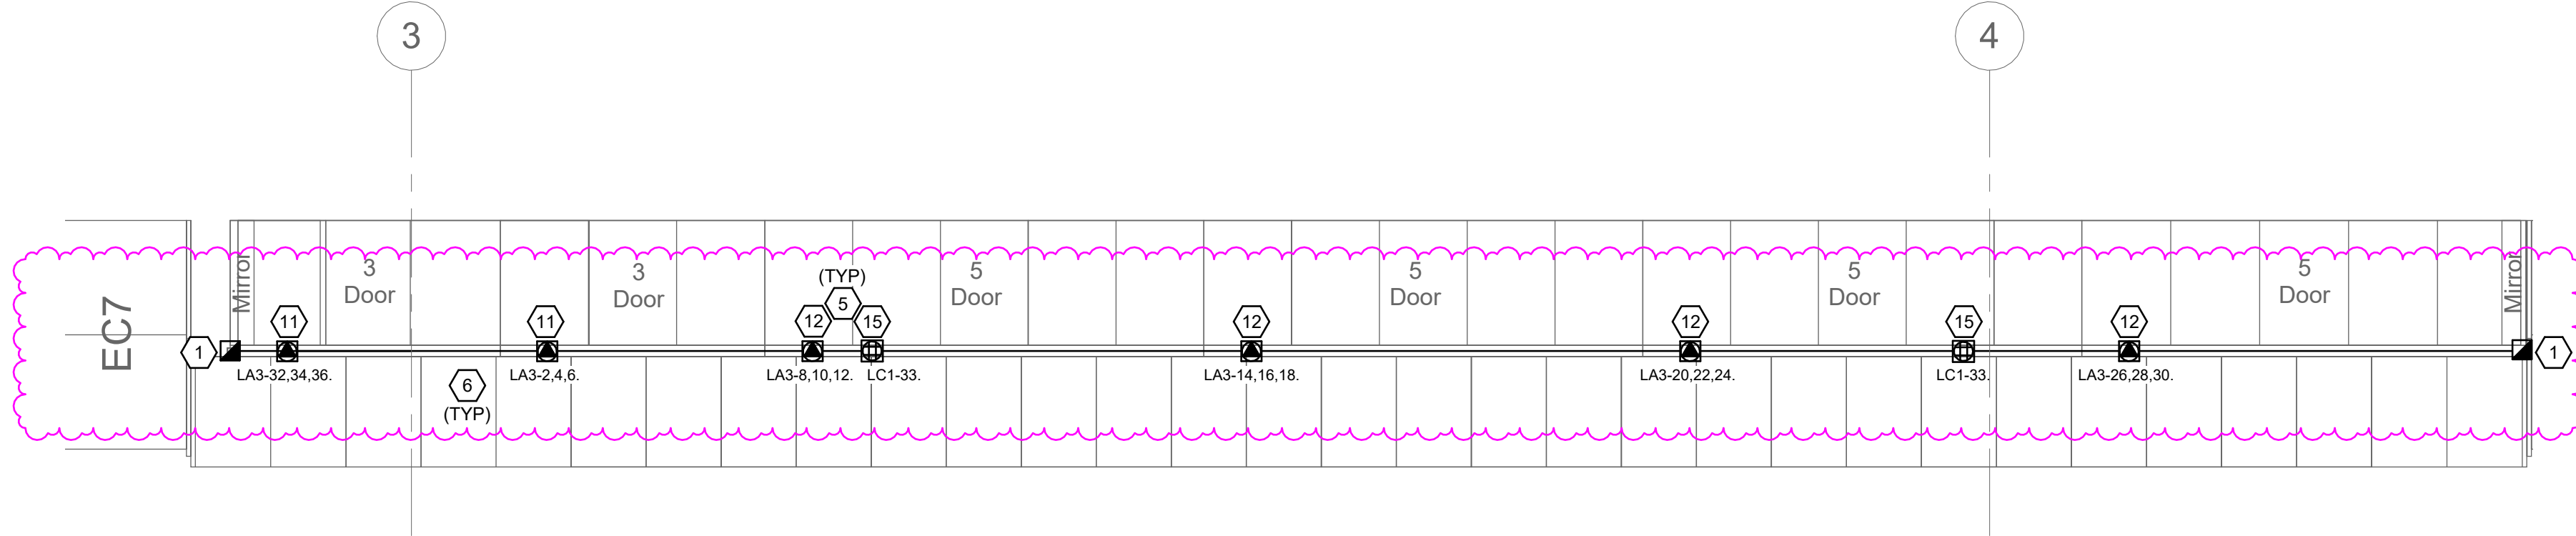


2 ENLARGED ELECTRICAL DRAWING - REFRIGERATION 2

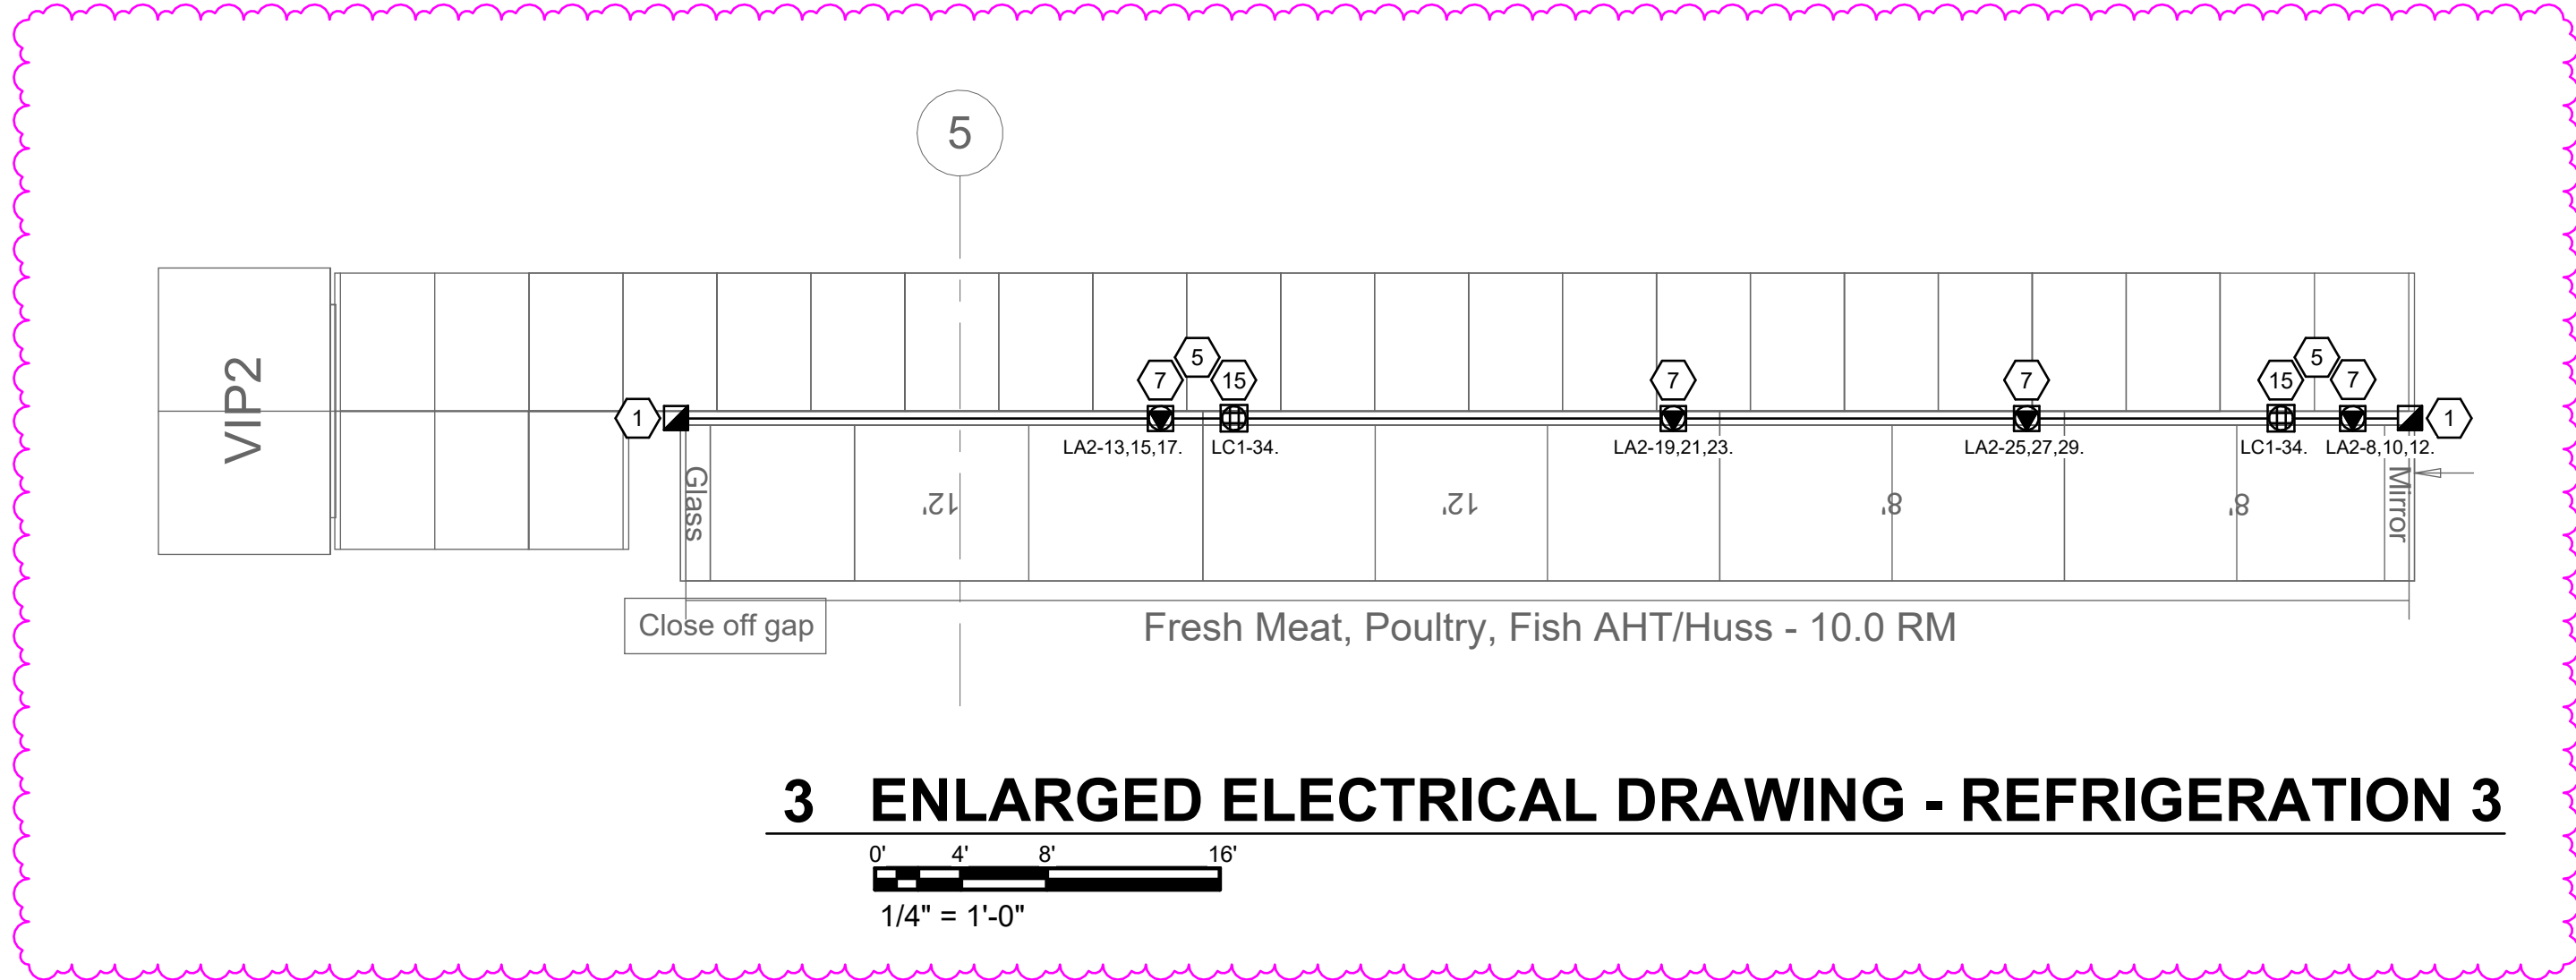

3 ENLARGED ELECTRICAL DRAWING - REFRIGERATION 3

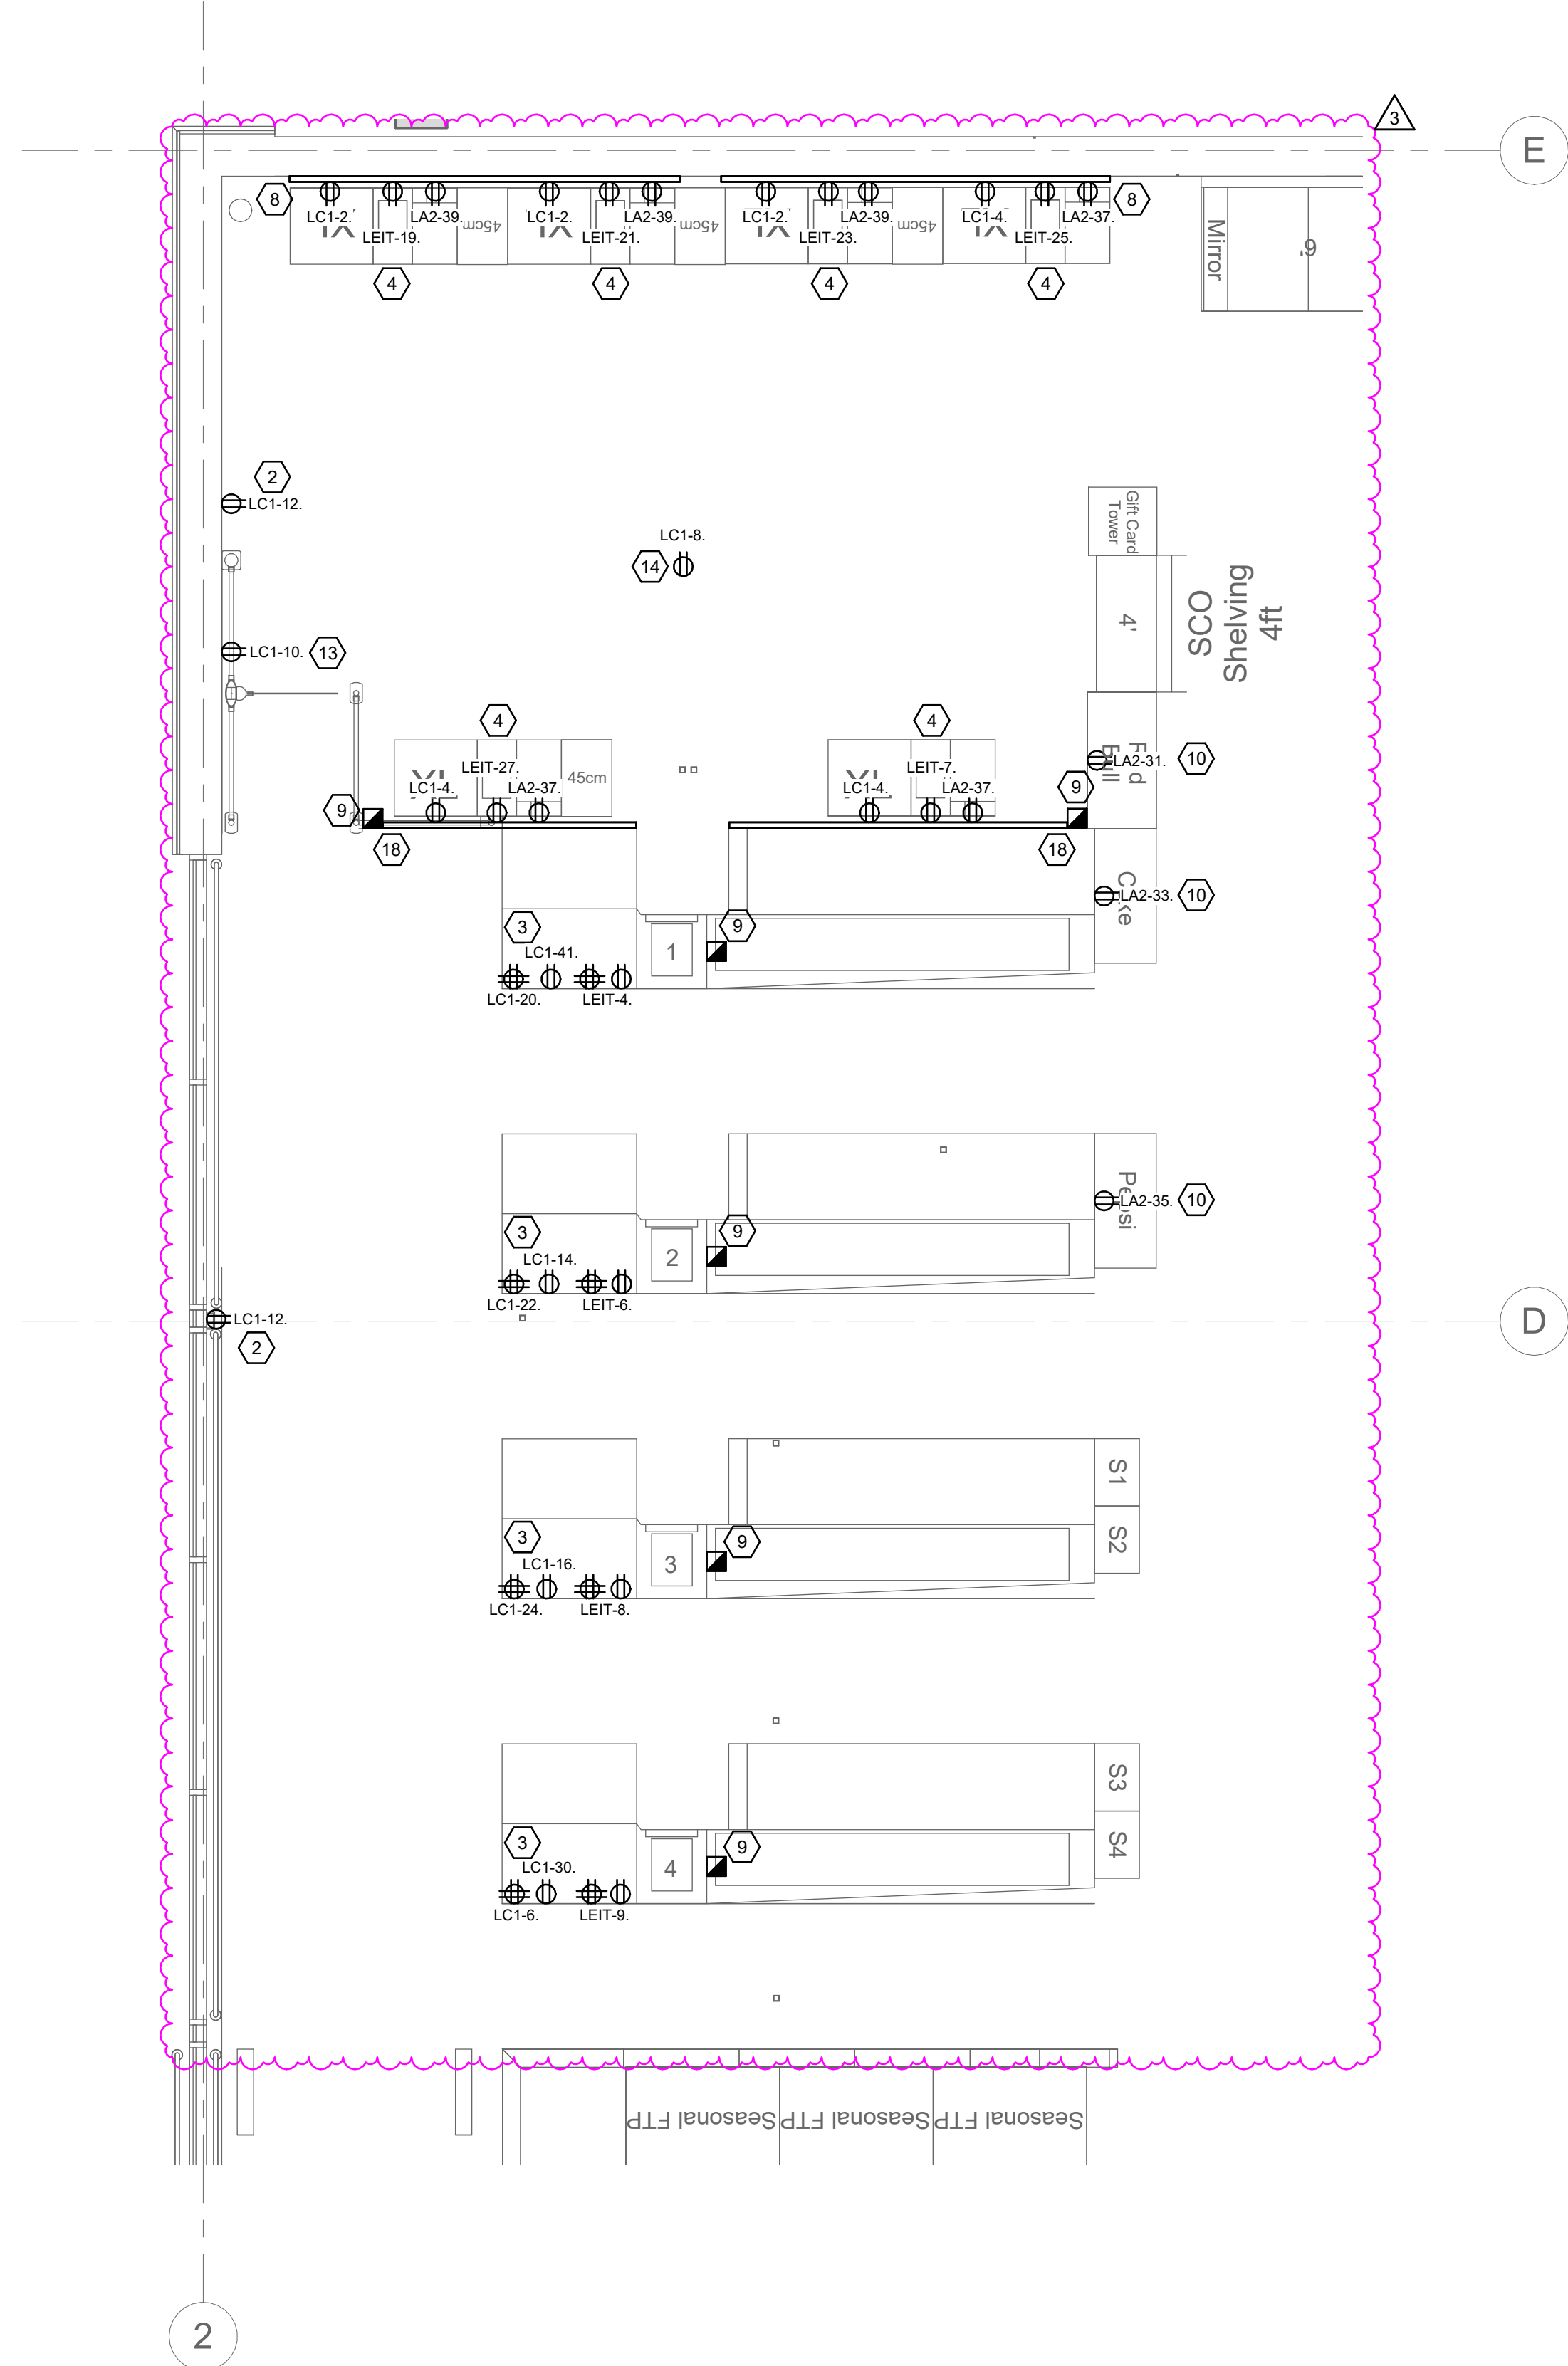

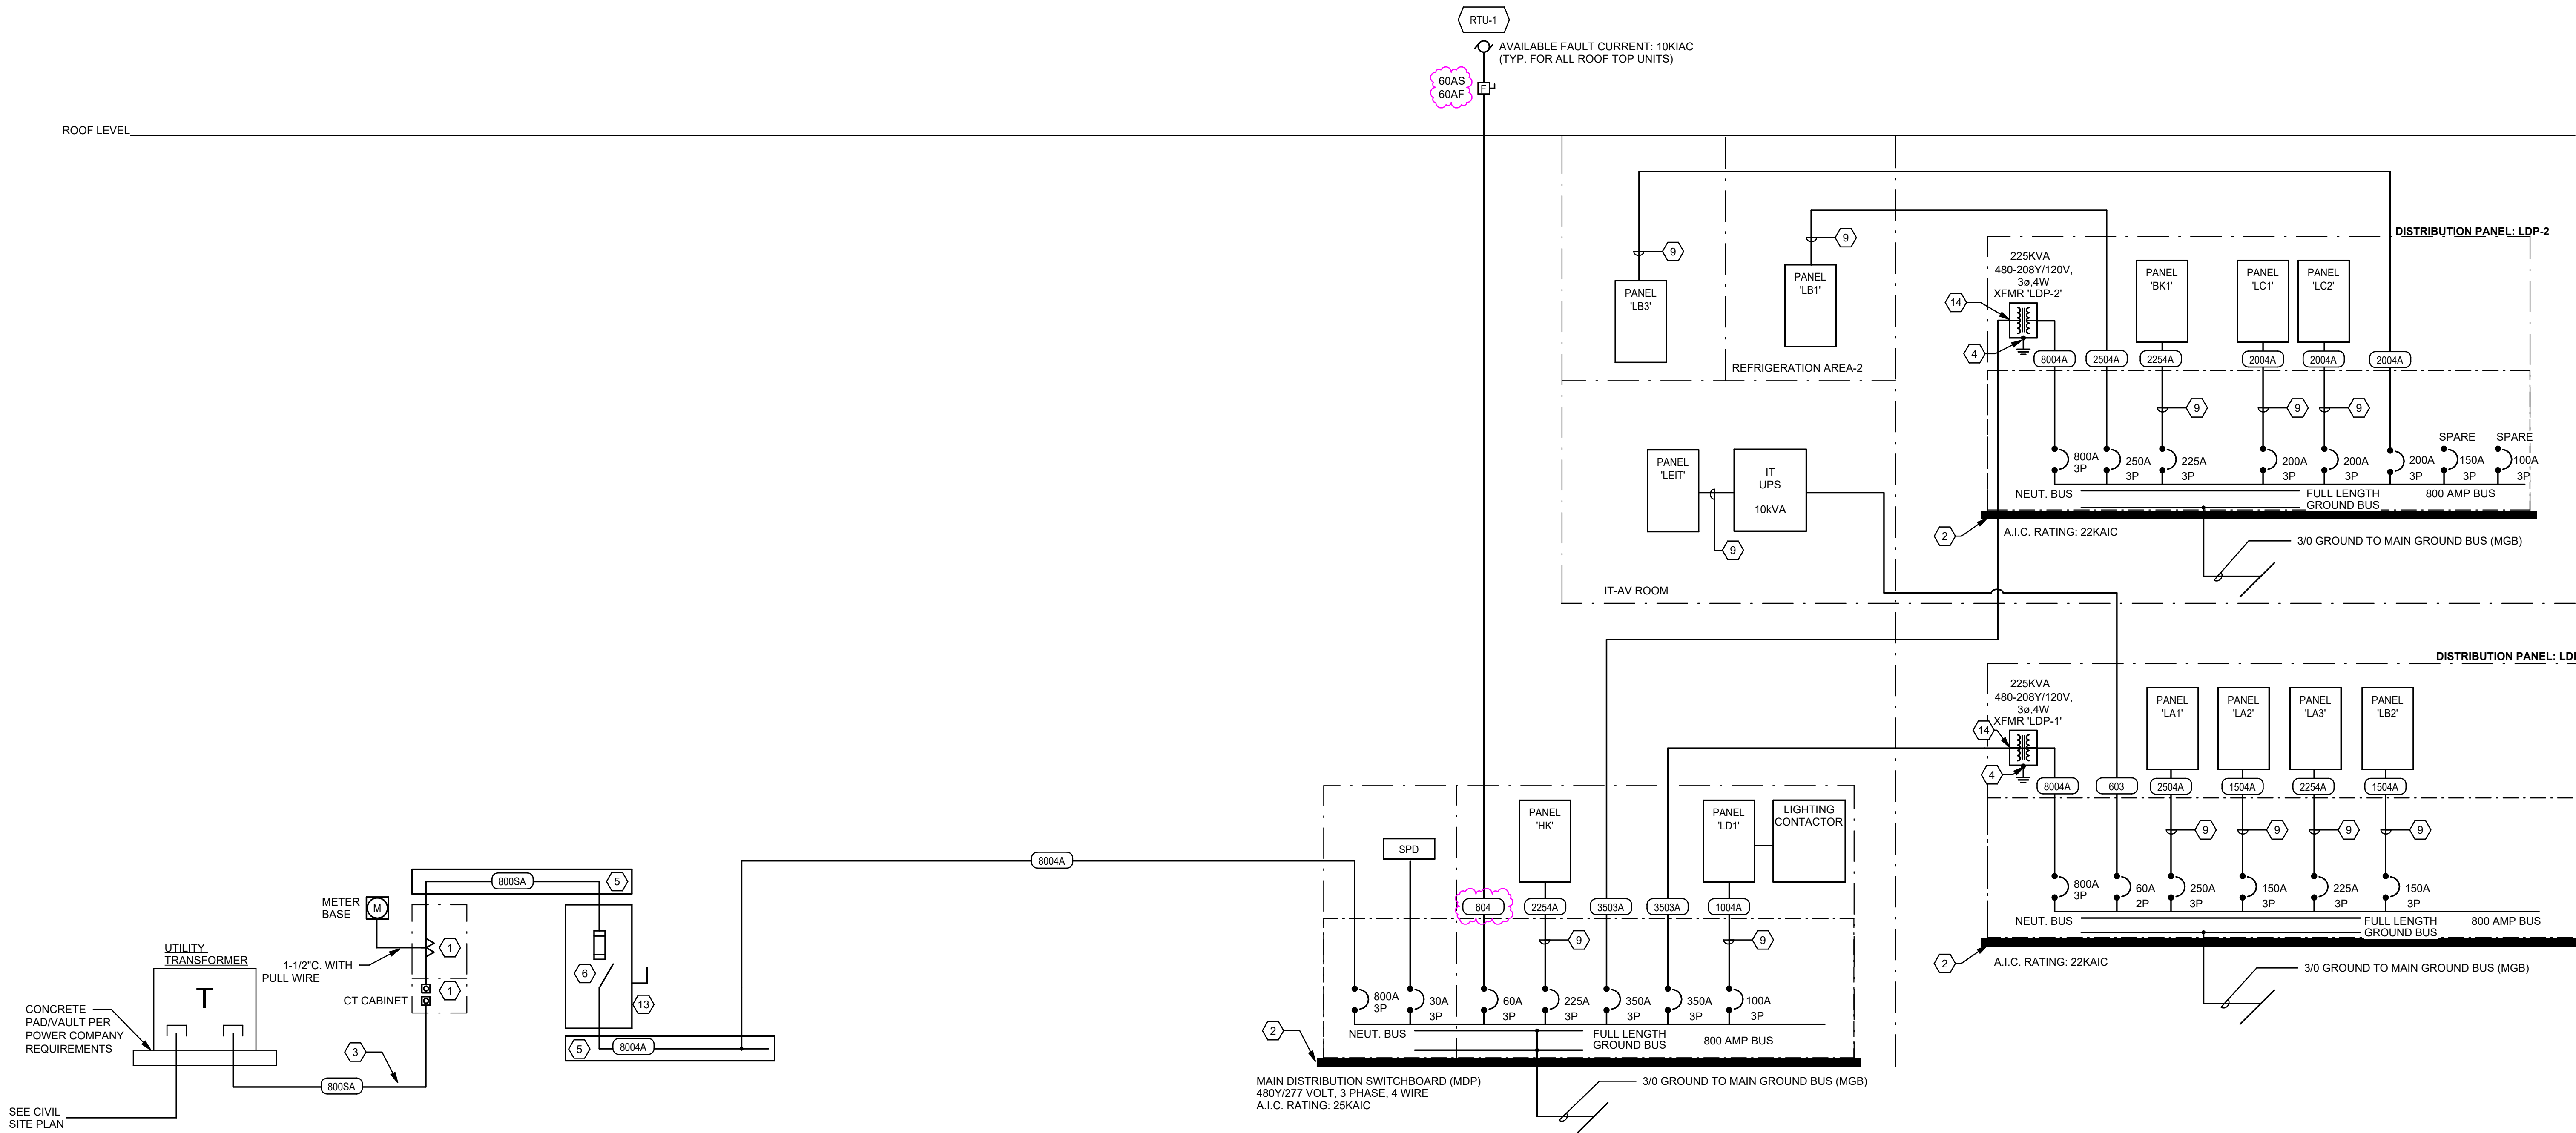

1 ONE-LINE POWER DISTRIBUTION DIAGRAM

NO SCALE

GENERAL SHEET NOTES

- REFER TO SHEET E000 FOR LEGENDS, ABBREVIATIONS AND GENERAL NOTES.
- REFER TO PANEL SCHEDULES FOR EXACT SPACES AND SPARE BREAKER QUANTITIES.
- INSTALL FEEDER FROM TRANSFORMER TO SECONDARY TO MAIN BREAKER IN SWITCHBOARD/PANEL, NOT TO EXCEED 25 FEET PER NEC 240.21(C)(6).
- ALL CIRCUIT BREAKERS 200A AND HIGHER A SHALL BE ELECTRONIC TRIP WITH LSI FUNCTIONS.

SHEET KEYNOTES

- PROVIDE CURRENT TRANSFORMER/TERMINAL CABINET PER POWER UTILITY REQUIREMENTS. PROVIDE 4/0 BONDING JUMPER TO CABINET AND METER.
- PROVIDE 3-1/2 INCH HIGH CONCRETE HOUSEKEEPING PAD UNDER TRANSFORMER/SWITCHBOARD.
- CONTRACTOR SHALL VERIFY AND PROVIDE SERVICE CONDUITS/CONDUCTORS AS PER POWER UTILITY REQUIREMENTS FOR INCOMING SERVICE.
- CONNECT GROUNDING ELECTRODE CONDUCTOR FROM TRANSFORMER GROUNDING LUG TO AVAILABLE GROUNDING ELECTRODES PER NEC 250.30 AND 250.104. FOR FEEDER SIZING REFER TO DETAIL 6/E000.
- PROVIDE NEMA 3R WIRE TROUGH AS PER NEC 376.
- PROVIDE NEMA 3R, 600V, 800A/800AF SERVICE DISCONNECT. INSTALL AS PER LOCAL UTILITY REQUIREMENTS.
- NOT USED.
- NOT USED.
- PROVIDE ENERGY METERING AT ALL LOADS LISTED ON METERING DETAIL. ENERGY METERING SHALL BE INSTALLED TO COMPLY WITH LOCAL ADOPTION OF IEC 603. PROVIDE CTs SIZED FOR EACH FEEDER AND ENERGY SUB METER. ALL ENERGY METERING SHALL BE PROVIDED TO INTERFACE WITH BMS SYSTEM AND PROVIDED TO FACILITATE THE COLLECTION OF DATA FOR EACH BUILDING ENERGY USE CATEGORY (SEE METERING DETAIL FOR CATEGORY AND MONITORING OF INDIVIDUAL CIRCUITS):
 - HVAC TOTAL SYSTEM ENERGY USE.
 - LIGHTING SYSTEM TOTAL ENERGY USE.
 - BAKERY OVENS ENERGY USE.
 - REFRIGERATION CASES & DRY COOLERS TOTAL ENERGY USE.
 - WALK-IN FREEZER & COOLER TOTAL ENERGY USE.
 - TOTAL BUILDING ENERGY USE.

CONTRACTOR IS RESPONSIBLE FOR PROVIDED A FULL OPERATIONAL SYSTEM COMPLETE WITH THE FOLLOWING ITEMS PROVIDED BY DENT INSTRUMENTS OR APPROVED EQUAL: POWERSCOUT 48 NETWORK SUB METER (TECHNICAL ROOM), ROICIL FLEXIBLE CTs, HIGH PERFORMANCE MIDI HINGED CTs, AND MEDIUM SPLIT CORE CTs. CONTRACTOR IS RESPONSIBLE FOR PROVIDING ALL QUANTITIES, WIRING, CONNECTORS, CABLES, ACCESSORIES AND MAKING ALL CONNECTIONS FOR A COMPLETE AND OPERABLE SYSTEM PER MANUFACTURER'S INSTRUCTIONS.
CONTACT: REINO MATTILA, DENT INSTRUMENTS 541-668-4181; rmattila@dentinstruments.com

PROVIDE A PERMANENT READILY ACCESSIBLE AND VISIBLE DISPLAY ADJACENT TO THE MAIN BUILDING ENTRANCE OR ON A PUBLICLY AVAILABLE INTERNET WEBSITE. THE DISPLAY SHALL PROVIDE THE FOLLOWING:

- CURRENT DEMAND FOR WHOLE BUILDING ENERGY LEVEL MEASUREMENTS
- THE AVERAGE PEAK DEMANDS FOR THE PREVIOUS DAY AND THE SAME DAY PREVIOUS YEAR
- THE TOTAL ENERGY USAGE FOR THE PREVIOUS 18 MONTHS

CONTRACTOR IS RESPONSIBLE FOR PROVIDED A FULL OPERATIONAL SYSTEM COMPLETE WITH THE FOLLOWING ITEMS PROVIDED BY DENT INSTRUMENTS OR APPROVED EQUAL: POWERSCOUT 48 NETWORK SUB METER (TECHNICAL ROOM), ROICIL FLEXIBLE CTs, HIGH PERFORMANCE MIDI HINGED CTs, AND MEDIUM SPLIT CORE CTs. CONTRACTOR IS RESPONSIBLE FOR PROVIDING ALL QUANTITIES, WIRING, CONNECTORS, CABLES, ACCESSORIES AND MAKING ALL CONNECTIONS FOR A COMPLETE AND OPERABLE SYSTEM PER MANUFACTURER'S INSTRUCTIONS.
CONTACT: IAN MAAREFI, OBIUS 503-505-3849; ian.maarefi@obivius.com

- NOT USED.
- NOT USED.
- NOT USED.
- MAIN BONDING JUMPER SHALL BE SIZED #4/0 AL. CONTRACTOR TO INSTALL MAIN BONDING JUMPER AS PER NEC 250.28 AND CONNECTED TO THE MAIN GROUNDING BUS BAR.
- MANUFACTURER TO PROVIDE #1/0 AWG COPPER SUPPLY-SIDE BONDING JUMPER FOR TRANSFORMERS AS PER NEC 250.66

FEEDER SCHEDULE

A.C.S.X	A=Aluminum CU=Copper C=Conduit only (RIGID METAL CONDUIT) S=Service secondary X=Separately derived system
600SA	2 SETS OF (4 - #500 kcmil AL IN 2 1/2" C.)
603	3 #4 CU, 1 #10 CU GND., IN 1" C.
604	4 #4 CU, 1 #10 CU GND., IN 1 1/4" C.
604T	4 #4 CU, 1 #4 CU GND., IN 1 1/4" C.
703	3 #4 CU, 1 #8 CU GND., IN 1" C.
800SA	3 SETS OF (4 - #400 kcmil AL IN 2 1/2" C.)
1004A	4 #1/0 AL, 1 #8 CU GND., IN 1 1/2" C.
1254A	4 #2/0 AL, 1 #6 CU GND., IN 2" C.
1504A	4 #3/0 AL, 1 #6 CU GND., IN 2" C.
2004A	4 - #250 kcmil AL, 1 #6 CU GND., IN 2 1/2" C.
2254A	4 - #300 kcmil AL, 1 #4 CU GND., IN 2 1/2" C.
2504A	4 - #350 kcmil AL, 1 #4 CU GND., IN 2 1/2" C.
3503A	2 SETS OF (3 #4/0 AL, 1 #2 CU GND., IN 2" C.)
6004A	2 SETS OF (4 - #500 kcmil AL, 1 #1 CU GND., IN 3" C.)
8004A	3 SETS OF (4 - #400 kcmil AL, 1 #1/0 CU GND., IN 3" C.)

MINIMUM SIZE EQUIPMENT GROUNDING CONDUCTORS FOR GROUNDING RACEWAY & EQUIPMENT		
RATING OR SETTING OF AUTOMATIC OVER CURRENT DEVICE IN CIRCUIT AHEAD OF EQUIPMENT, CONDUIT ETC. NOT EXCEEDING (AMPERES)	SIZE (AWG/kcmil)	
	COPPER	ALUMINUM OR COPPER-CLAD ALUMINUM
15	14	12
20	12	10
30	10	8
40	10	8
60	10	8
100	8	6
200	6	4
300	4	2
400	3	1
500	2	1/0
600	1	2/0
800	1/0	3/0
1000	2/0	4/0
1200	3/0	250
1600	4/0	350
2000	250	400
2500	350	600
3000	400	600
4000	500	750
5000	700	1200
6000	800	1200

EQUIPMENT GROUNDING CONDUCTORS MAY NEED TO BE SIZED LARGER THAN SPECIFIED IN THIS SCHEDULE IN ORDER TO COMPLY WITH N.E.C. SECTION 250.4(A)(5) or (B)(4)

GROUNDING ELECTRODE CONDUCTOR FOR AC SYSTEMS			
SIZE OF LARGEST SERVICE ENTRANCE CONDUCTOR OR EQUIVALENT AREA FOR PARALLEL CONDUCTORS (AWG/kcmil)		SIZE OF GROUNDING ELECTRODE CONDUCTOR	
COPPER		ALUMINUM OR COPPER-CLAD ALUMINUM	COPPER
2 OR SMALLER		1/0 OR SMALLER	8
1 OR 1/0		2/0 OR 3/0	6
2/0 OR 3/0		4/0 OR 250 kcmil	4
4/0 THRU 350 kcmil		300 kcmil THROUGH 500 kcmil	2
400 kcmil THROUGH 600 kcmil		600 kcmil THROUGH 900 kcmil	1/0
750 kcmil THROUGH 1100 kcmil		1000 kcmil THROUGH 1750 kcmil	2/0
OVER 1100 kcmil		OVER 1750 kcmil	3/0

WHERE MULTIPLE SETS OF SERVICE-ENTRANCE CONDUCTORS ARE USED AS PERMITTED IN N.E.C. ARTICLE 230.40, EXCEPTION NO. 2, THE EQUIVALENT SIZE OF THE LARGEST SERVICE-ENTRANCE CONDUCTOR SHALL BE DETERMINED BY THE SUM OF THE AREAS OF THE CORRESPONDING CONDUCTORS OF EACH SET, WHERE THERE ARE NO SERVICE-ENTRANCE CONDUCTORS, THE GROUNDING ELECTRODE CONDUCTOR SIZE SHALL BE DETERMINED BY THE EQUIVALENT SIZE OF THE LARGEST SERVICE ENTRANCE CONDUCTOR REQUIRED FOR THE LOAD TO BE SERVED. SIZE THE MAIN BONDING JUMPER PER NEC 250.102 (C)(1)

TRANSFORMER GROUNDING CONDUCTORS	
TRANSFORMER KVA RATING	COPPER GROUND CONDUCTOR SIZE (AWG/kcmil)
3	8
6	8
9	8
15	8
25	8
30	6
45	6
75	2
112.5	2
150	1/0
225	2/0
300	3/0
500	3/0
750	3/0
1000	3/0

ISSUANCE
1 12/18/2025 PERMIT CYCLE 2
3 05/28/2026 CCD 01

PROJECT NUMBER
79650191
PROJECT MANAGER
A. HENGSTEBECK
PROFESSIONAL
D. HERSCHER
DRAWN BY
M. GONZALEZ
CHECKED BY
D. HERSCHER

ELECTRICAL
RISER DIAGRAMS
E400

PROGRESSIVE
COMPANIES
PROGRESSIVE ARCHITECTURE ENGINEERING & PLANNING, LLC
Charlotte, NC | Detroit, MI | Grand Rapids, MI
weareprogressive.com




LIDL US, LLC
LIDL 1517 NORCROSS, GA

499 JIMMY CARTER BLVD NORCROSS, GA 30093

1 METERING DETAIL

NTS

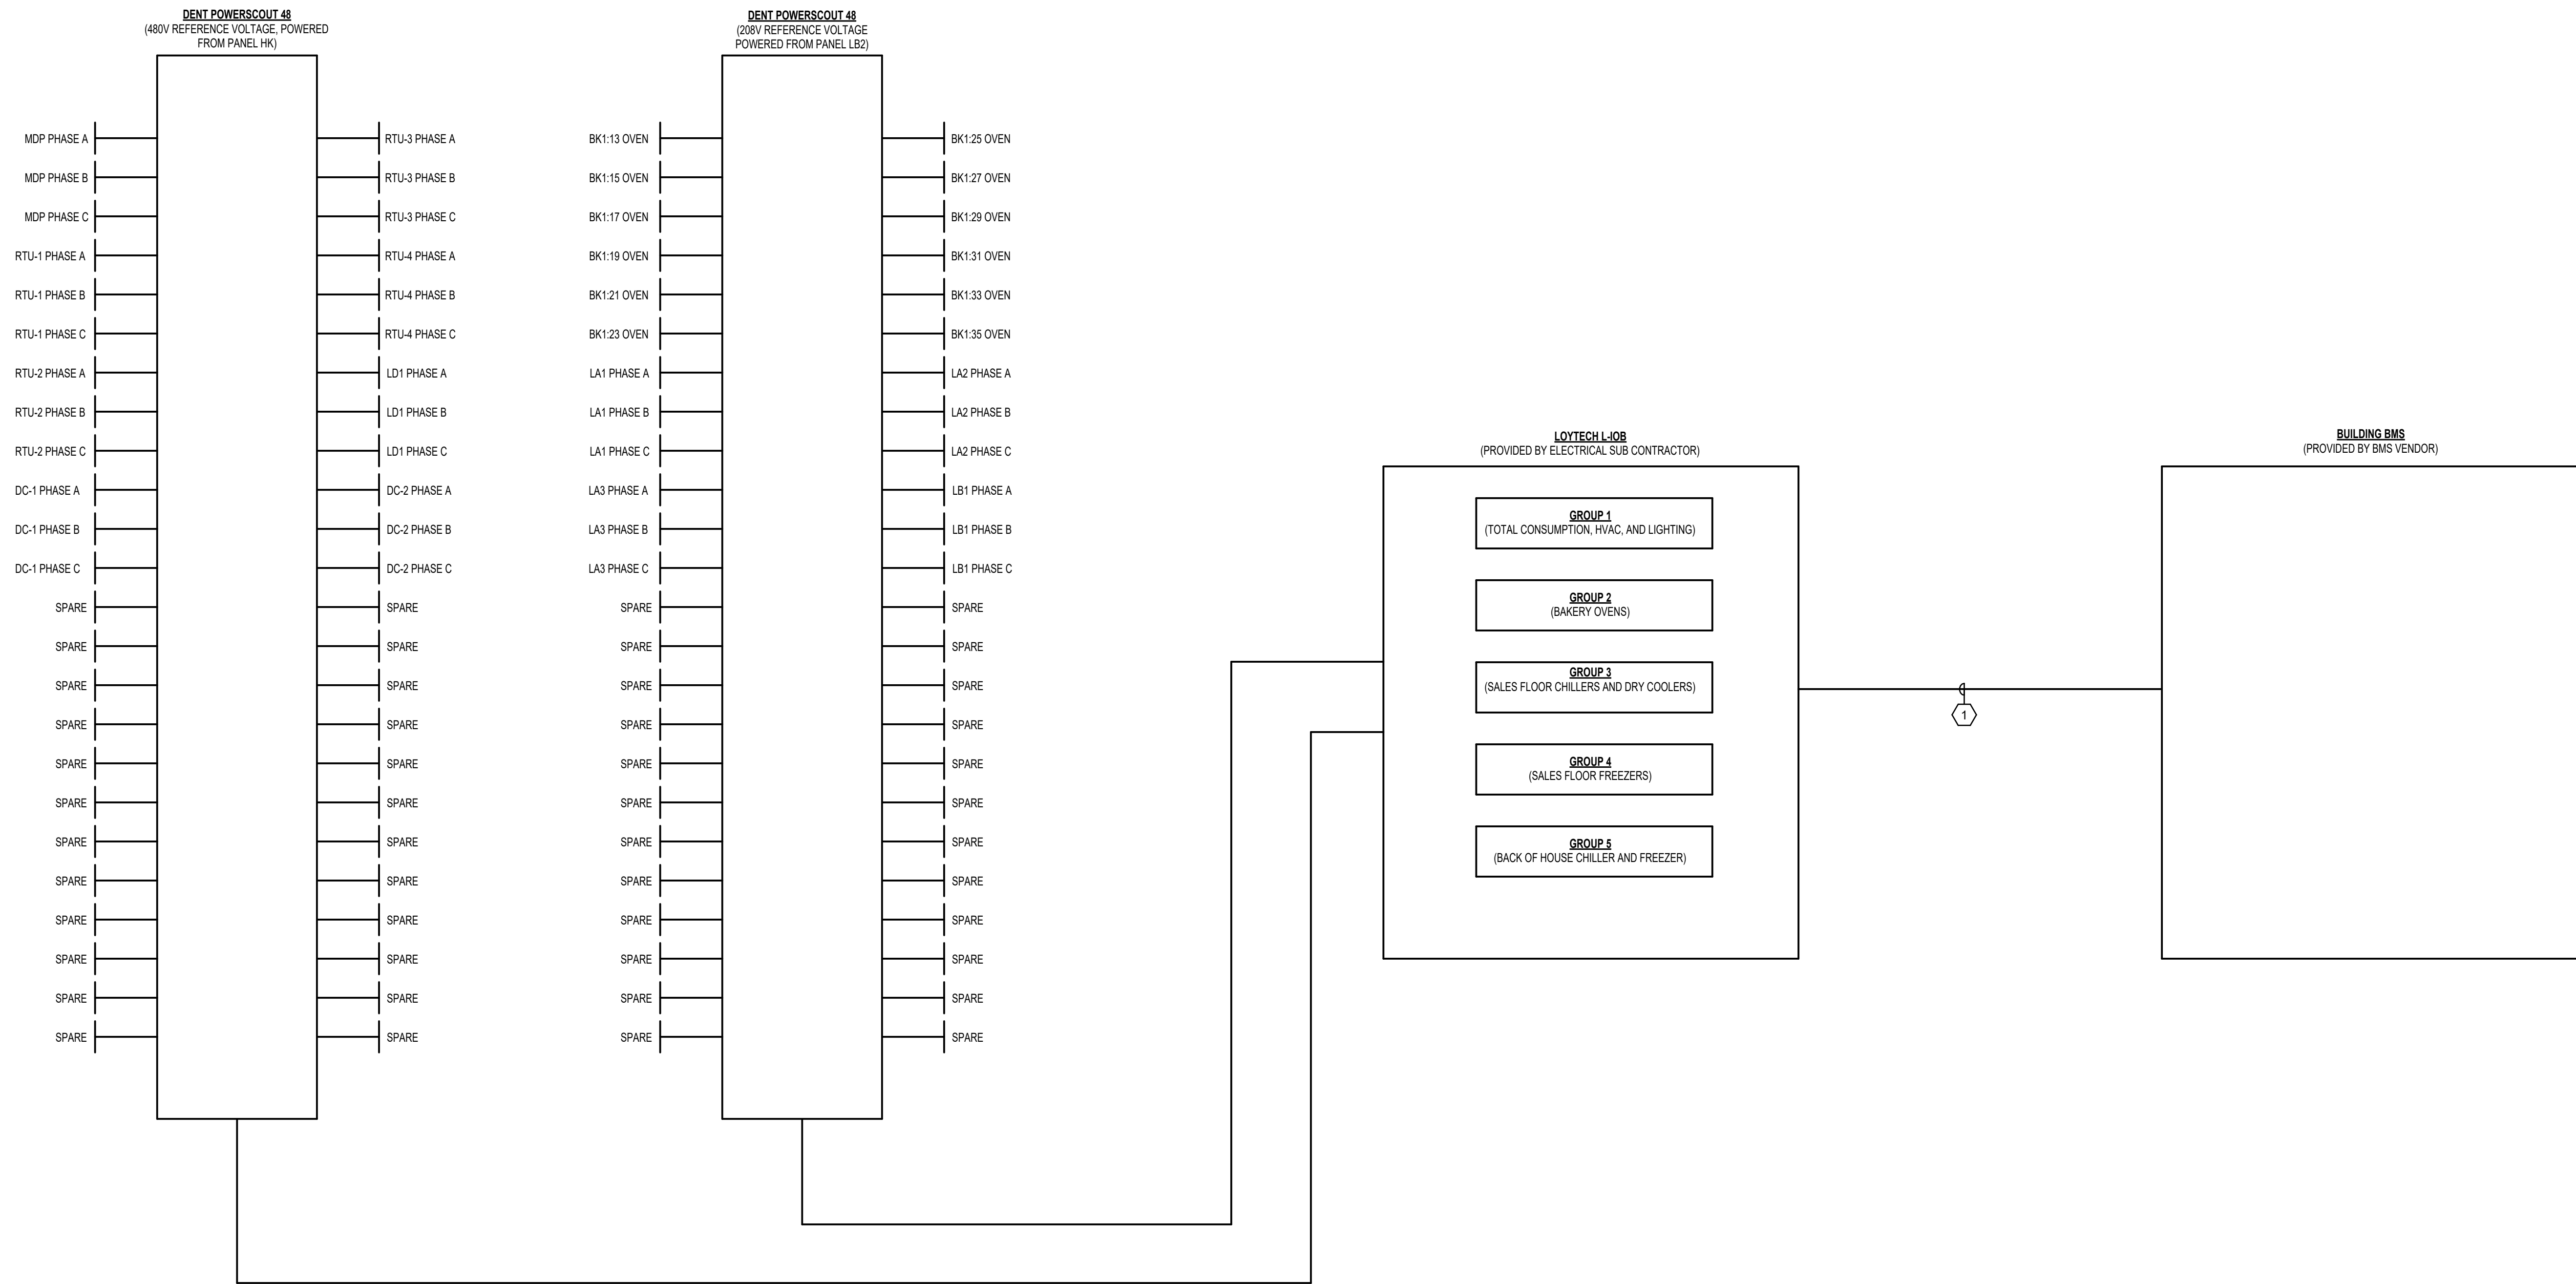

GENERAL SHEET NOTES

- A. REFER TO PANEL SCHEDULES FOR EXACT CIRCUIT NUMBERS.

SHEET KEYNOTES

1. FINAL INTEGRATION TO BMS PANEL BY COPELAND.

ISSUANCE
1 12/18/2025 PERMIT CYCLE 2

PROJECT NUMBER
79650191
PROJECT MANAGER
A. HENGSTEBECK
PROFESSIONAL
D. HERSCHER
DRAWN BY
M. GONZALEZ
CHECKED BY
D. HERSCHER

ELECTRICAL -
METERING
DETAIL
E401

LIDL US, LLC
LIDL 1517 NORCROSS, GA

499 JIMMY CARTER BLVD NORCROSS, GA 30093




PROGRESSIVE
ARCHITECTURE ENGINEERING & PLANNING, LLC
COMPANIES
Charlotte, NC | Detroit, MI | Grand Rapids, MI
weareprogressive.com




MECHANICAL EQUIPMENT CONNECTION SCHEDULE											
SYMBOL	DESCRIPTION	LOCATION	VOLTS	PH	LOAD(VA)	HP	MCA	MOCp	CIRCUIT NUMBER	WIRE / CONDUIT	NOTES
AC-1	AIR CONDITIONING UNIT	IT ROOM 110	208	3	6373.9 41.6		2	15	HK-33,35,37 LB3-37,39	202	SINGLE POINT POWER CONNECTION. INDOOR UNIT POWERED FROM OUTDOOR UNIT CU-1.
CU-1	CONDENSING UNIT	ROOF	208	1	3120.0		15	15	LB3-32,34,36	202	
CVF-1	INLINE BOOSTER	SALES	120	1	152.4		1.27	20	LB3-33	202	
CVF-2	INLINE BOOSTER	SALES	120	1	152.4		1.27	20	LB3-33	202	
CVF-3	INLINE BOOSTER	SALES	120	1	152.4		1.27	20	LB3-35	202	
DC-1	DRY COOLER DC-1	ROOF	480	3	22627.5		27.22	35	HK-27,29,31	403	
DC-2	DRY COOLER DC-2	ROOF	480	3	28284.4		34	45	HK-7,9,11	503	
DSP	DESTRATIFICATION FAN	SALES	120	1	45.0		0.32	20	LC1-25	202	
EUH-1	ELECTRIC UNIT HEATER	VESTIBULE	480	1	8160.0		17	25	HK-8,10	302	
EW-H-1	ELECTRIC WATER HEATER	STAGING 113	480	1	12000.0		15	20	HK-39,41	202	
KEF-1	KITCHEN EXHUAIST FAN	SALES	120	1	756.0		6.3	20	BK1-5	202	
RTU-1	ROOF TOP UNIT	ROOF	480	3	46211.1		58	60	MDP-1-13,15,17	603	
RTU-2	ROOF TOP UNIT	ROOF	480	3	46211.1		58	60	HK-1,3,5	603	
RTU-3	ROOF TOP UNIT	ROOF	480	3	25495.8		32	35	HK-13,15,17	403	1
RTU-4	ROOF TOP UNIT	ROOF	480	3	9560.9		12	15	HK-19,21,23	203	1
TEF-1	EXHAUST FAN	SALES	120	1	54.0		.16	20	LC1-19	202	
TEF-2	EXHAUST FAN	SALES	120	1	54.0		.16	20	LC1-17	202	

WIRE/CONDUIT SCHEDULE	
200S	4 #3/0 CU IN 2" C.
202	2 #12 CU, 1 #12 CU GND., IN 3/4" C.
203	3 #12 CU, 1 #12 CU GND., IN 3/4" C.
302	2 #10 CU, 1 #10 CU GND., IN 3/4" C.
403	3 #8 CU, 1 #10 CU GND., IN 3/4" C.
	3 #6 CU, 1 #10 CU GND., IN 3/4" C.
603	3 #4 CU, 1 #10 CU GND., IN 1" C.

GENERAL MECHANICAL EQUIPMENT CONNECTION NOTE:	
A.	THE ABOVE INFORMATION IS FOR A SPECIFIC MANUFACTURER. ACTUAL MANUFACTURER FOR EQUIPMENT MAY BE DIFFERENT. COORDINATE WITH MECHANICAL EQUIPMENT SUBMITTALS FOR LOADS AND OVER CURRENT PROTECTION REQUIREMENTS PRIOR TO INSTALLATION OF WIRING.
B.	MOCp = MAXIMUM OVER CURRENT PROTECTION. MCA = MINIMUM CIRCUIT AMPACITY
C.	PROVIDE DISCONNECTING MEANS FOR EACH ITEM OF EQUIPMENT LISTED IN THE SCHEDULE ABOVE, EXCEPT AS SPECIFICALLY NOTED OTHERWISE IN SCHEDULE NOTES, BELOW.
MECHANICAL EQUIPMENT CONNECTION SCHEDULE NOTES	
1	RTU PROVIDED WITH LOCAL SERVICE DISCONNECT. BY MECHANICAL CONTRACTOR.

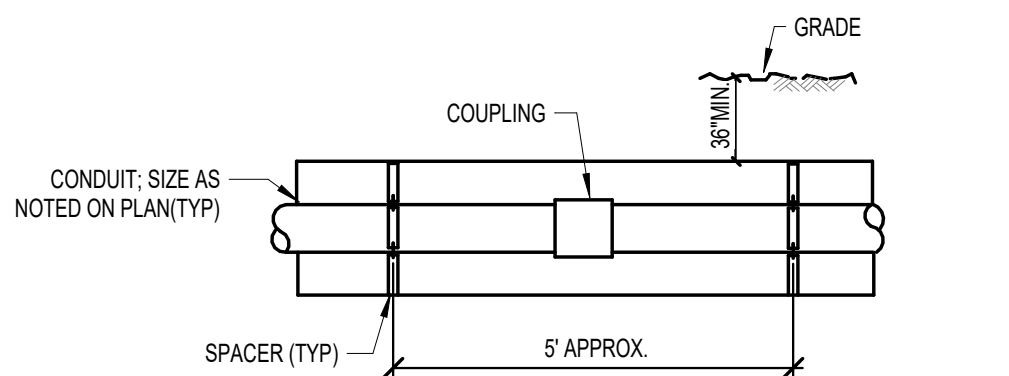


SECTION

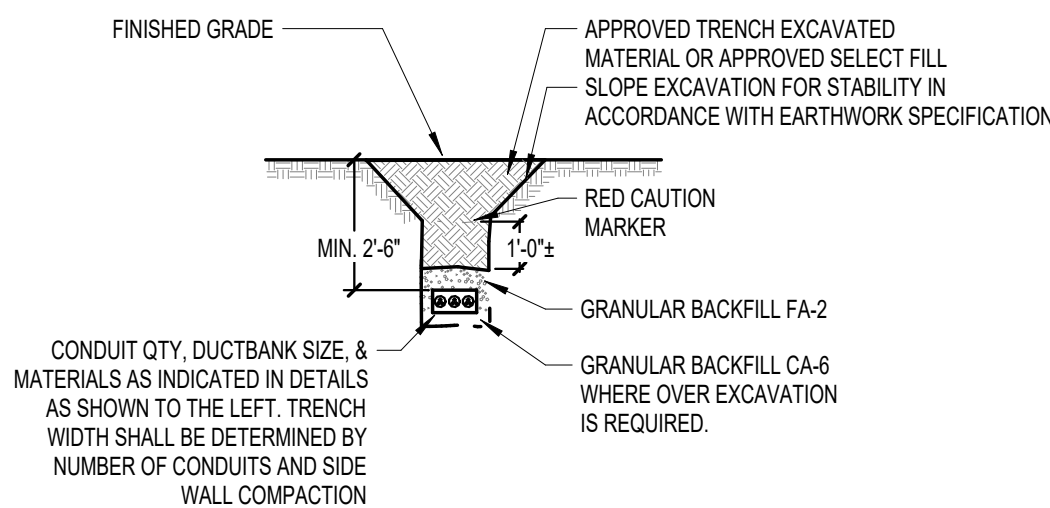

CROSS SECTION

7 NON-CONCRETE UNDERGROUND CONDUITS


NTS

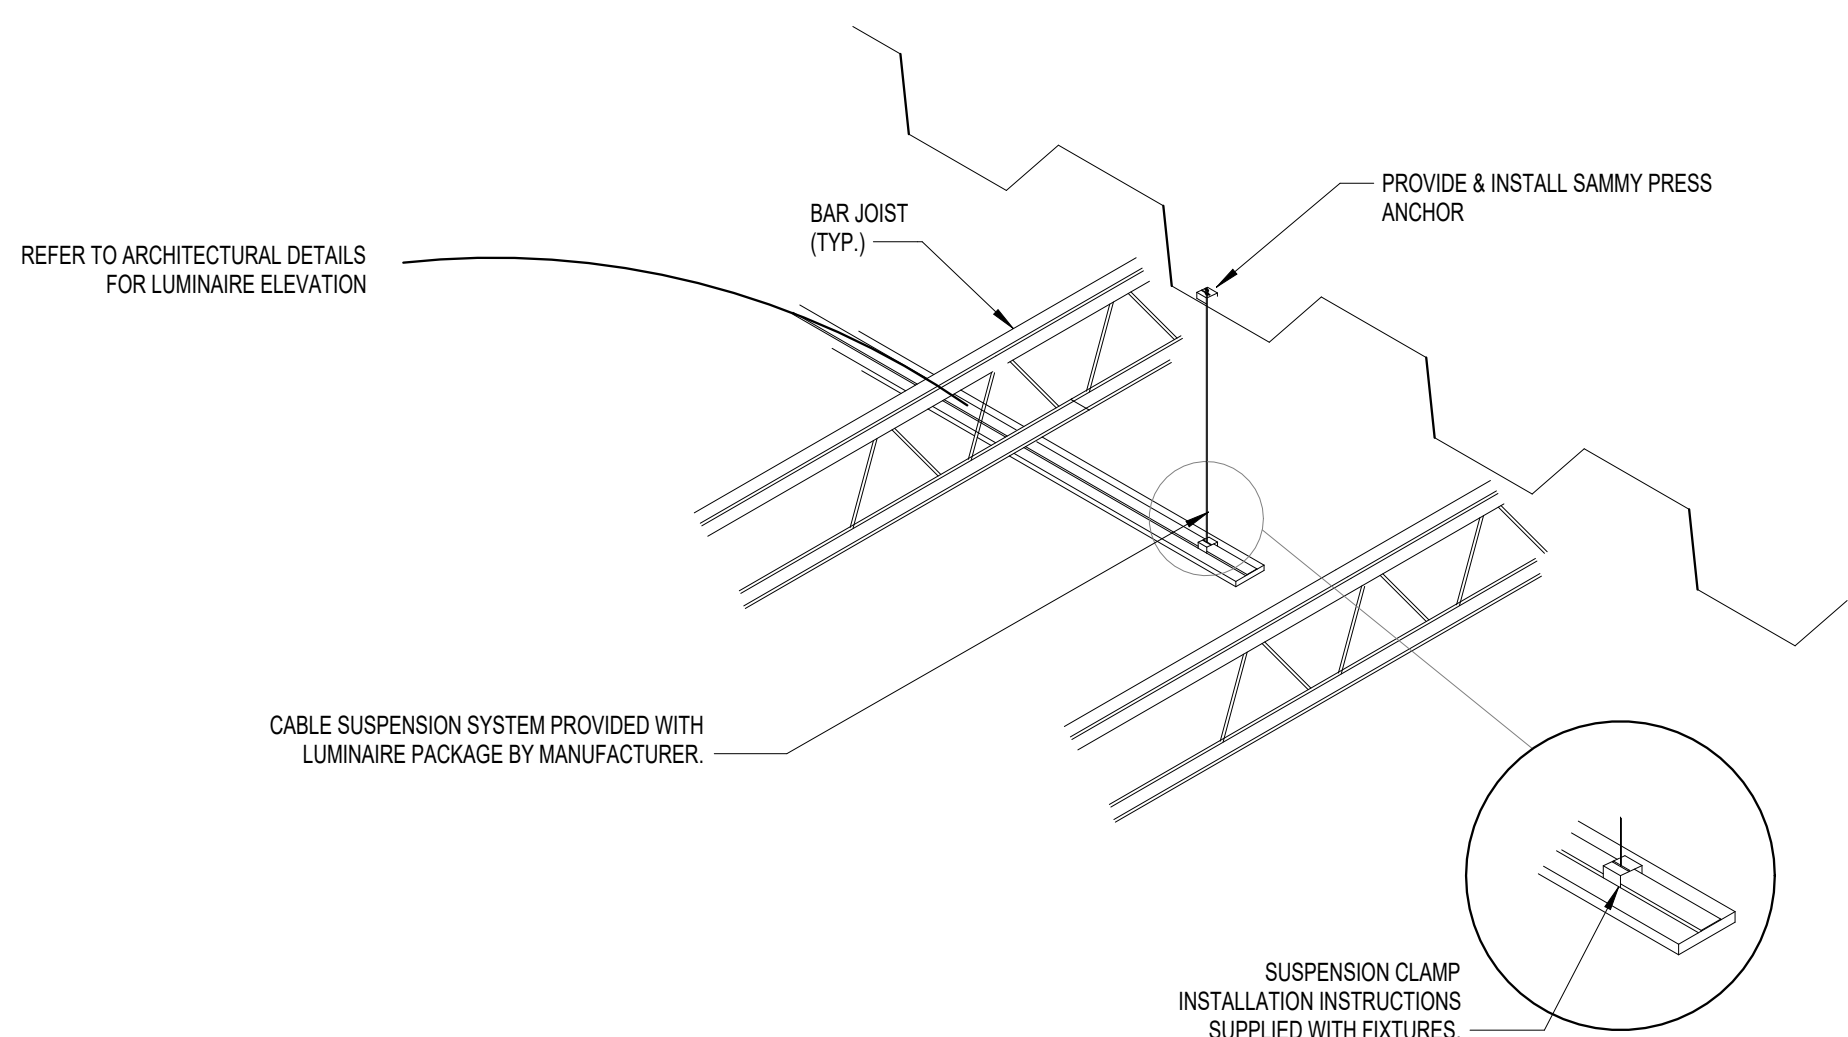

NOTE: LIGHT FIXTURES IN THE SALES FLOOR AREA SHALL NOT BE ATTACHED TO THE JOIST.

8 SALES FLOOR LIGHTING DETAIL


NTS

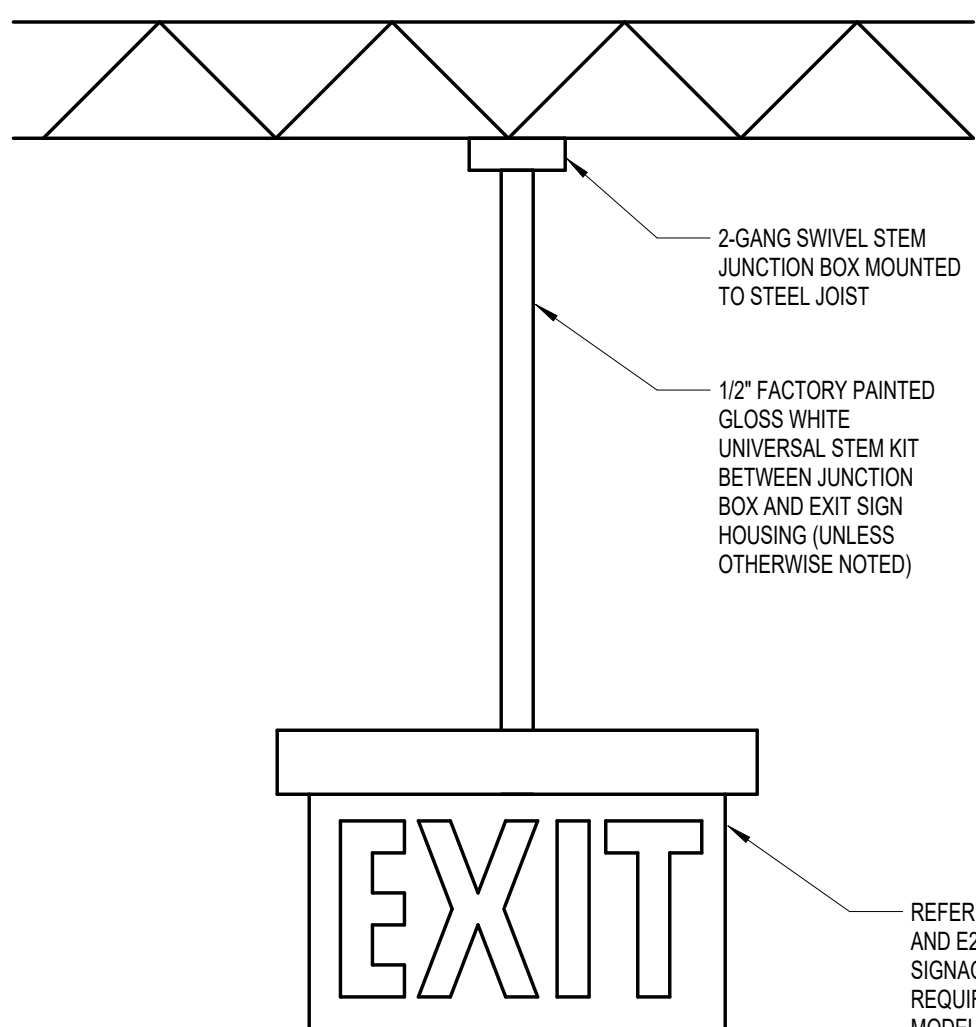

REFER TO SHEET E201 AND E202 FOR EXIT SIGNAGE POWER REQUIREMENTS AND MODEL


4 EXIT SIGN -PENDANT MOUNTING-INSTALLATION DETAIL

NTS

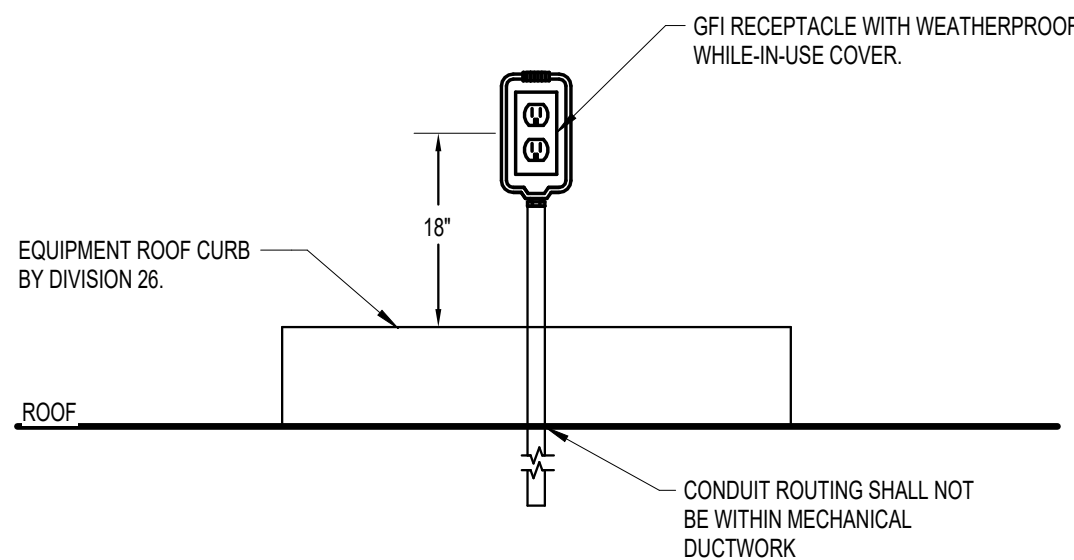


5 ROOFTOP RECEPTACLE MOUNTING DETAIL

NTS

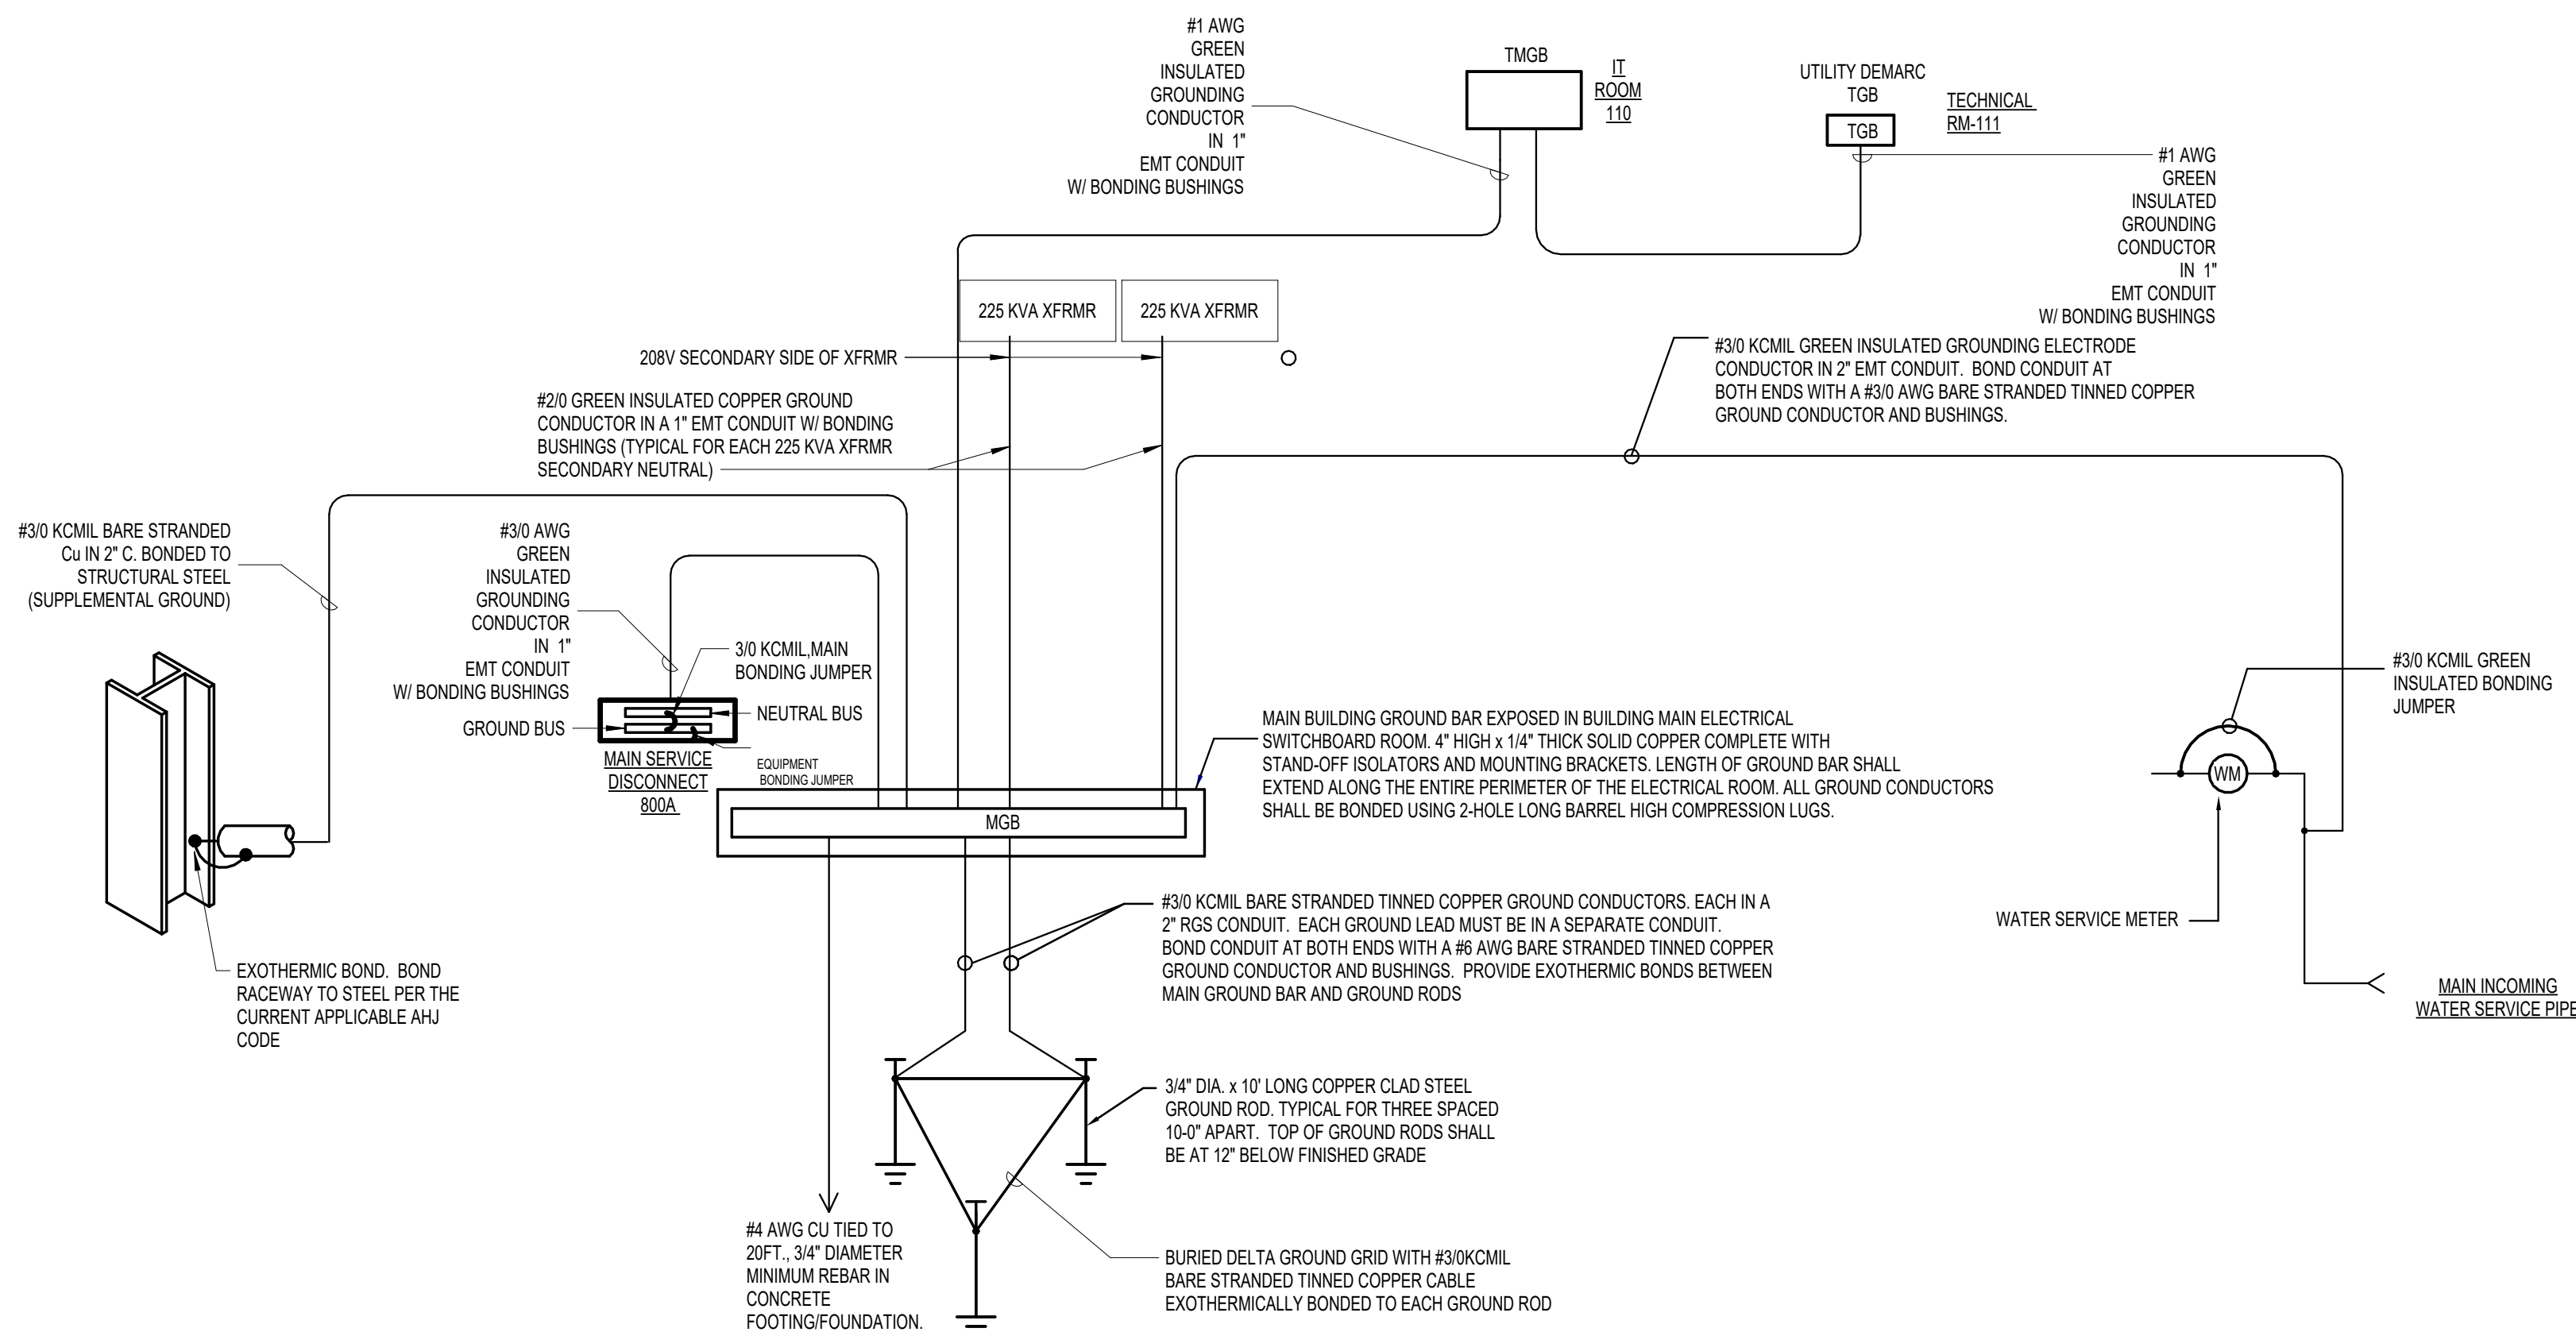


6 GROUNDING SYSTEM ONE-LINE RISER DIAGRAM

NTS

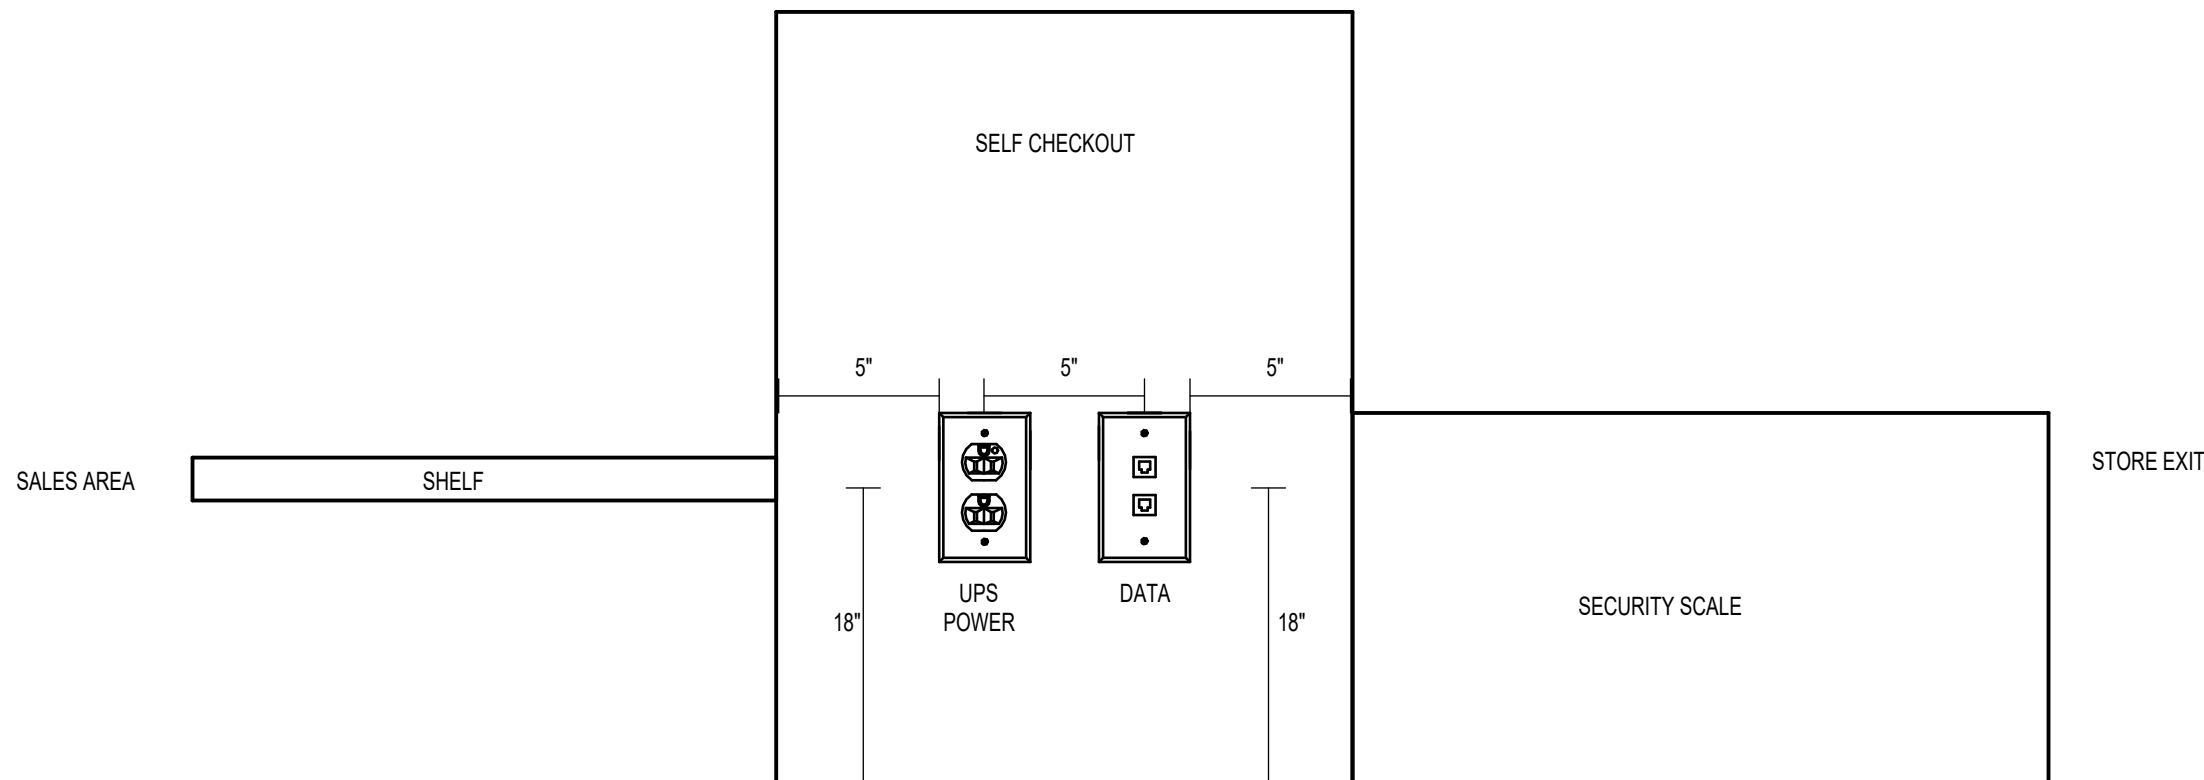


VERSION A - CUSTOMER TRAFFIC FROM LEFT TO RIGHT

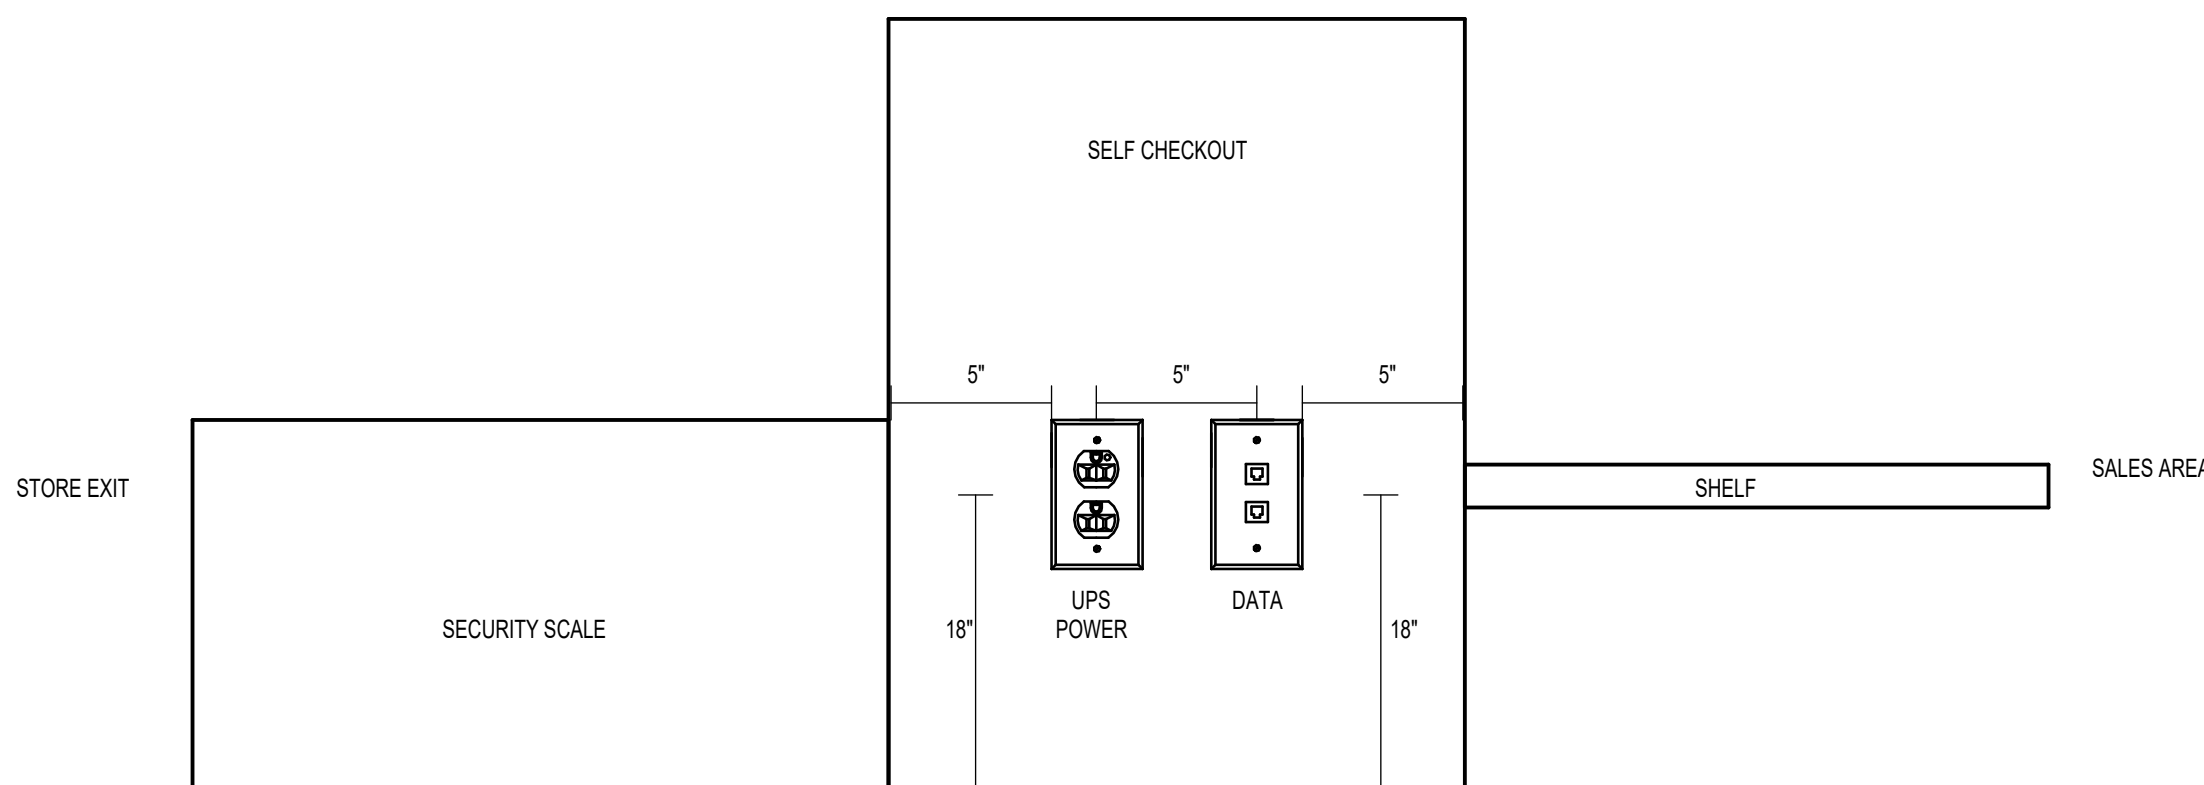

VERSION B - CUSTOMER TRAFFIC FROM RIGHT TO LEFT

1 SCO VERSION A,B FRONT VIEW DATA UPS

NTS

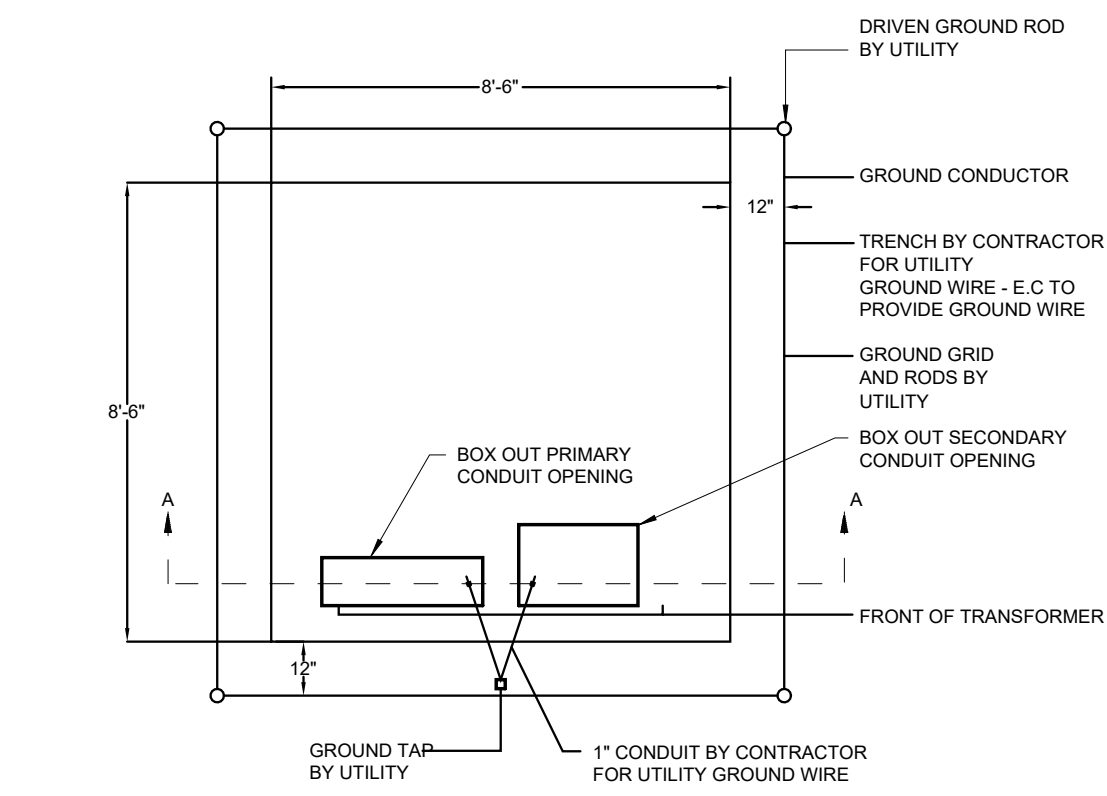


- E.C. TO CONSTRUCT TRANSFORMER PAD IN ACCORDANCE WITH UTILITY STANDARD AND INSTALL IN ACCORDANCE WITH UTILITY STANDARD
- E.C. SHALL PROVIDE THE GROUND WIRE. COMED TO MAKE FINAL CONNECTIONS. COORDINATE EXACT REQUIREMENTS WITH UTILITY. GROUNDING SHALL BE IN ACCORDANCE WITH UTILITY STANDARD
- PAD SHALL BE CAST IN PLACE. COORDINATE EXACT REQUIREMENTS WITH UTILITY.
- E.C. SHALL COORDINATE ALL GROUNDING SCOPE OF WORK WITH UTILITY.

DIMENSIONS TO BE VERIFIED WITH TRANSFORMER SHOP DRAWINGS.

2 UTILITY TRANSFORMER PAD DETAILS AND GROUNDING

NTS

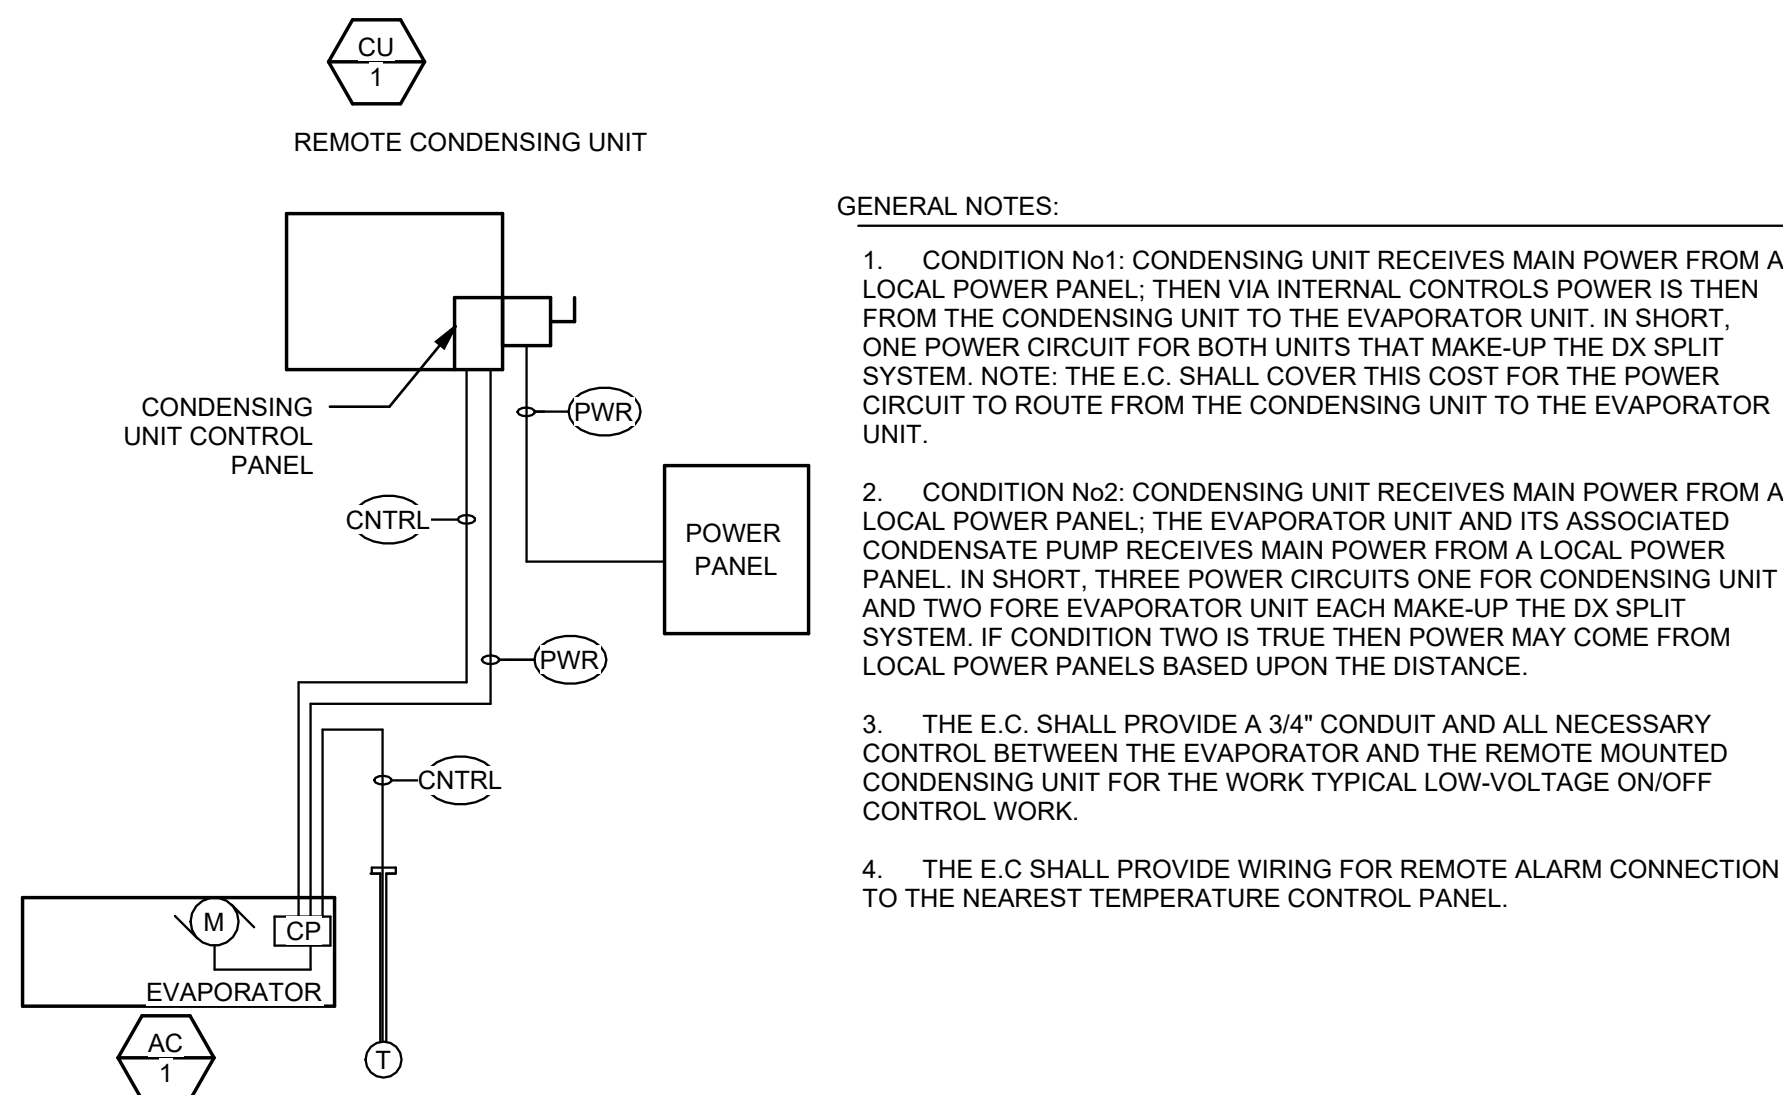


GENERAL NOTES:

- CONDITION N01: CONDENSING UNIT RECEIVES MAIN POWER FROM A LOCAL POWER PANEL. THEN VIA INTERNAL CONTROLS POWER IS THEN FROM THE CONDENSING UNIT TO THE EVAPORATOR UNIT. IN SHORT, ONE POWER CIRCUIT FOR BOTH UNITS THAT MAKE-UP THE DX SPLIT SYSTEM. NOTE: THE E.C. SHALL COVER THIS COST FOR THE POWER CIRCUIT TO ROUTE FROM THE CONDENSING UNIT TO THE EVAPORATOR UNIT.
- CONDITION N02: CONDENSING UNIT RECEIVES MAIN POWER FROM A LOCAL POWER PANEL. THE EVAPORATOR UNIT AND ITS ASSOCIATED CONDENSATE PUMP RECEIVES MAIN POWER FROM A LOCAL POWER PANEL. IN SHORT, THREE POWER CIRCUITS ONE FOR CONDENSING UNIT AND TWO FOR EVAPORATOR UNIT EACH MAKE-UP THE DX SPLIT SYSTEM. IF CONDITION TWO IS TRUE THEN POWER MAY COME FROM LOCAL POWER PANELS BASED UPON THE DISTANCE.
- THE E.C. SHALL PROVIDE A 3/4" CONDUIT AND ALL NECESSARY CONTROL BETWEEN THE EVAPORATOR AND THE REMOTE MOUNTED CONDENSING UNIT FOR THE WORK TYPICAL LOW-VOLTAGE ON/OFF CONTROL WORK.
- THE E.C. SHALL PROVIDE WIRING FOR REMOTE ALARM CONNECTION TO THE NEAREST TEMPERATURE CONTROL PANEL.

3 DX SPLIT SYSTEMS POWER AND CONTROLS DIAGRAM

NTS

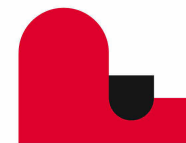





GROUND BAR SCHEDULE				
TAG	QTY.	LENGTH (INCHES)	THICKNESS (INCHES)	MOUNTING HEIGHT (IN)
MGB	1	30"	1/4"	12" A.F.F.
TMGB	1	30"	1/4"	8'-2" A.F.F.
TGB	1	24"	1/4"	18" A.F.F.

5 TYPICAL WIRING SCHEMATICS FOR LINEAR ROW OF FIXTURES WITHIN 15'-0" FROM WINDOW


ELECTRICAL DETAILS E601

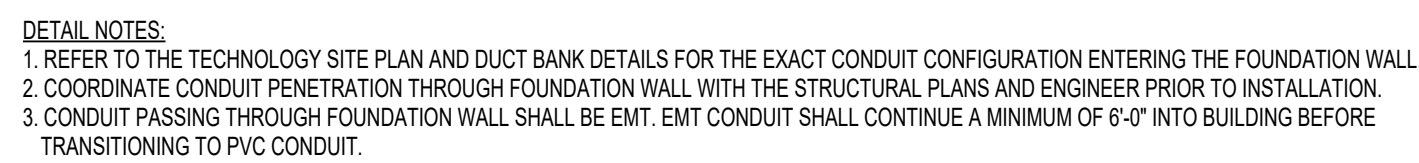

NTS

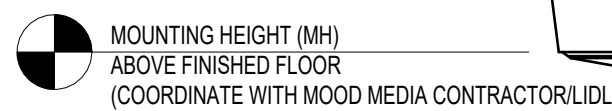


NTS

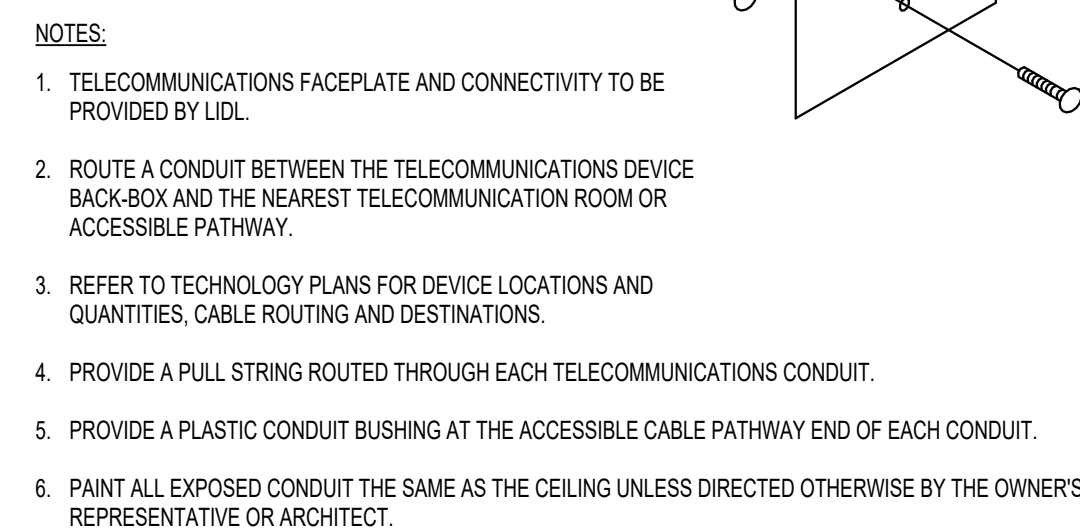

NTS




NTS

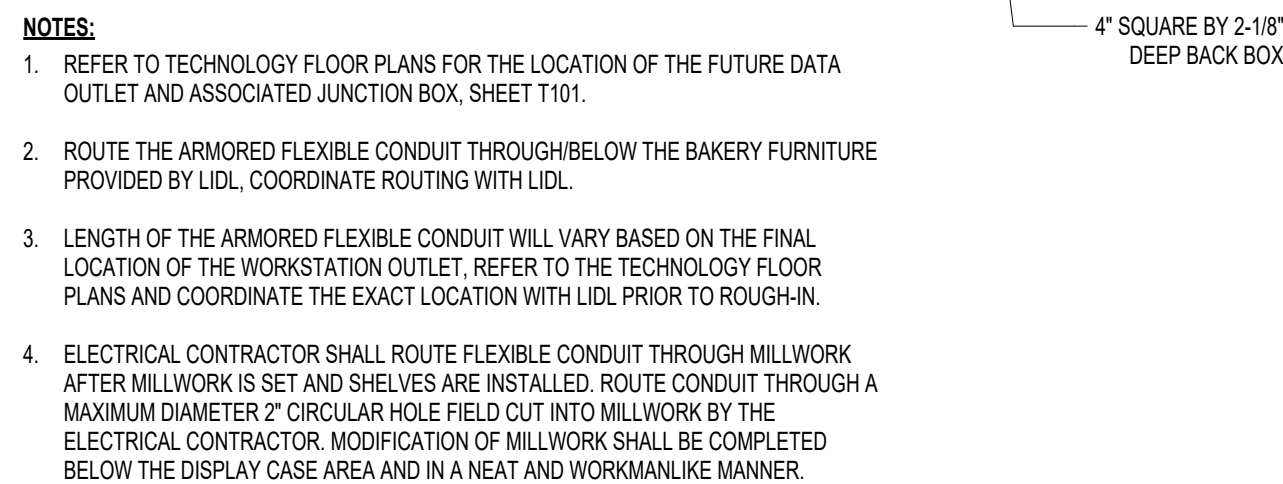

NTS




NTS

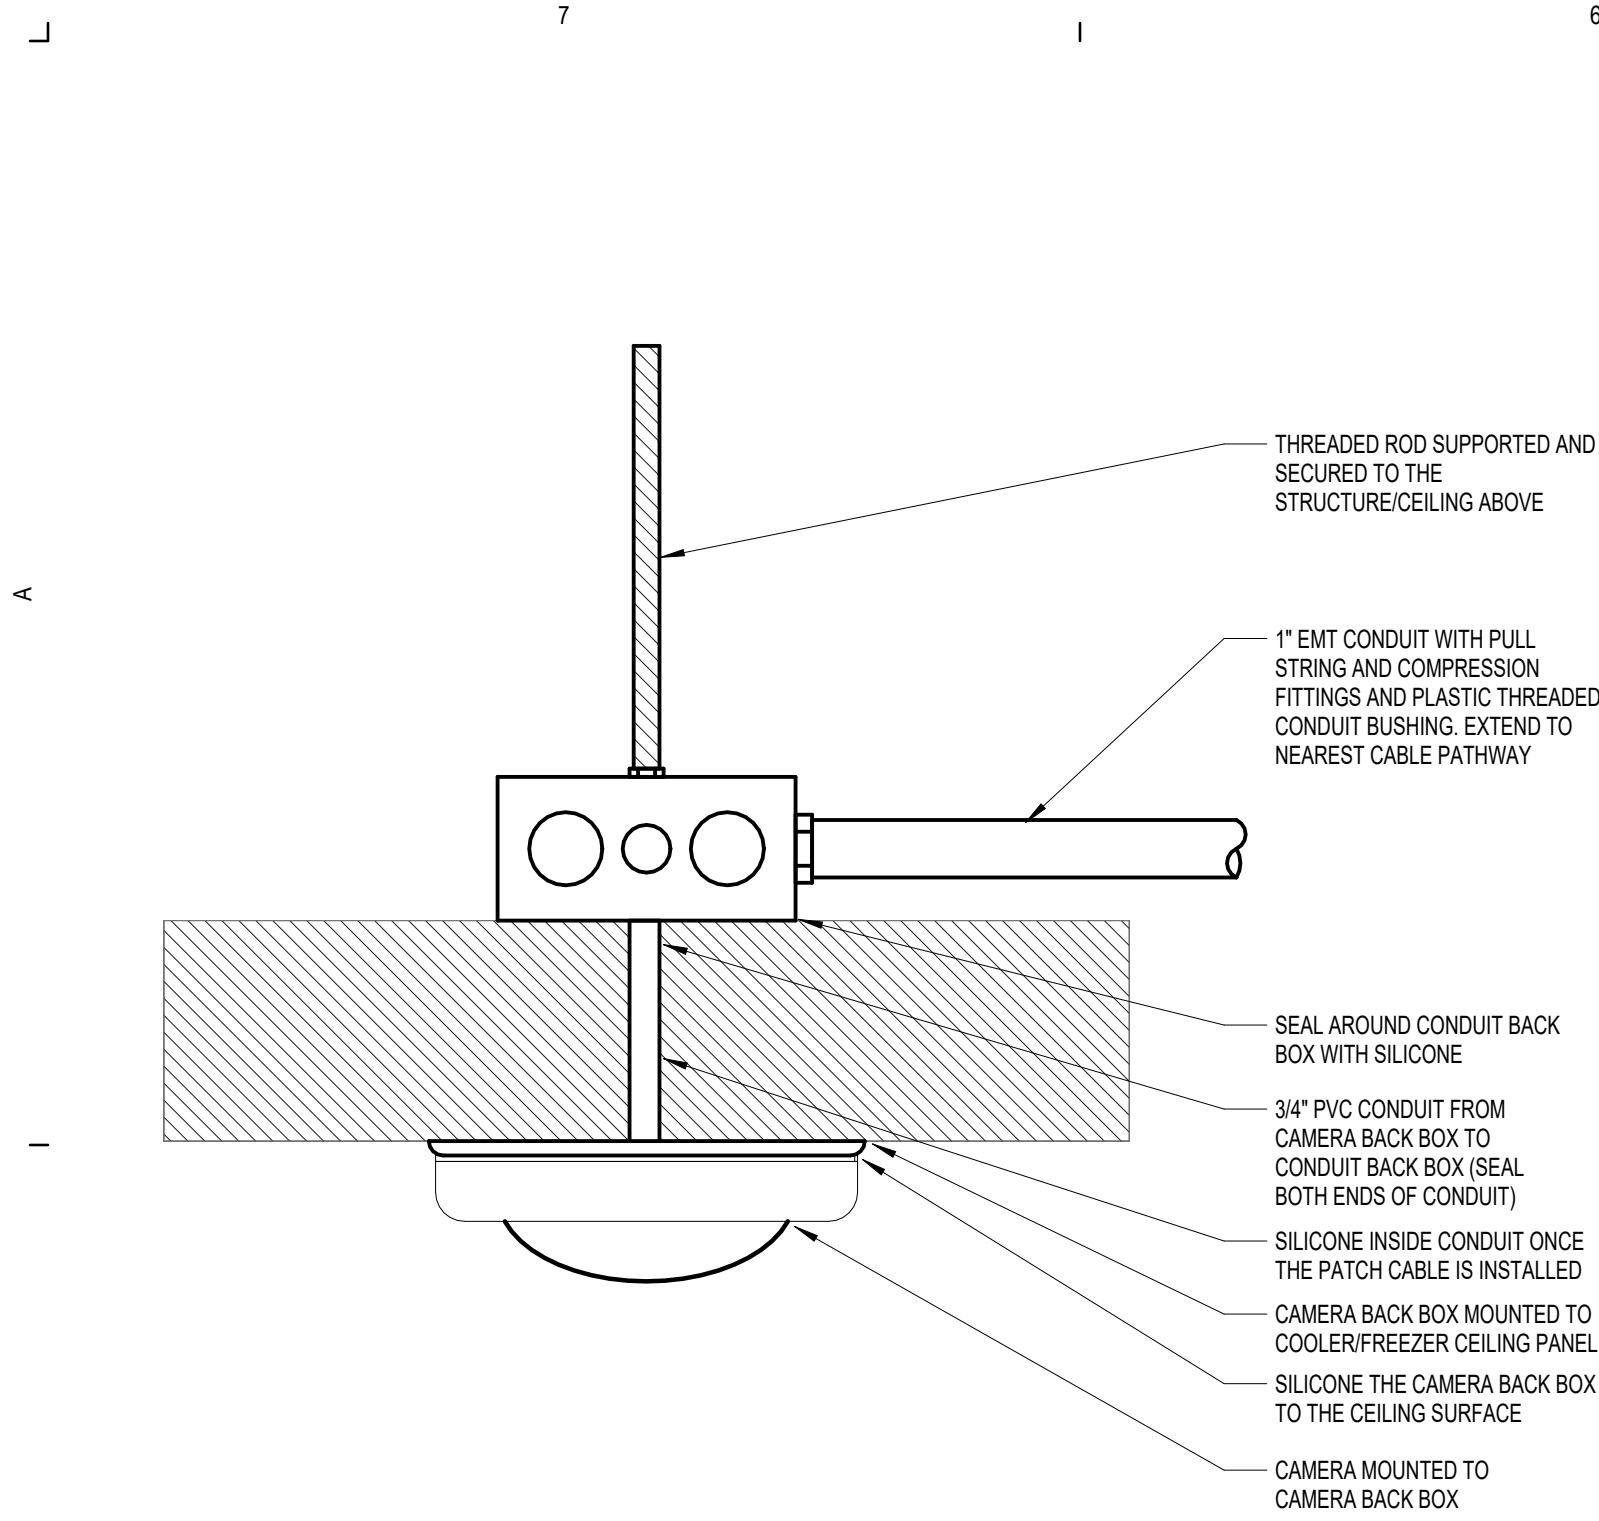


7 COOLER/FREEZER CEILING MOUNTED CAMERA DETAIL

NTS

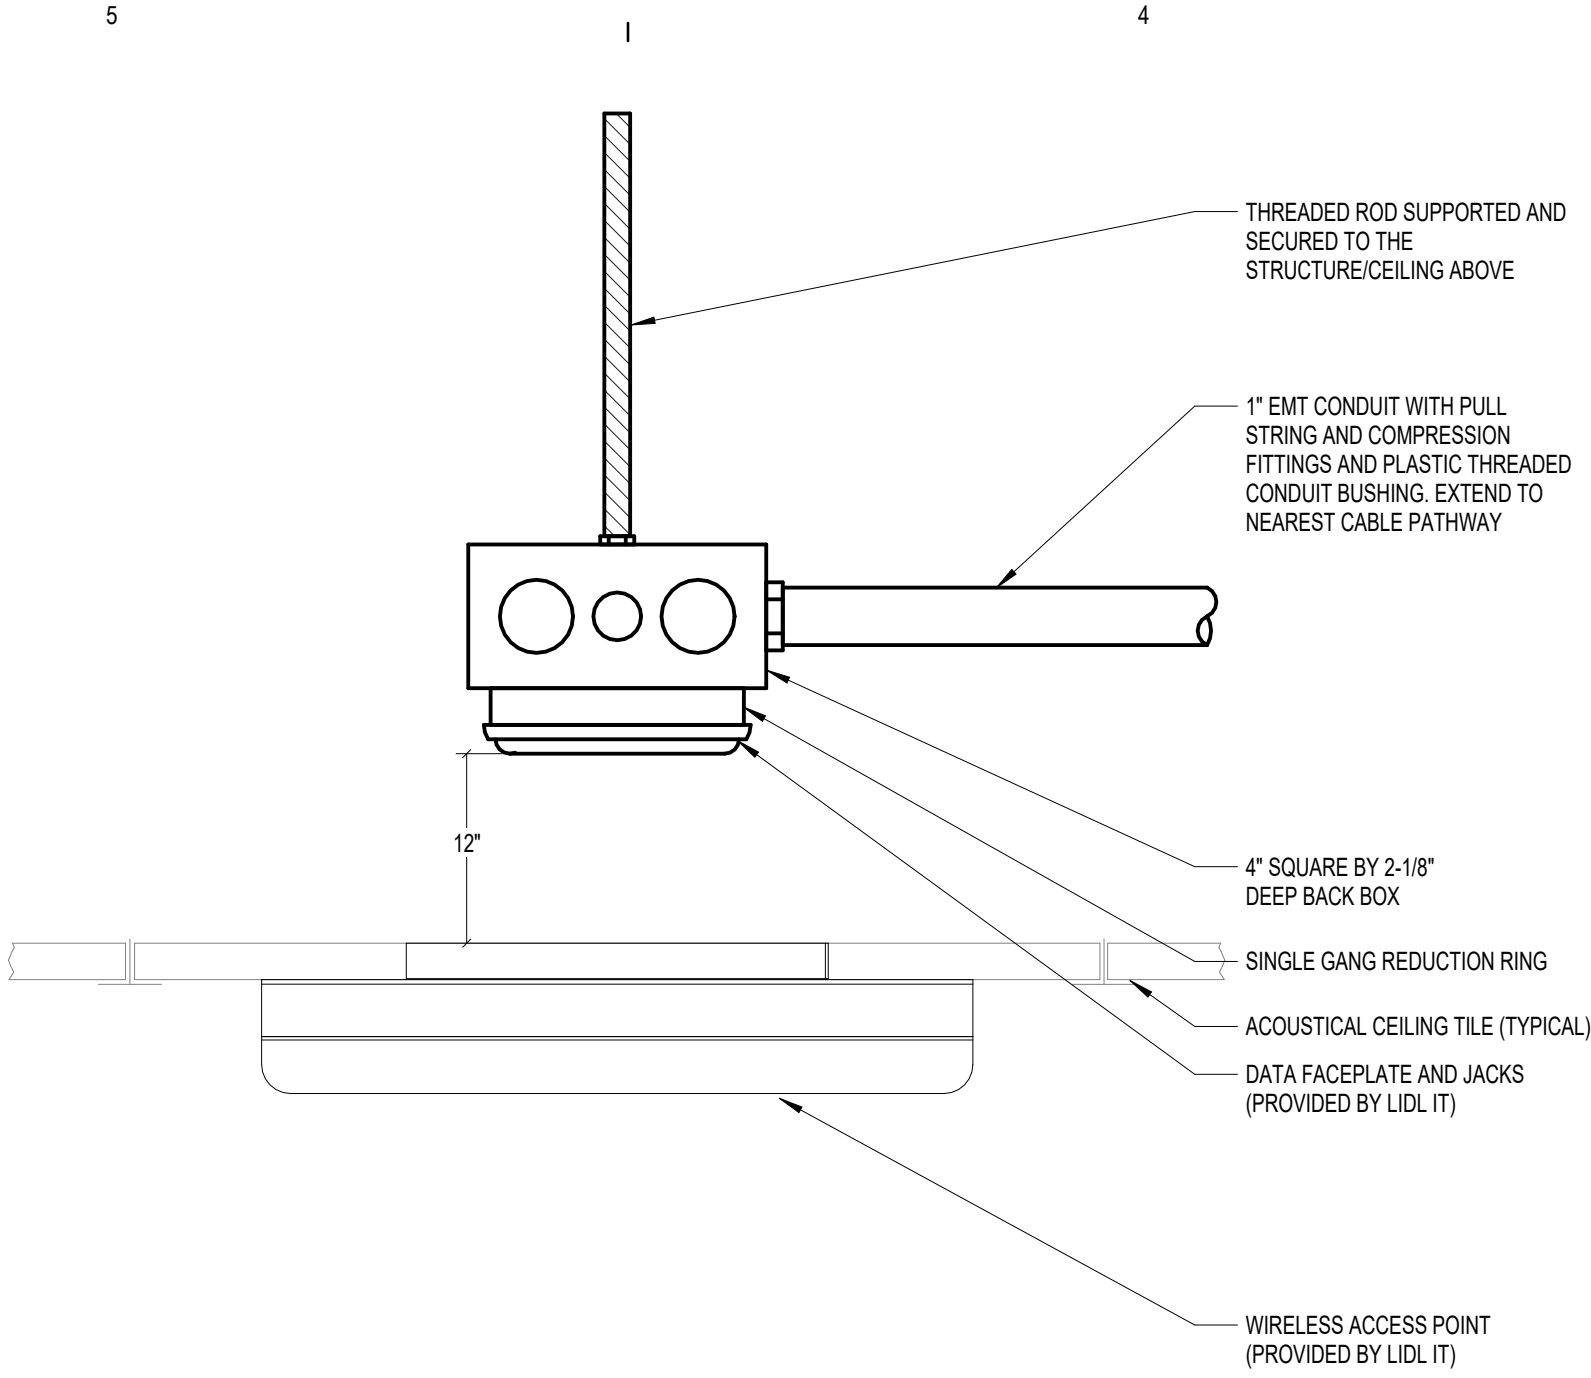


4 INTERIOR CEILING MOUNTED WIRELESS ACCESS POINT DETAIL

NTS

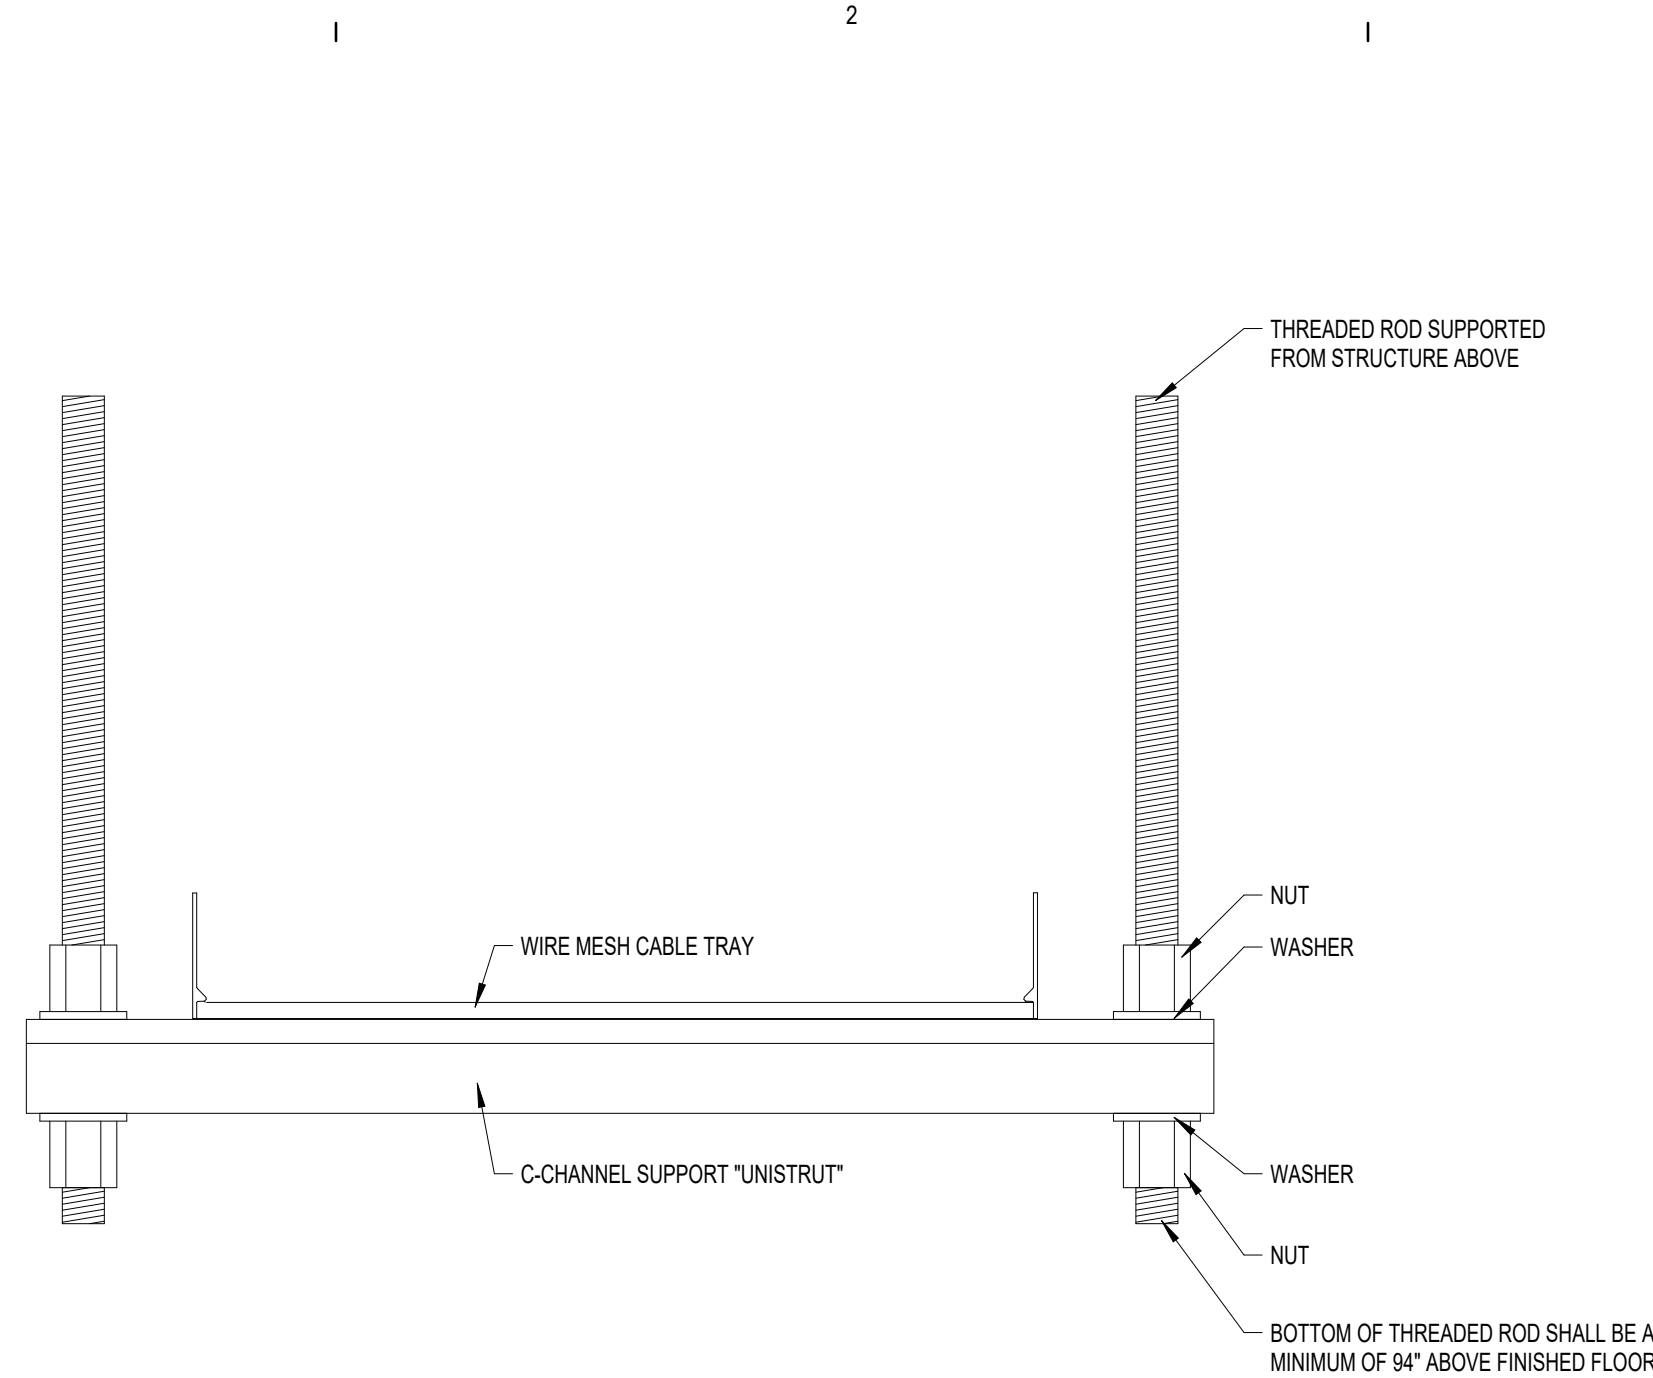


1 IT ROOM 110 CABLE WIREWAY SECTION

NTS

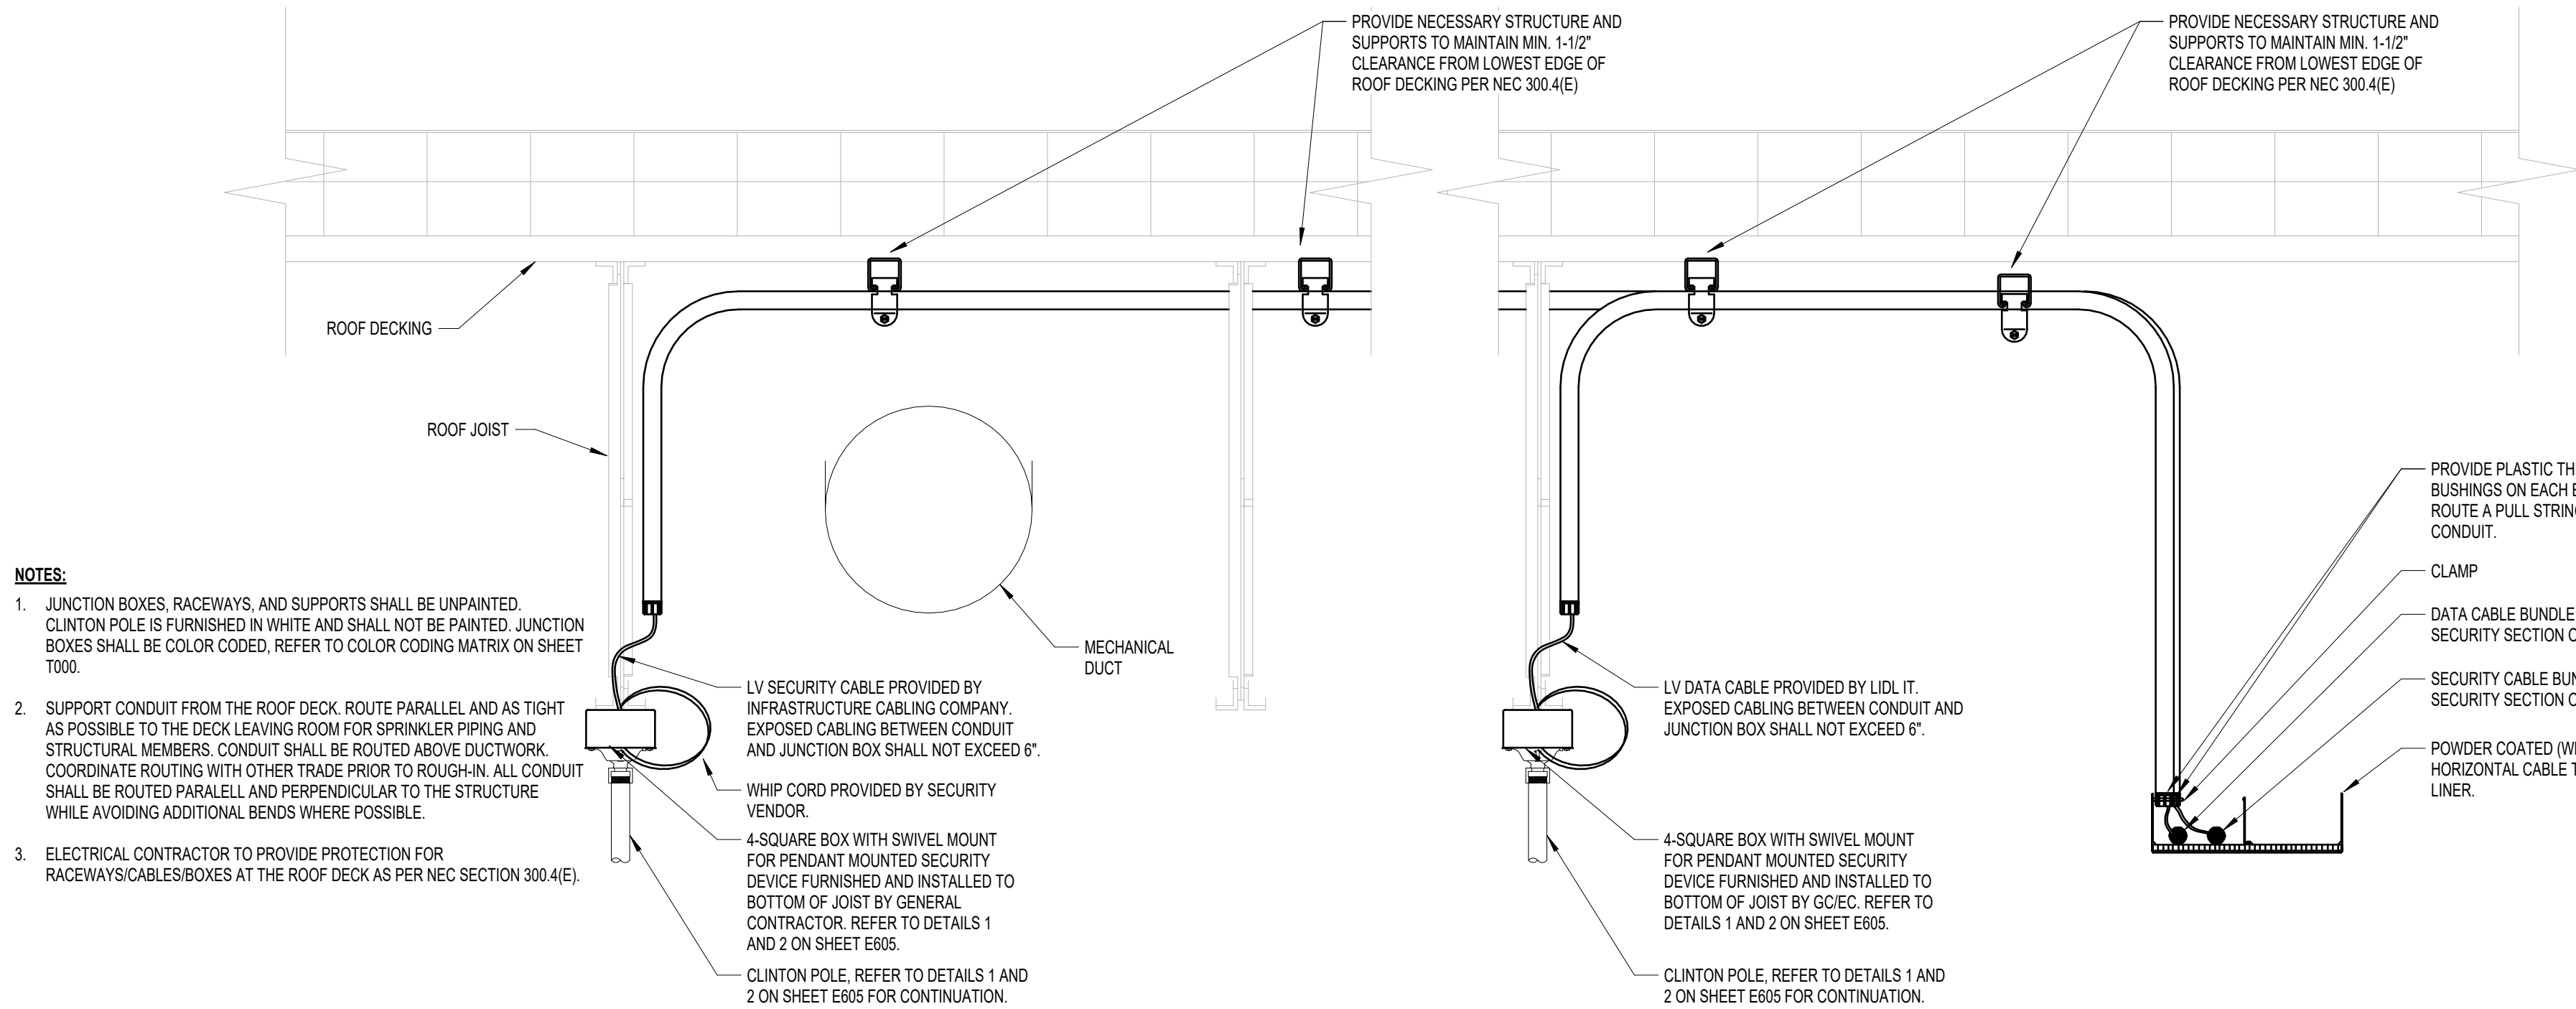


5 SALES AREA CABLE WIREWAY TO LOW VOLTAGE DEVICE CONDUIT ROUTING DETAIL

NTS

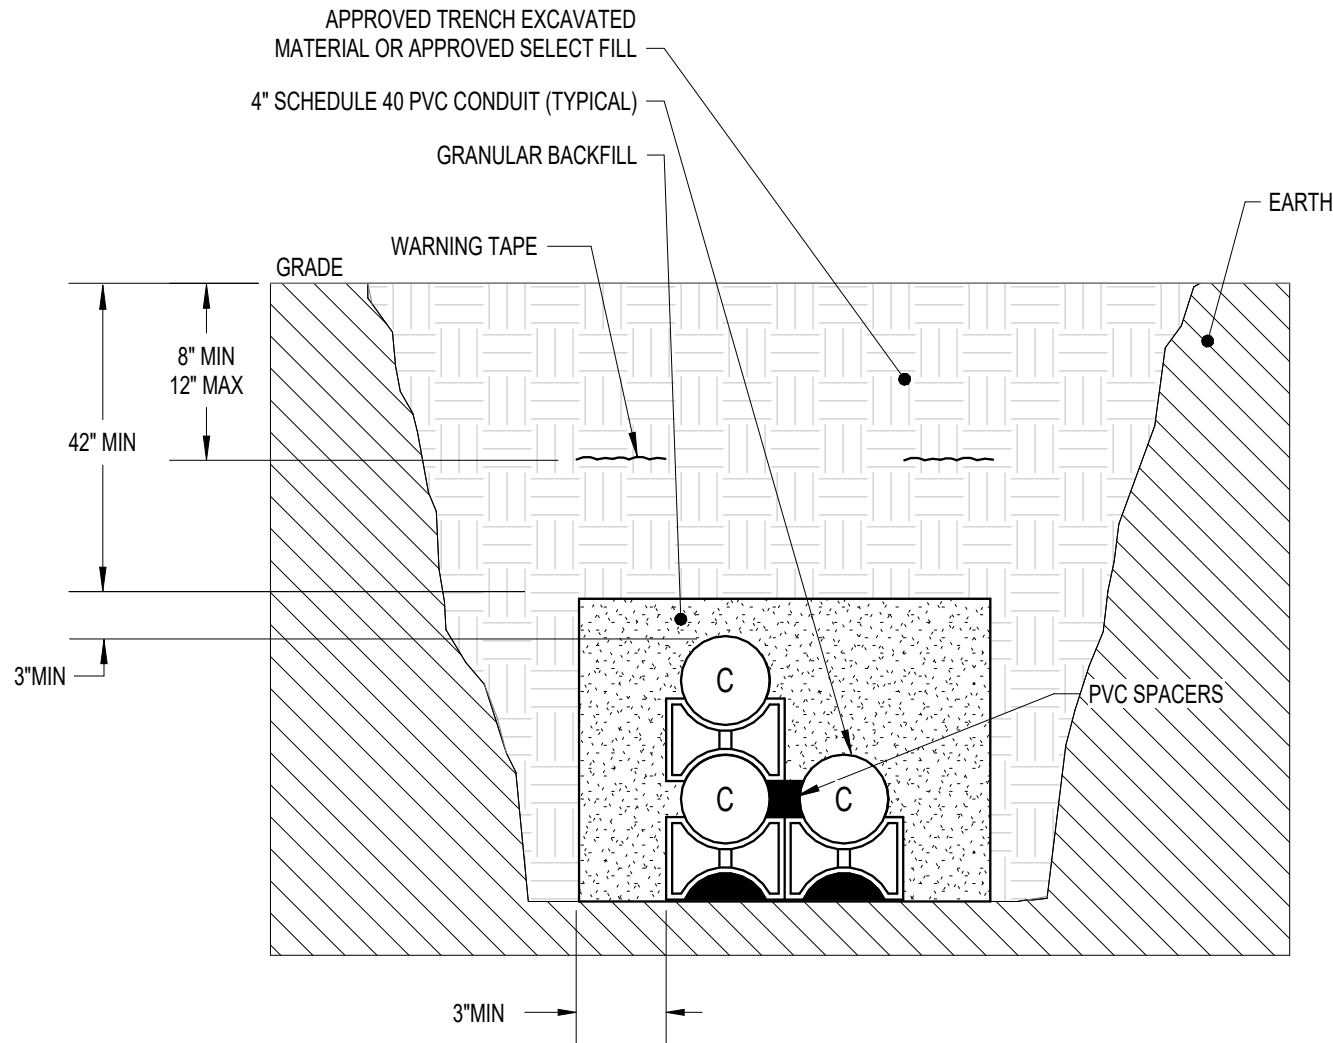


2 CONDUIT TRENCH DETAIL

NTS

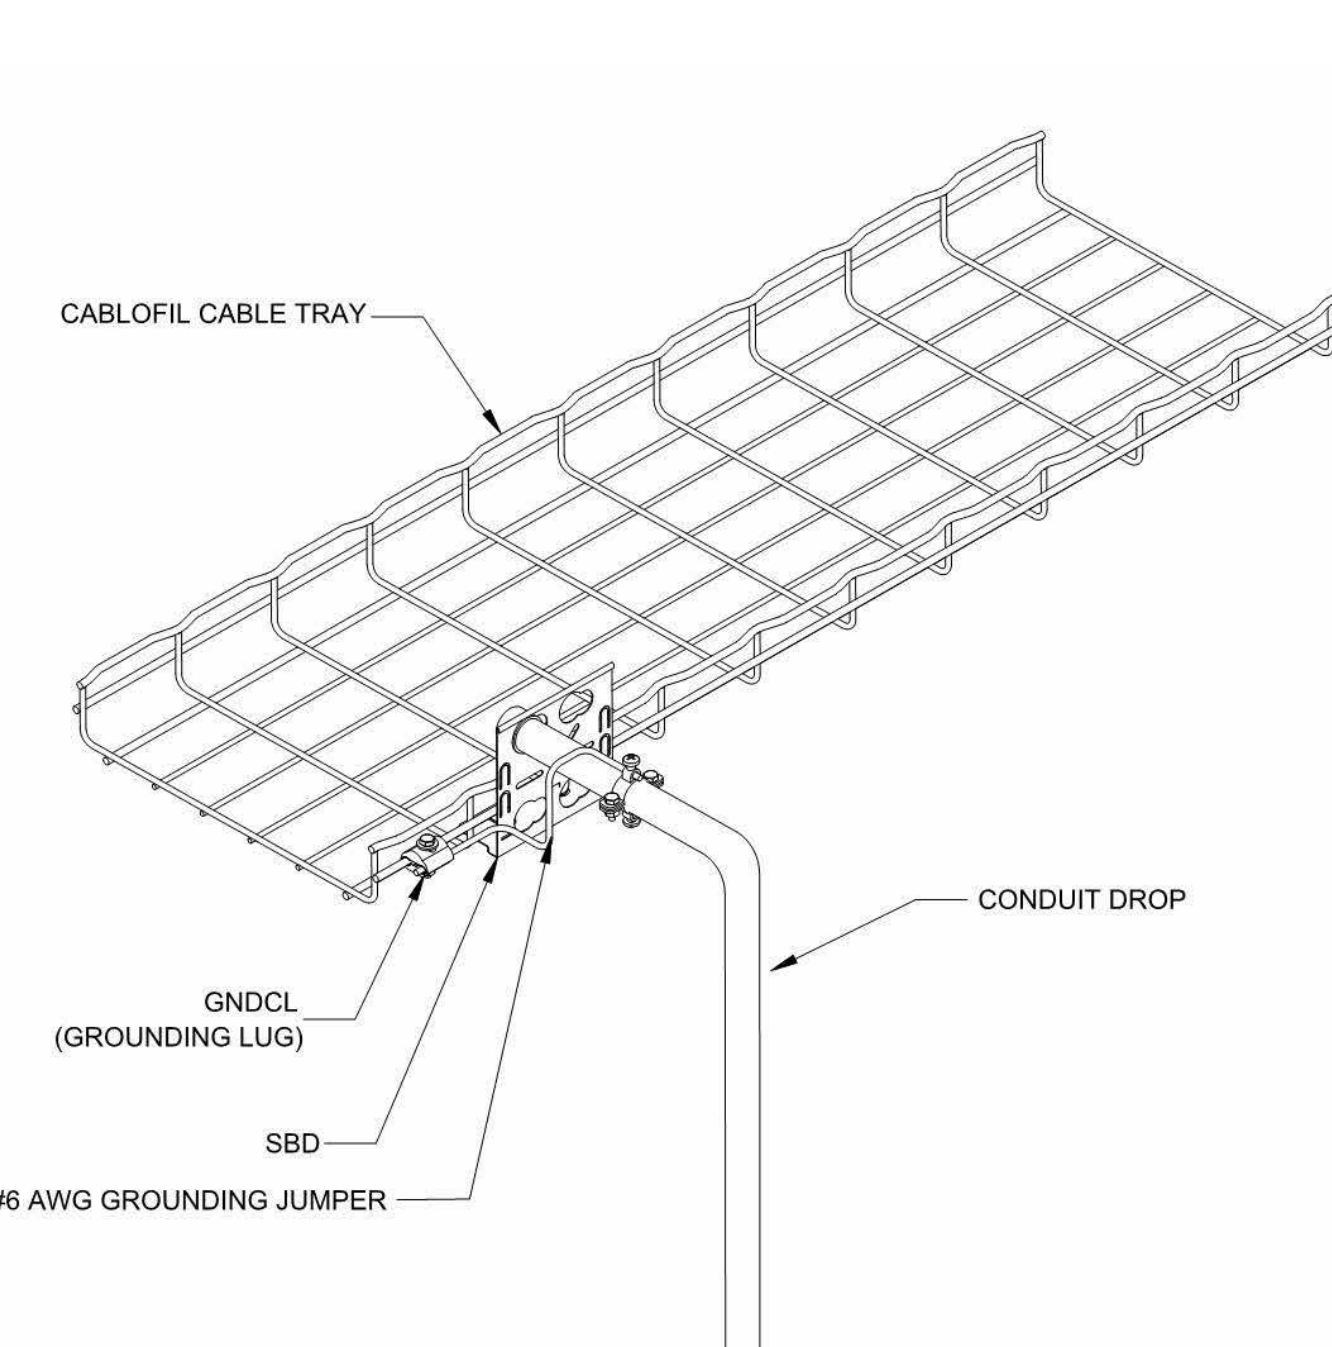


6 CABLE WIREWAY WITH CONDUIT DETAIL

NTS

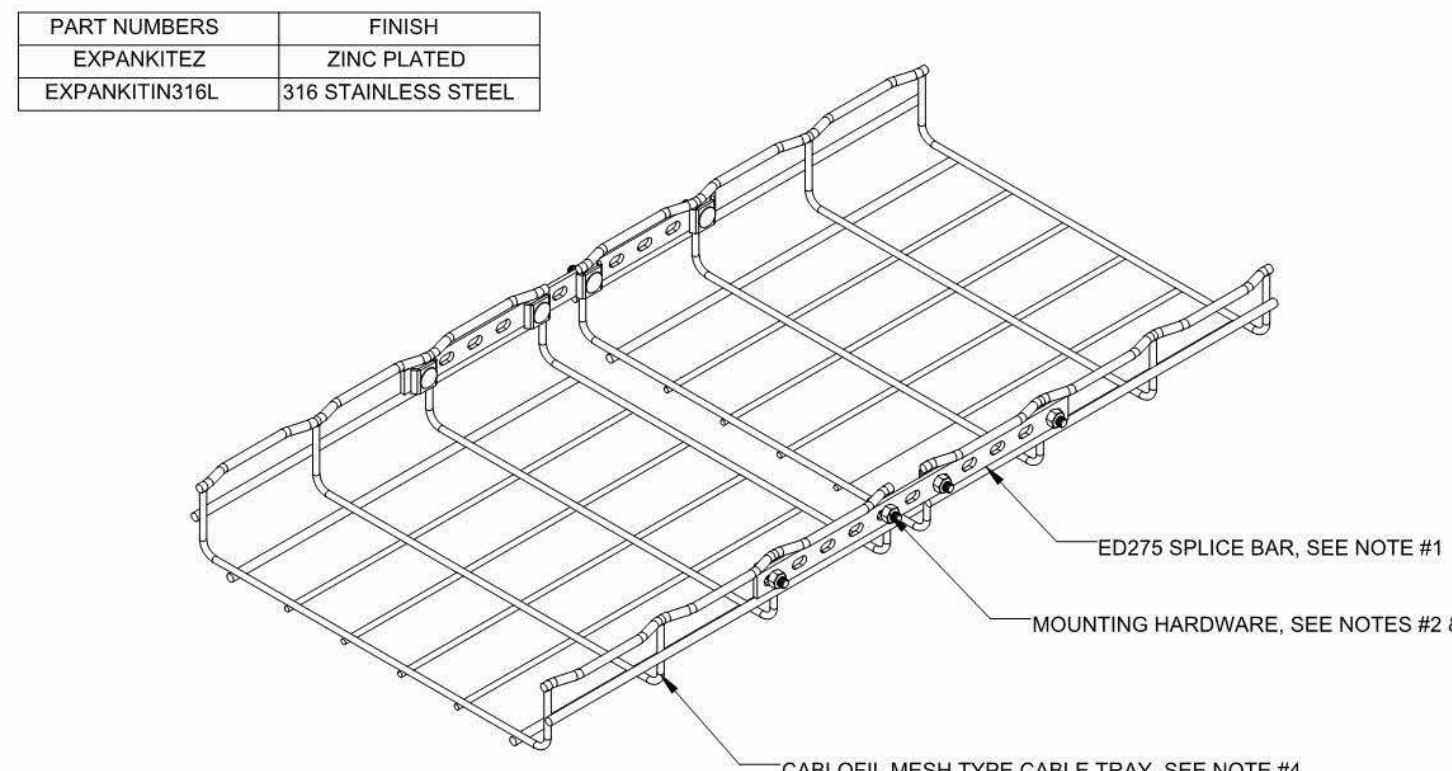

3 CABLE WIREWAY MOUNTING DETAILS

NTS

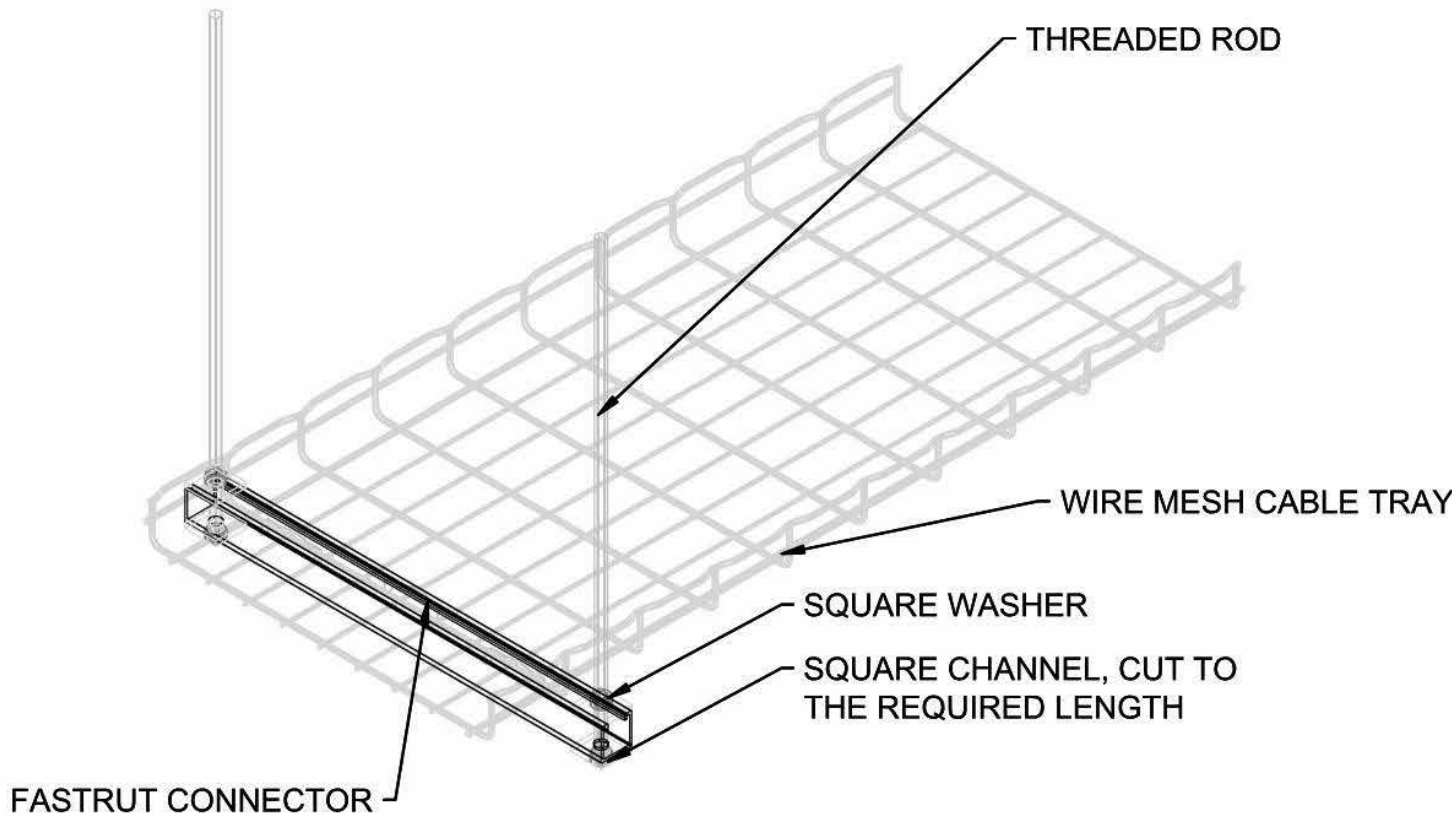




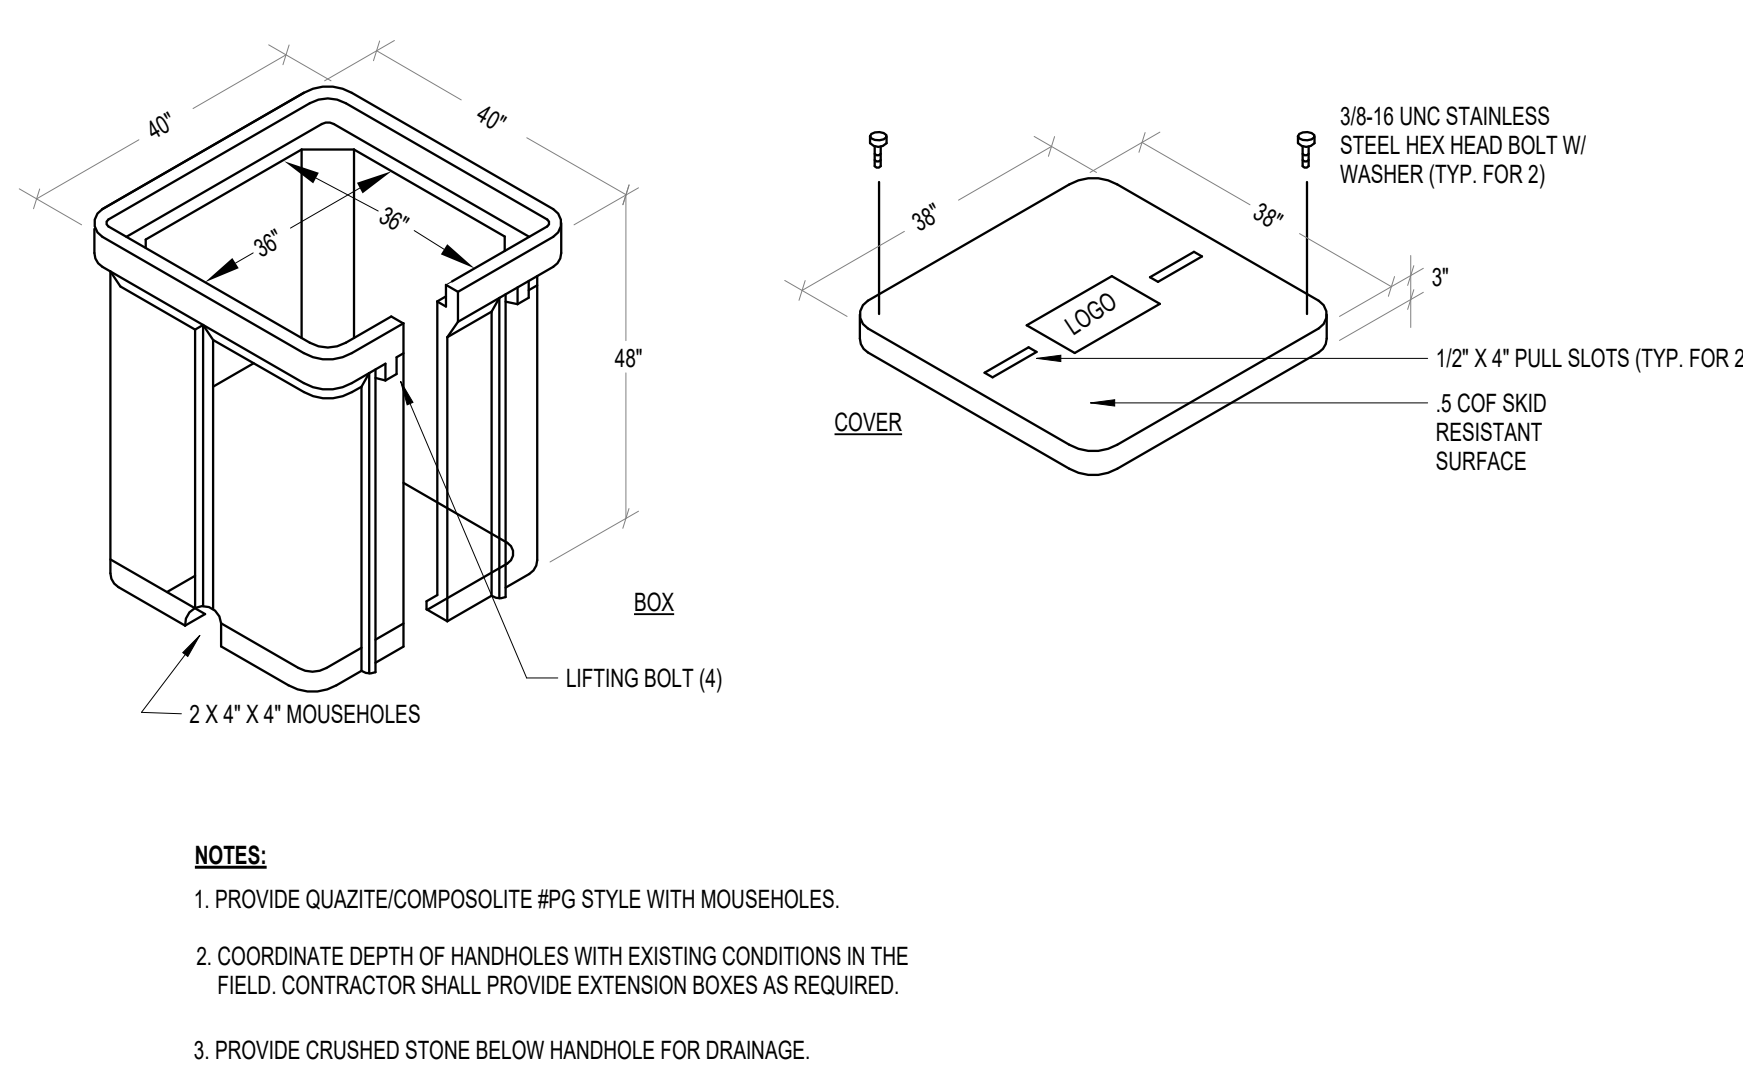



Diagram illustrating the assembly of a ceiling tile bridge. The components and labels are as follows:

- HANGER WIRE SECURED TO STRUCTURE ABOVE**: Points to the top of the vertical support rod.
- 3/4" EMT CONDUIT WITH PULL STRING AND COMPRESSION FITTINGS ROUTED TO CABE TRAY, SIZE AS NOTED ON PLANS (TYP.)**: Points to the vertical conduit.
- PROVIDE PLASTIC THREADED CONDUIT BUSHINGS ON EACH END OF CONDUIT**: Points to the conduit.
- SECONDARY SUPPORT POINT**: Points to the support bracket on the vertical rod.
- 18" ABOVE CEILING TILE**: Indicates the height of the support structure above the ceiling tile.
- TILE BRIDGE BY LIDL**: Points to the bridge structure.
- MOOD MEDIA RECESSED CEILING SPEAKER BY LIDL**: Points to the speaker mounted on the bridge.
- CEILING TILE**: Points to the ceiling tile.


- ## 1 BACK OF HOUSE ACCESSIBLE CEILING MOUNTED SPEAKER DETAIL

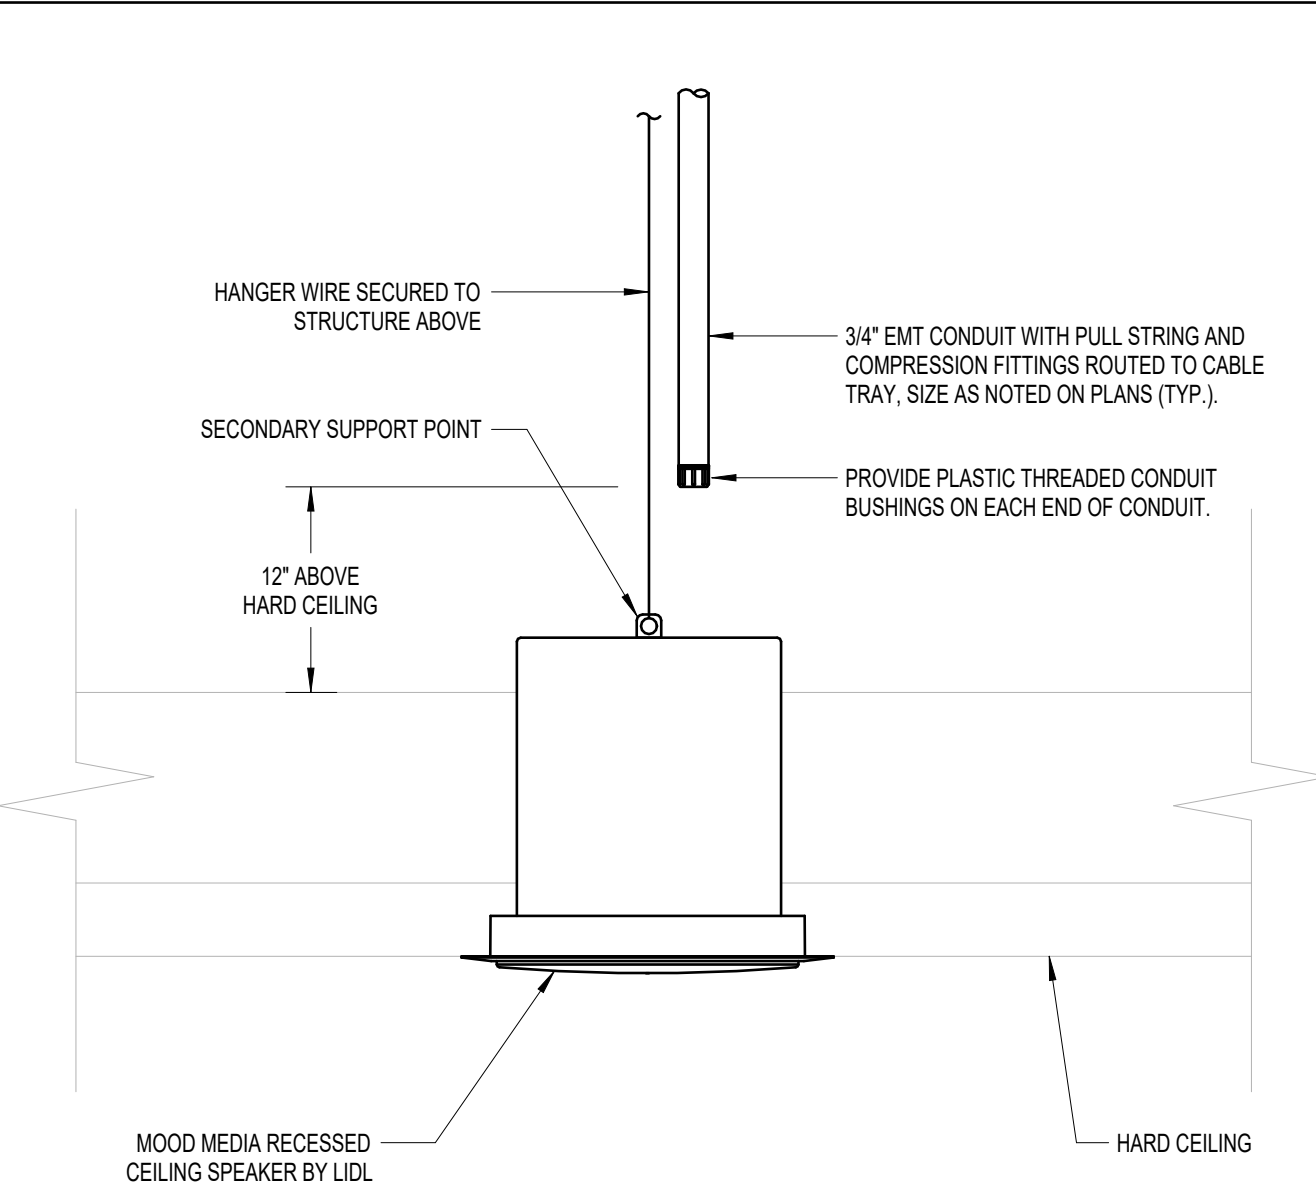

- ## 2 BACK OF HOUSE NON-ACCESSIBLE CEILING MOUNTED SPEAKER DETAIL

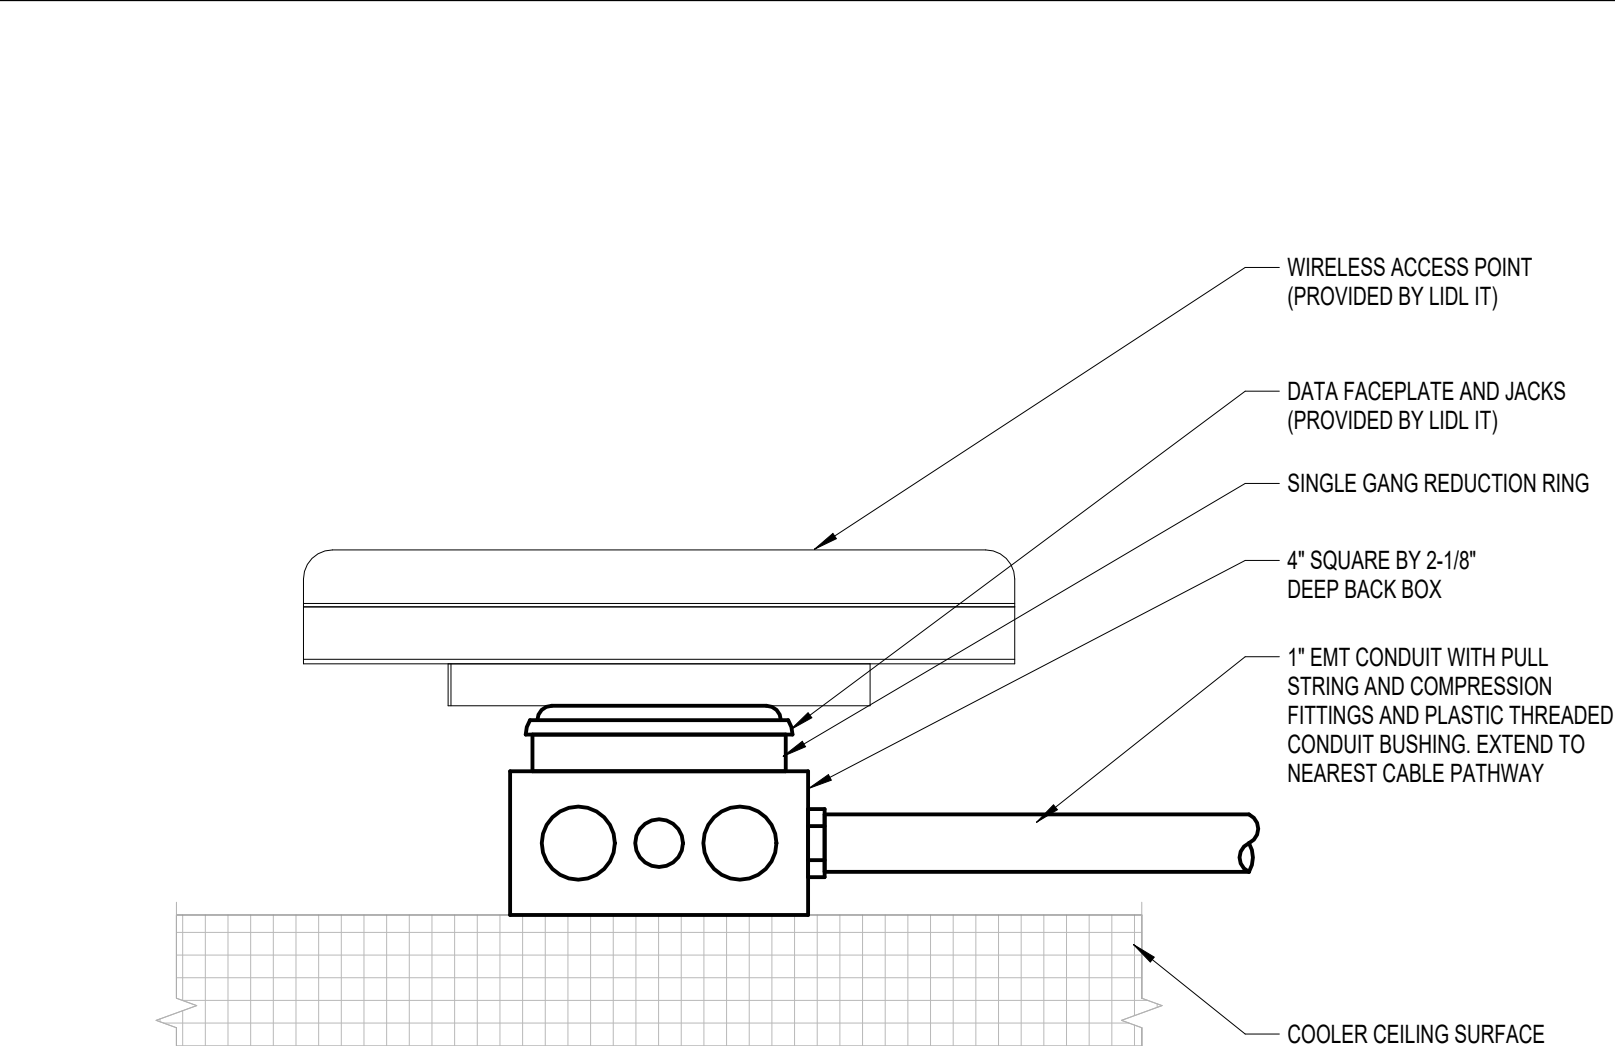

NTS

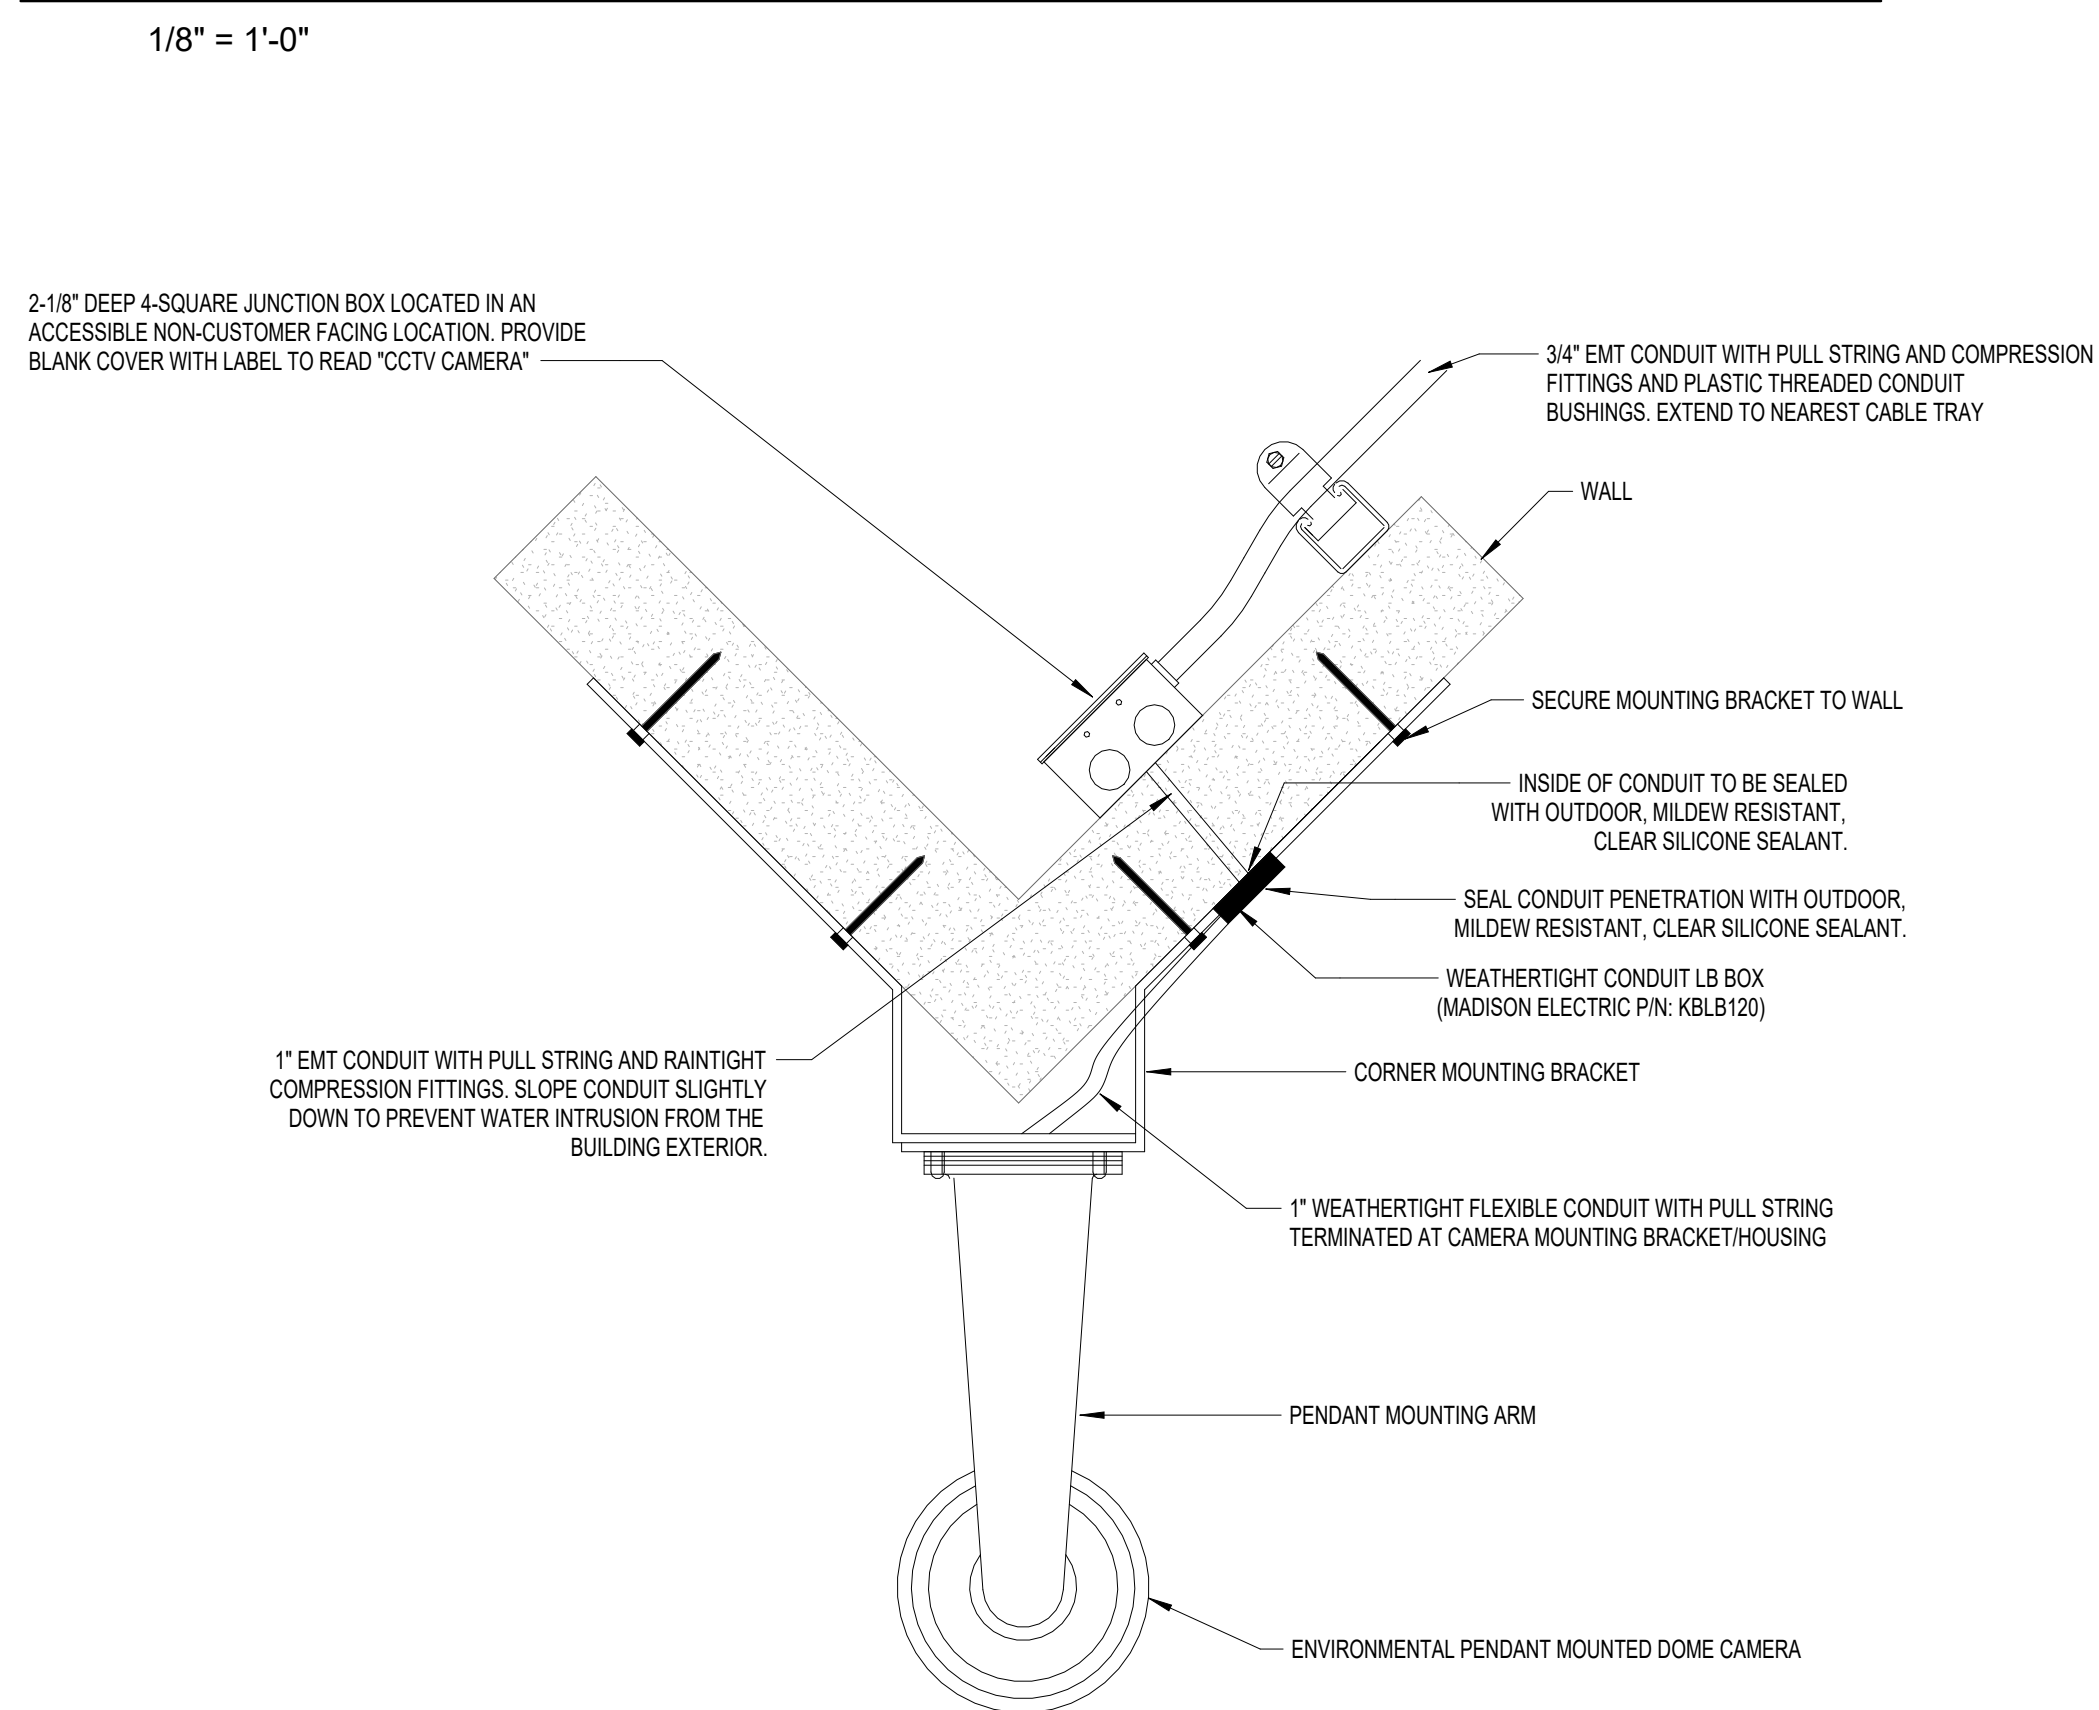

- TOP VIEW

BACK OF HOUSE

BUILDING EXTERIOR

3/4" EMT CONDUIT WITH PULL STRING AND COMPRESSION FITTINGS AND PLASTIC THREADED CONDUIT BUSHINGS. EXTEND TO NEAREST CABLE TRAY

2-1/8" DEEP 4-SQUARE JUNCTION BOX LOCATED IN AN ACCESSIBLE NON-CAMERA FACING LOCATION. PROVIDE BLANK COVER WITH LABEL TO READ "CCTV CAMERA"

1/2" MC CONDUIT WITH PULL STRING STUBBED OUT MIN. 1" BEYOND OUTSIDE EDGE OF WALL. COORDINATE EXACT LOCATION, STUB-OUT LENGTH, AND MEANS OF ATTACHMENT WITH TELAID PRIOR TO ROUGH-IN

SLOPE CONDUIT SLIGHTLY DOWN TO PREVENT WATER INTRUSION FROM BUILDING EXTERIOR.

SEAL CONDUIT PENETRATION WITH OUTDOOR, MILDEW RESISTANT, CLEAR SILICONE SEALANT.


PROVIDE PLASTIC THREADED CONDUIT BUSHINGS ON EACH END.

WALL MOUNTED OUTDOOR CCTV CAMERA FURNISHED AND INSTALLED BY TELAID.

MOUNTING HEIGHT (MH)
ABOVE FINISHED FLOOR
(REFER TO ARCHITECTURAL PLANS)

INSIDE OF CONDUIT TO BE SEALED BY TELAID WITH OUTDOOR, MILDEW RESISTANT, CLEAR SILICONE SEALANT.

CAMERA BRACKET EDGE TO BE SEALED AGAINST EXTERIOR WALL BY TELAID WITH OUTDOOR, MILDEW RESISTANT, SILICONE SEALANT. COLOR AS DETERMINED BY OWNER AND/OR ARCHITECT.
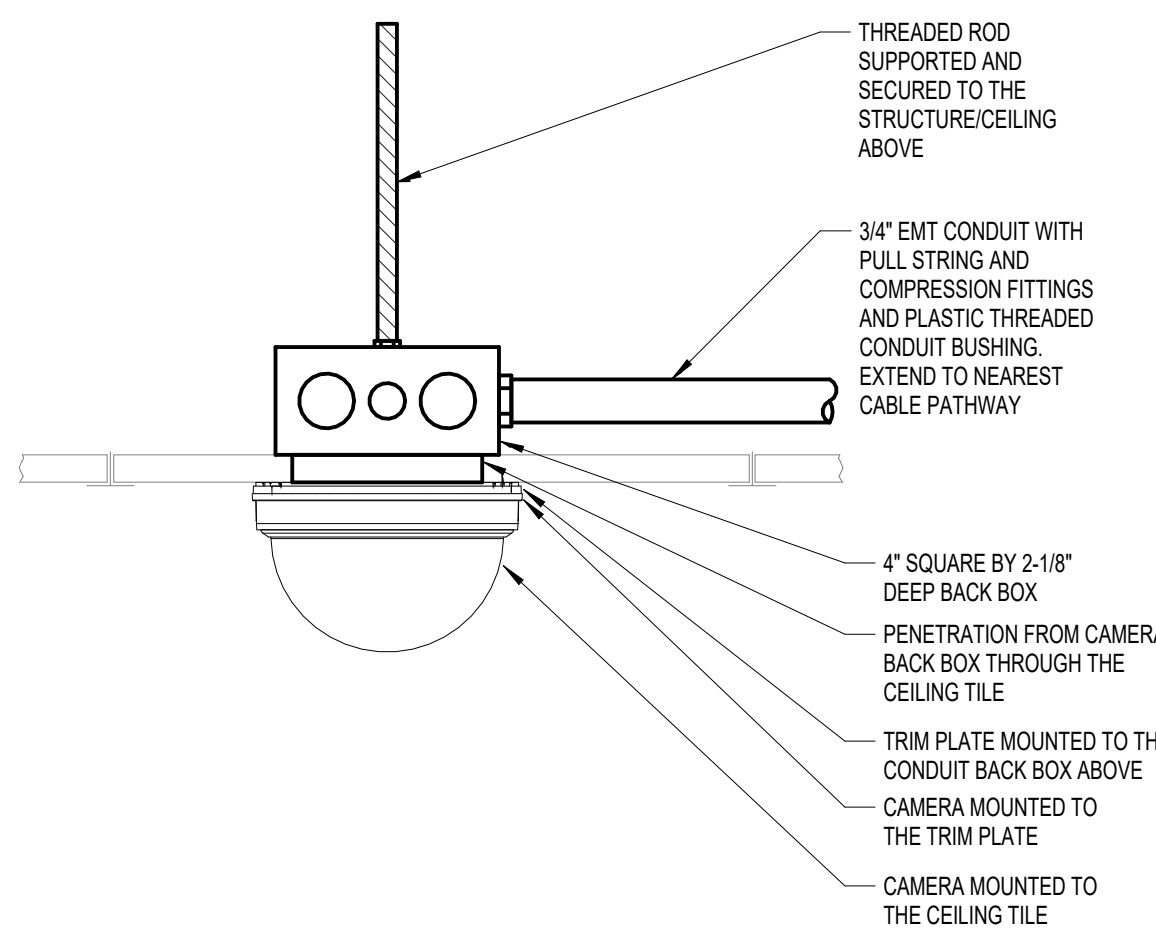
$$1/8'' = 1'-0''$$


NTS

12" = 1'-0"

JOB NO 3327865 **MODEL NUMBER** DCV-III1 **DRAWN BY** INITIALS **DATE** 3/6/2018 **DESCRIPTION OF OPERATION** Based on duct temperature inverter shut down time. Lights out in fire. Fire module based on duct temperature inverter shut down time. Phase meter required. From temperature sensor shipped with fire. Field installation distance between VFD and motor additional cost could apply if distance exceeds 50 feet.

JOB NAME LDR-PROTOTYPE-V4-LV_R1

1 **BREAKER PANEL TO PRIMARY CONTROL PANEL**
Responsibility: Electrician
BREAKER SIZE SHOWN IS THE MAXIMUM ALLOWED

2 **BREAKER PANEL** **PRIMARY CONTROL PANEL**

3 **BREAKER 1PH** **100 V** **15 A** **CONTROL POWER** **DO NOT WIRE TO SPEED OR SHUNT TRIP BREAKER** **DO NOT LIGHT BREAKER SHARED V/ CONTROL POWER SWITCH #1**

4 **BREAKER 1PH** **115V** **NCA** **7.5A** **MDCP** **15A** **KEF-1** **POWER TO ECM FANS**

5 **BREAKER PANEL TO FANS**
Responsibility: Electrician

6 **BREAKER 1PH** **115V** **NCA** **7.5A** **MDCP** **15A** **KEF-1** **POWER TO ECM FANS**

7 **CONTROL PANEL TO FANS**
Responsibility: Electrician

8 **PRIMARY PANEL** **FANS**

9 **FEED STP THROUGH INNER COOLING TUBE ALLOW FOR EXCESS SLACK IN STP FOR PROPER WINDING CHANNEL ONLY. NOTE: PWM SIGNAL IS POLARITY SENSITIVE.** **RD TO RD NINEC MOTOR BK TO OF TOLCUD MOTOR BK TO BK ZEDAL MOTOR BK TO BK** **KEF-1** **ECM-01** **FAN G1**

10 **CONTROL PANEL TO ACCESSORY ITEMS**
Responsibility: Electrician

11 **CONTROL PANEL** **COMPONENT**

12 **CONTROL PANEL TO SWITCHES** **ALL SWITCHES FACTORY WIRED TO CAT-5 CONNECTION**

13 **CONTROL PANEL TO HEAD LIGHTS** **1400 V MAX** **BLACK** **WHITE** **WIRE TO J-BOX ON TOP OF HEAD** **HEAD LIGHTS**

14 **CONTROL PANEL TO CAT-5 ETHERNET CONNECTION** **WIRE DIRECTLY TO COMMUNICATION MODULE. SEE CASLINK OWNERS MANUAL FOR FURTHER INSTRUCTIONS** **ROUTER**

15 **CONTROL PANEL TO WORLD WIDE WEB** **FACTORY WIRES TEMPERATURE SENSOR MOUNTED IN HEAD CAPTURE VOLUME.** **HEAD 1 CAPTURE 1**

16 **CONTROL PANEL TO SIGNAL SWITCH THROUGH BMS TO EXTERNAL VILL. ACTIVATE ZONE1 FANS AND LIGHTS** **BMS SWITCH**

17 **BUILDING FIRE ALARM TO HEAD FIRE SYSTEM**
Responsibility: ELECTRICAL / ALARM CONTRACTOR

18 **HEAD CONTROL PANEL** **BUILDING ALARM PANEL**

19 **CONTROL PANEL SIGNAL FOR BUILDING FIRE ALARM PANEL** **BUILDING ALARM PANEL**

20 **CONTROL PANEL SIGNAL FOR BUILDING TROUBLE ALARM** **BUILDING ALARM PANEL**


21 **FACTORY WIRING** **FIELD WIRING**

22 **PROTOTYPE SHOP DRAWINGS**

23 **RIGHT WALL** **LEFT-HAND UTILITY CABINET**

24 **PROTYPING**

1. DRAWING FOR REFERENCE ONLY. ELECTRICAL CONTRACTOR IS RESPONSIBLE FOR PROVIDING AND INSTALLING ALL CABLE, CONDUCTOR AND CONDUIT ASSOCIATED WITH "FIELD WIRING" ONLY.

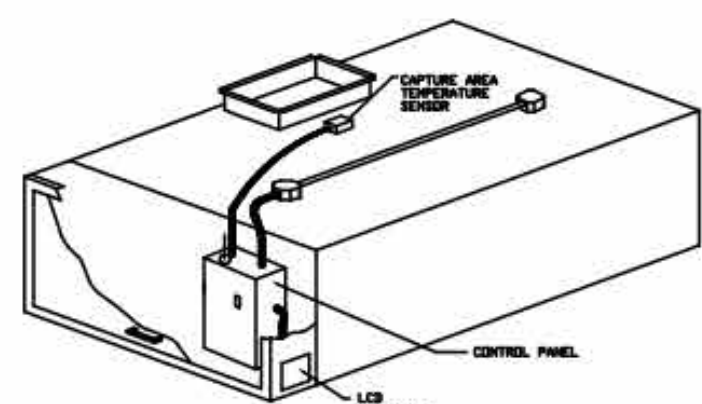

FACTORY WIRING
FIELD WIRING


PROTOTYPE SHOP DRAWINGS



CAPTIVE AIRE

JOB/BLIDL-PROTOTYPE [RIGHT WALL]	
LOCATION	
DATE 10/26/2022	JOB # VARIES
DWG # 7	DRAWN BY BT-32
REV.	SCALE



PROTOTYPE SHOP DRAWINGS

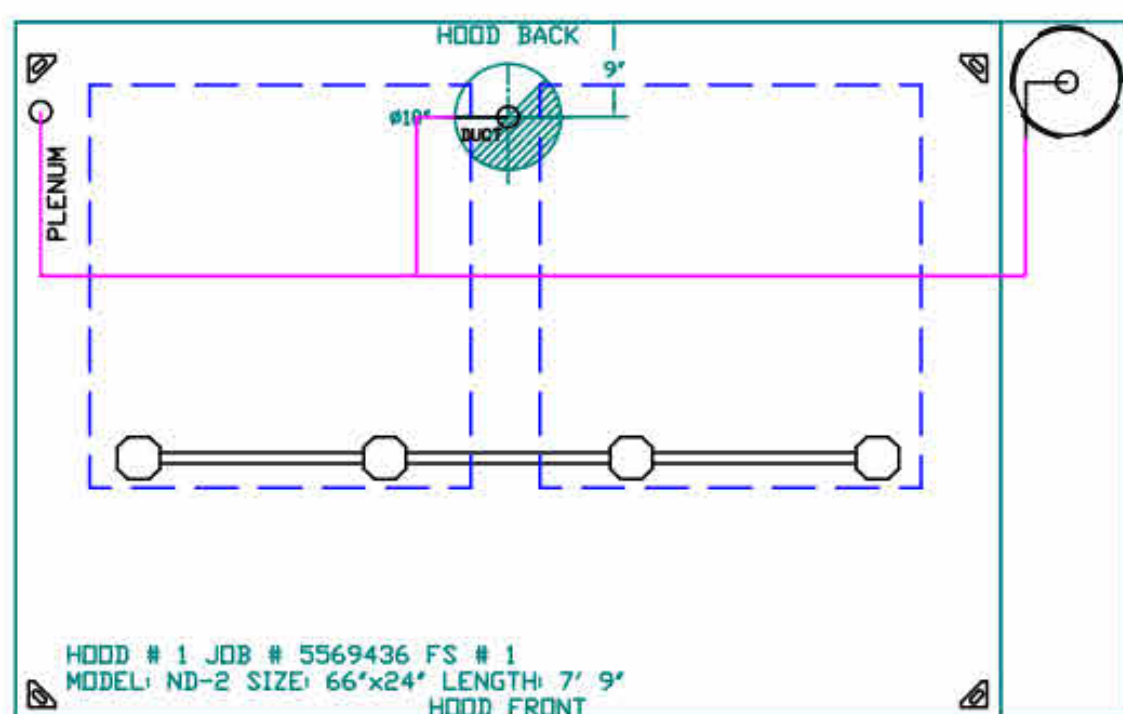

SYSTEM REQUIRES A MINIMUM OF 7 FT OF EQUIVALENT PIPE LENGTH BETWEEN TANK AND NEAREST APPLIANCE NOZZLE FOR MOST APPLIANCES. EACH 90 DEGREE ELBOW ADDS 1.3 FT OF EQUIVALENT LENGTH. SEE MANUAL FOR DETAILS

- FACTORY PIPING EXTENDS A MAXIMUM OF 6' ABOVE THE TOP OF THE HOOD.
- THIS FIRE SYSTEM COMPLIES WITH U.L. 300 REQUIREMENTS

Job Name: LIDL-PROTOTYPE-V4 [LEFT CAB].R1
 Drawn By:
 System Size: TANK-4.0 Total FP required: 3
 Hood # 1 11' 3.00' Long x 66" Wide x 24" High
 Riser # 1 Size: 12" Dia.
 Hood # 1 Metal Blow-Off Caps included.

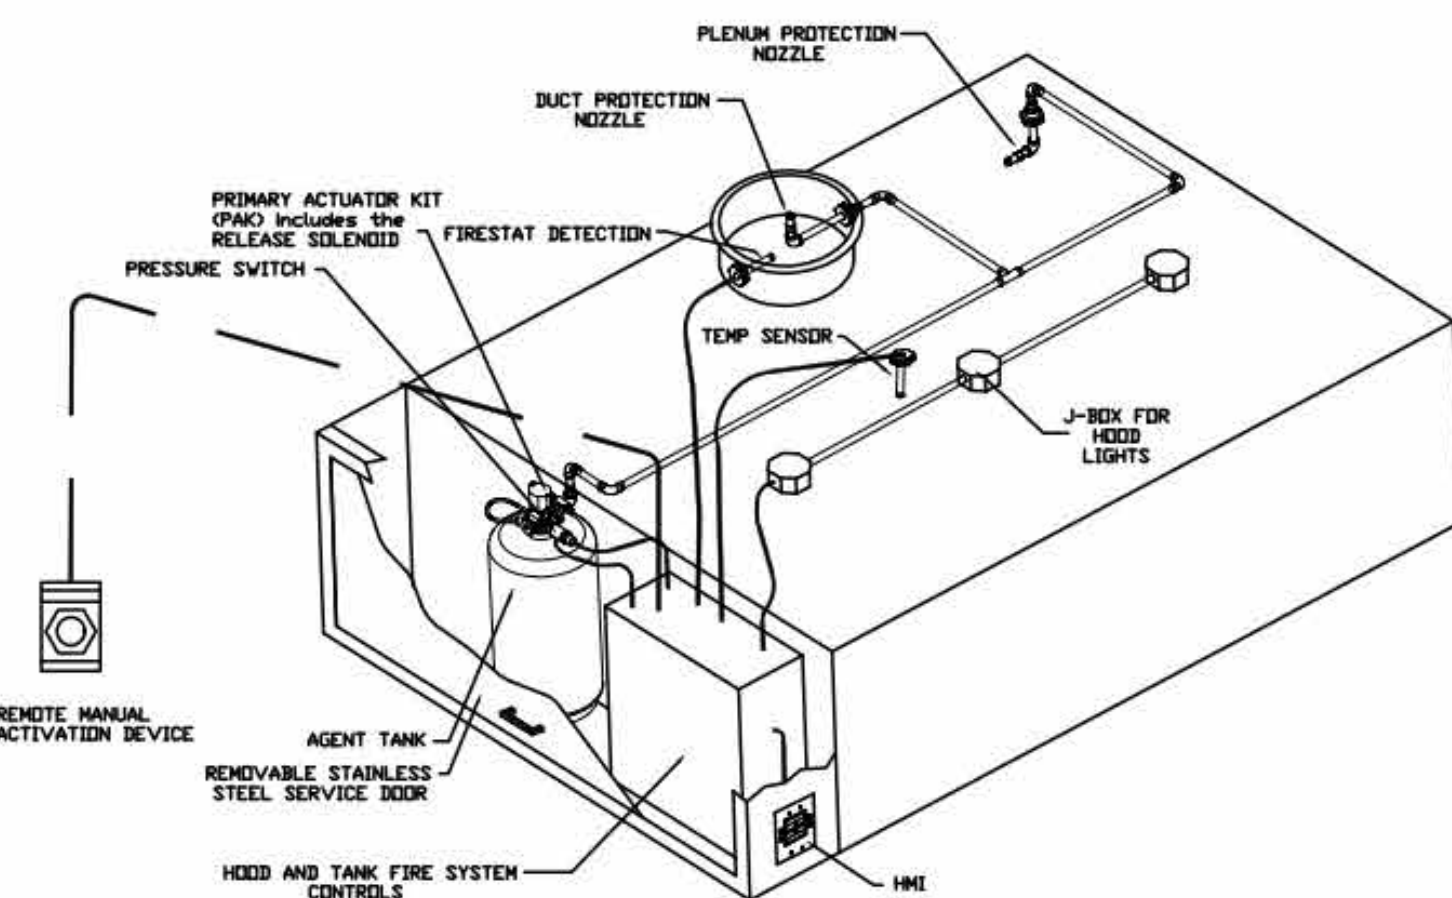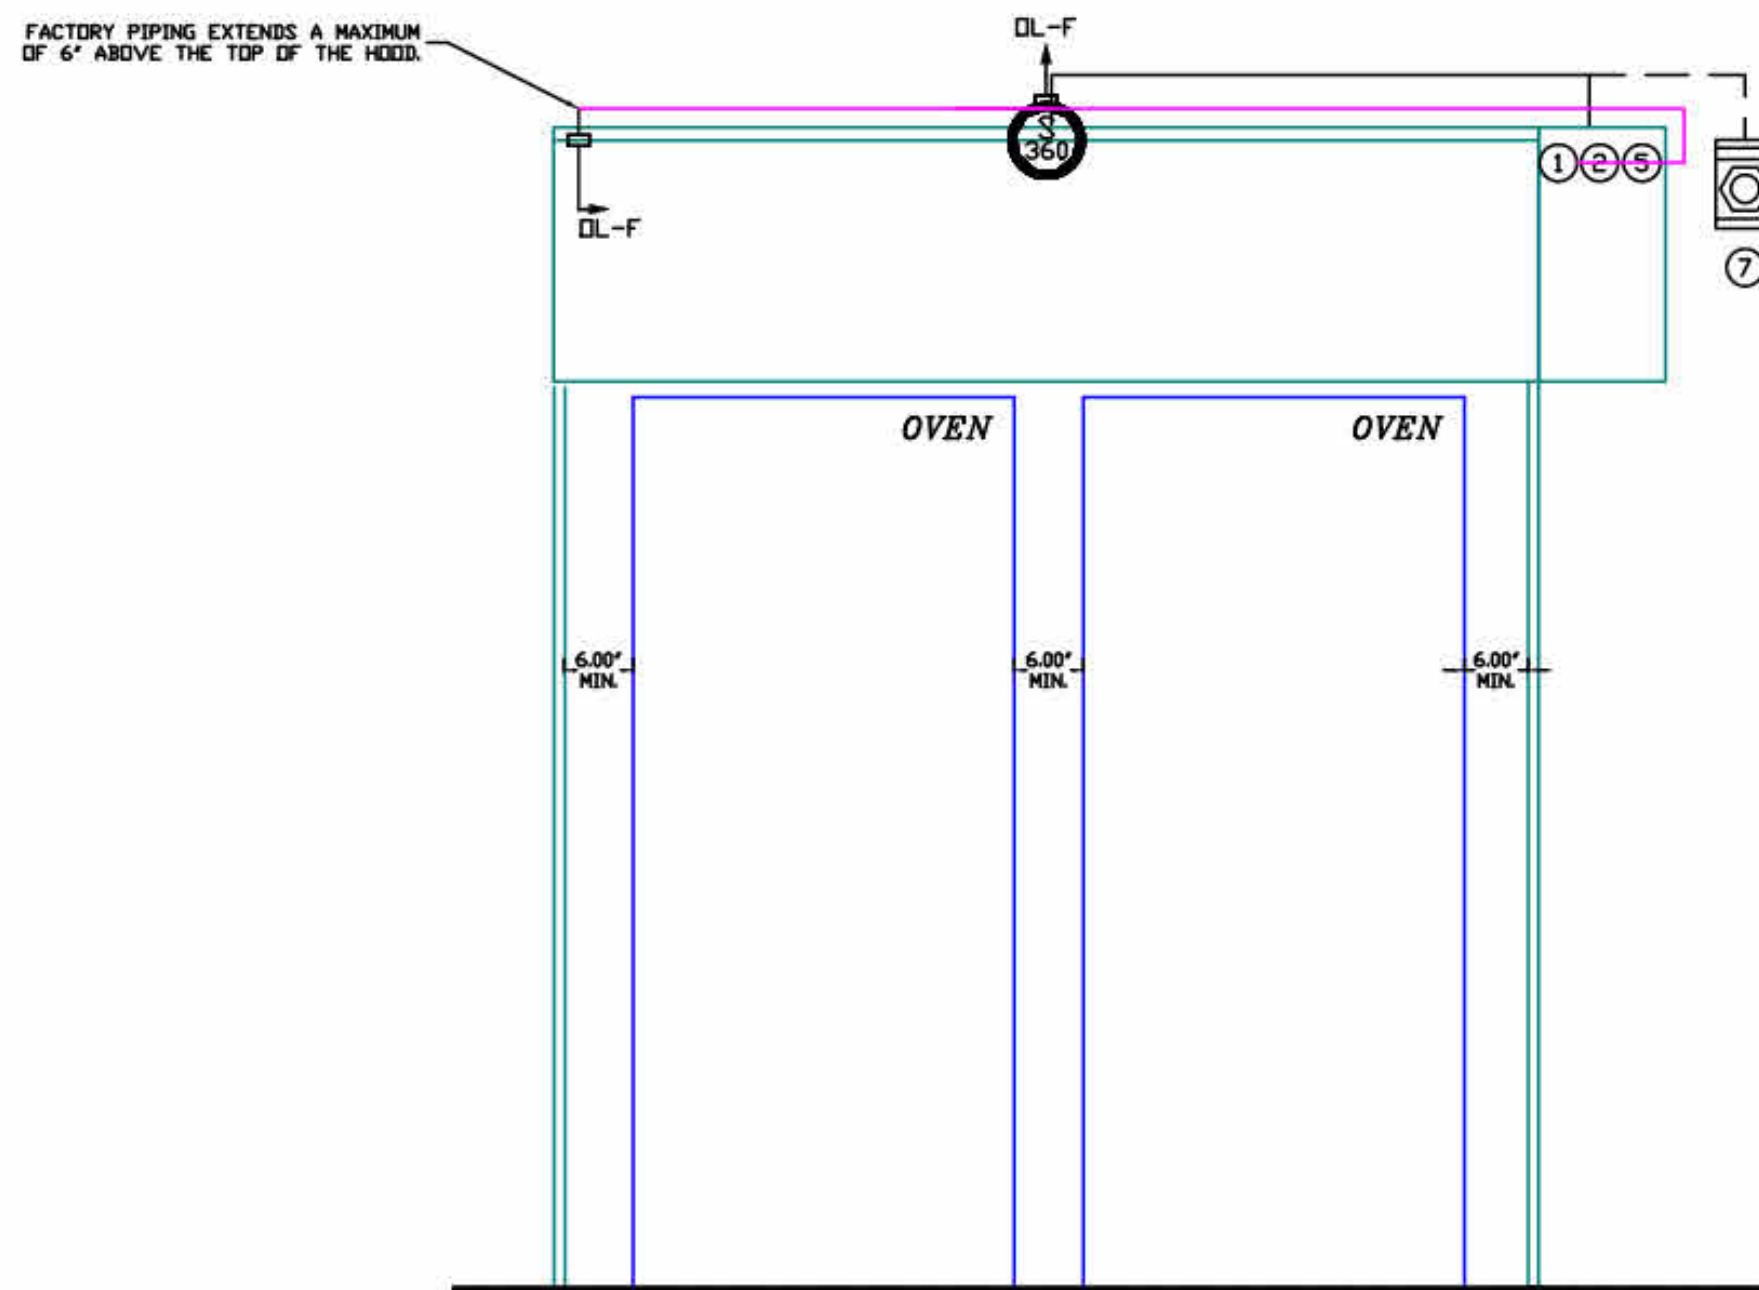


TYPICAL HOOD and TANK FIRE SYSTEM LAYOUT
THIS DETAIL IS GENERIC AND IS NOT INTENDED TO COVER ALL POSSIBLE, ACCEPTABLE SCENARIOS.
REFER TO PROJECT DRAWINGS/SCHEMATICS FOR DETAILS.



CAPTIVE AIRE

<i>JOB</i> LIDL-PROTOTYPE [RIGHT WALL]	
<i>LOCATION</i>	
<i>DATE</i> 10/26/2022	<i>JOB #</i> VARIET
<i>DWG #</i> 4	<i>DRAWN BY</i> BT-32
<i>REV</i>	<i>SCALE</i>

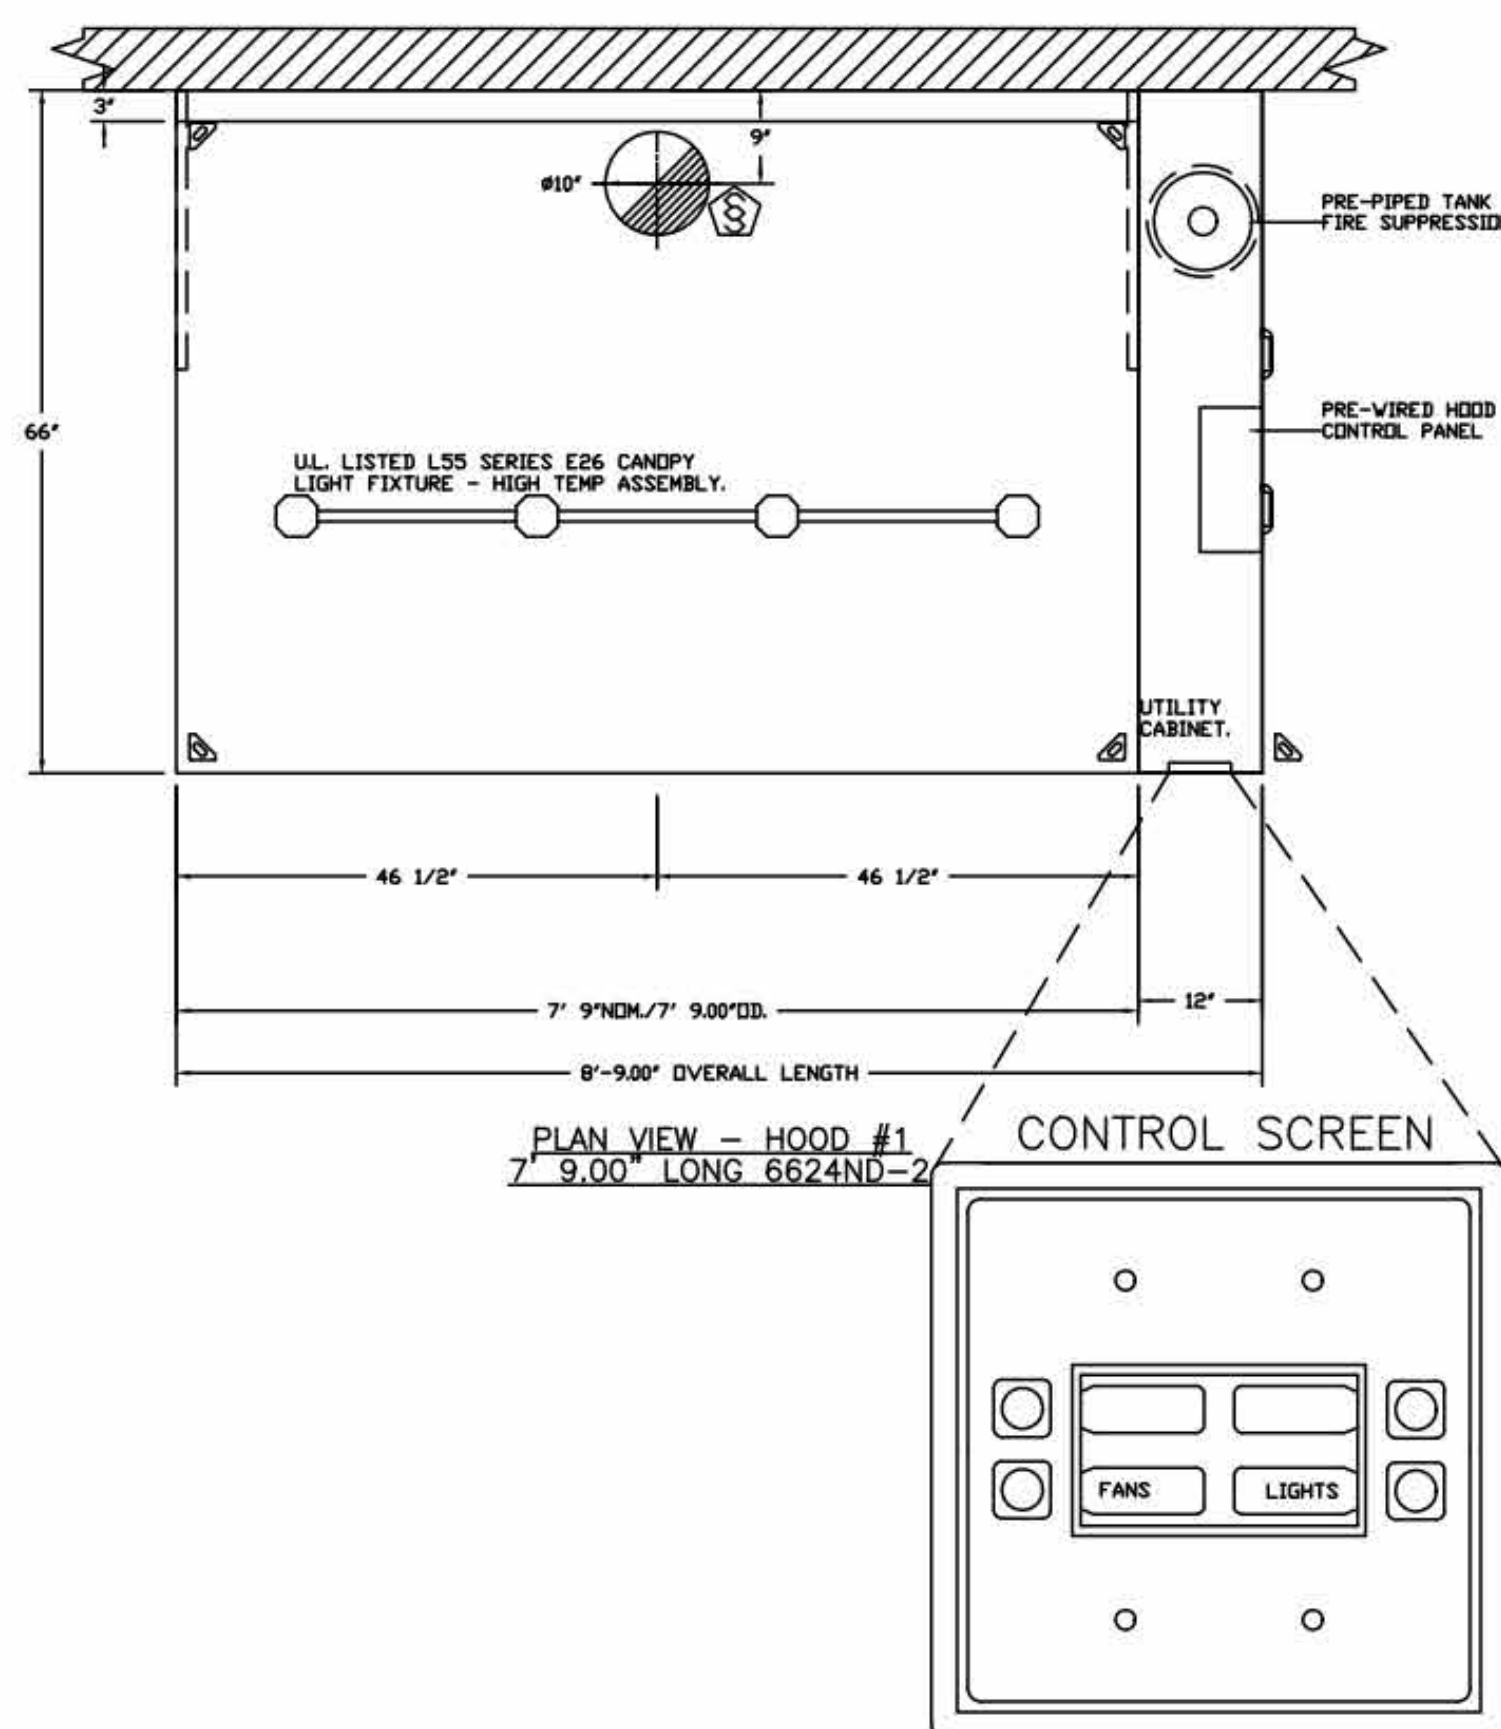

CAPTIVE AIRE

JOB/IDL-PROTOTYPE [RIGHT WALL]	
LOCATION	
DATE 10/26/2022	JOB # VARIES
DWC # 2	DRAWN BY BT-32
REV.	SCALE

INDIAN

LIDL 1517 NORCROSS, GA

4990 JIMMY CARTER BLVD. NORCROSS, GA 30093

PROGRESSIVE
COMPANIES




ISSUANCE

1	12/18/2025	PERMIT CYCLE 2
---	------------	----------------

PROJECT NUMBER
79650191
PROJECT MANAGER
A. HENGSTEBEC
PROFESSIONAL
D. HERSCHER
DRAWN BY
M. GONZALEZ
CHECKED BY
D. HERSCHER


ELECTRICAL - BAKERY HOOD DETAILS E606

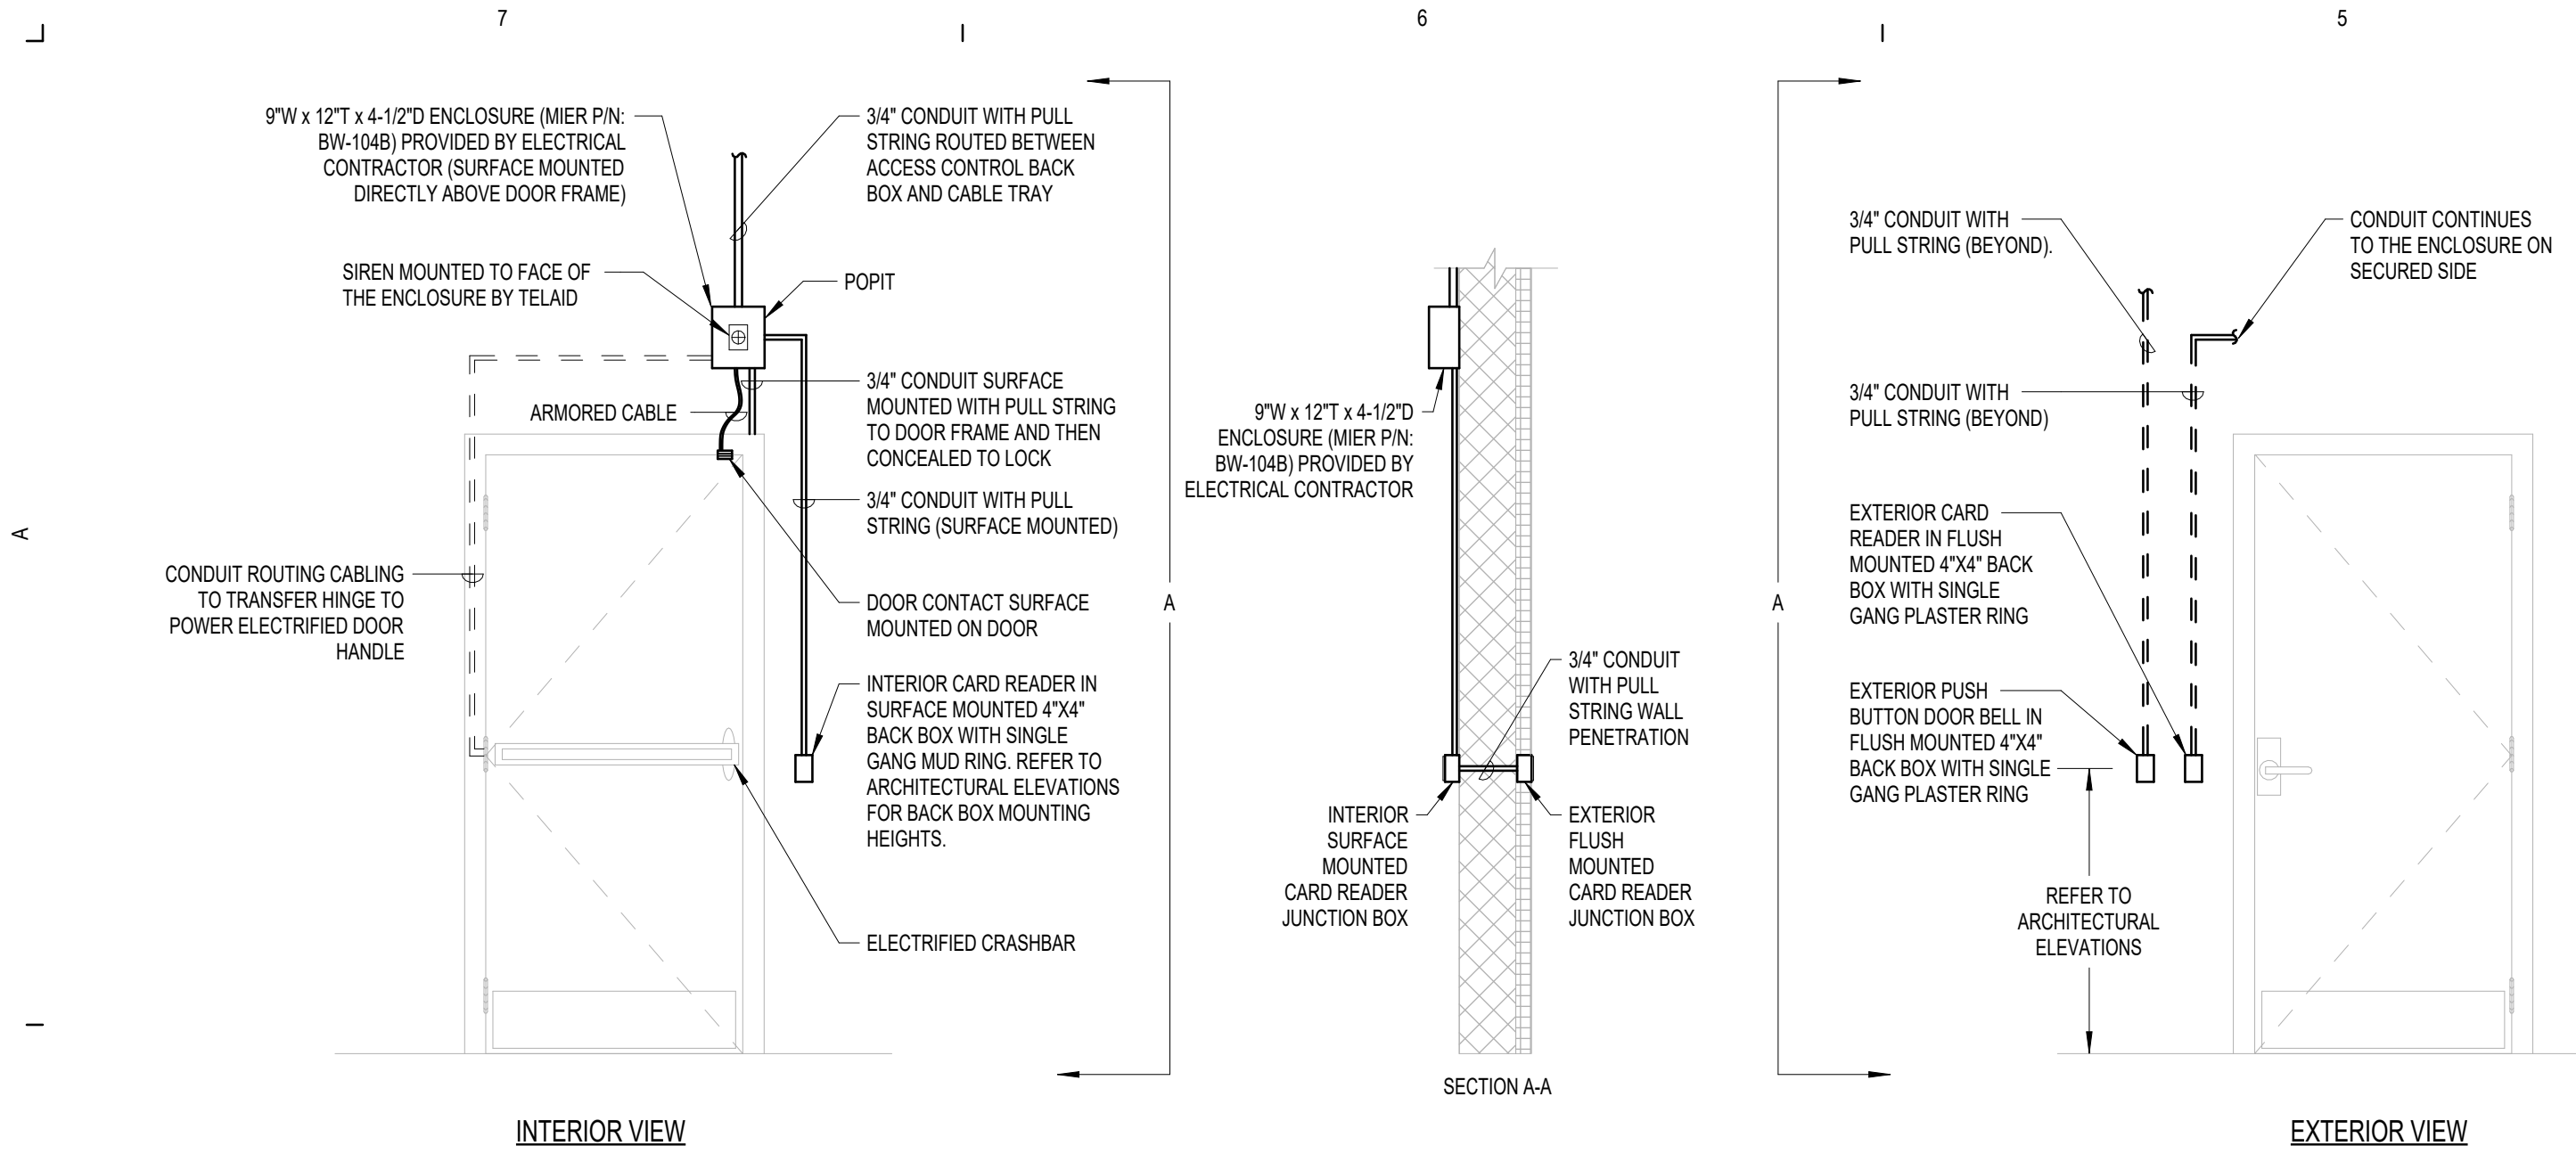

- NOTES:
1. ALL CONDUITS SHALL BE 3/4" UNLESS NOTED OTHERWISE.
 2. REFER TO FLOOR PLANS FOR EXACT DOOR SWING.
 3. REFER TO SHOP DRAWINGS FOR EXACT CONDUIT ROUGH-IN LOCATIONS.
 4. PROVIDE PULL STRINGS IN ALL CONDUITS.

3 SINGLE DOOR - TYPE 4


NTS

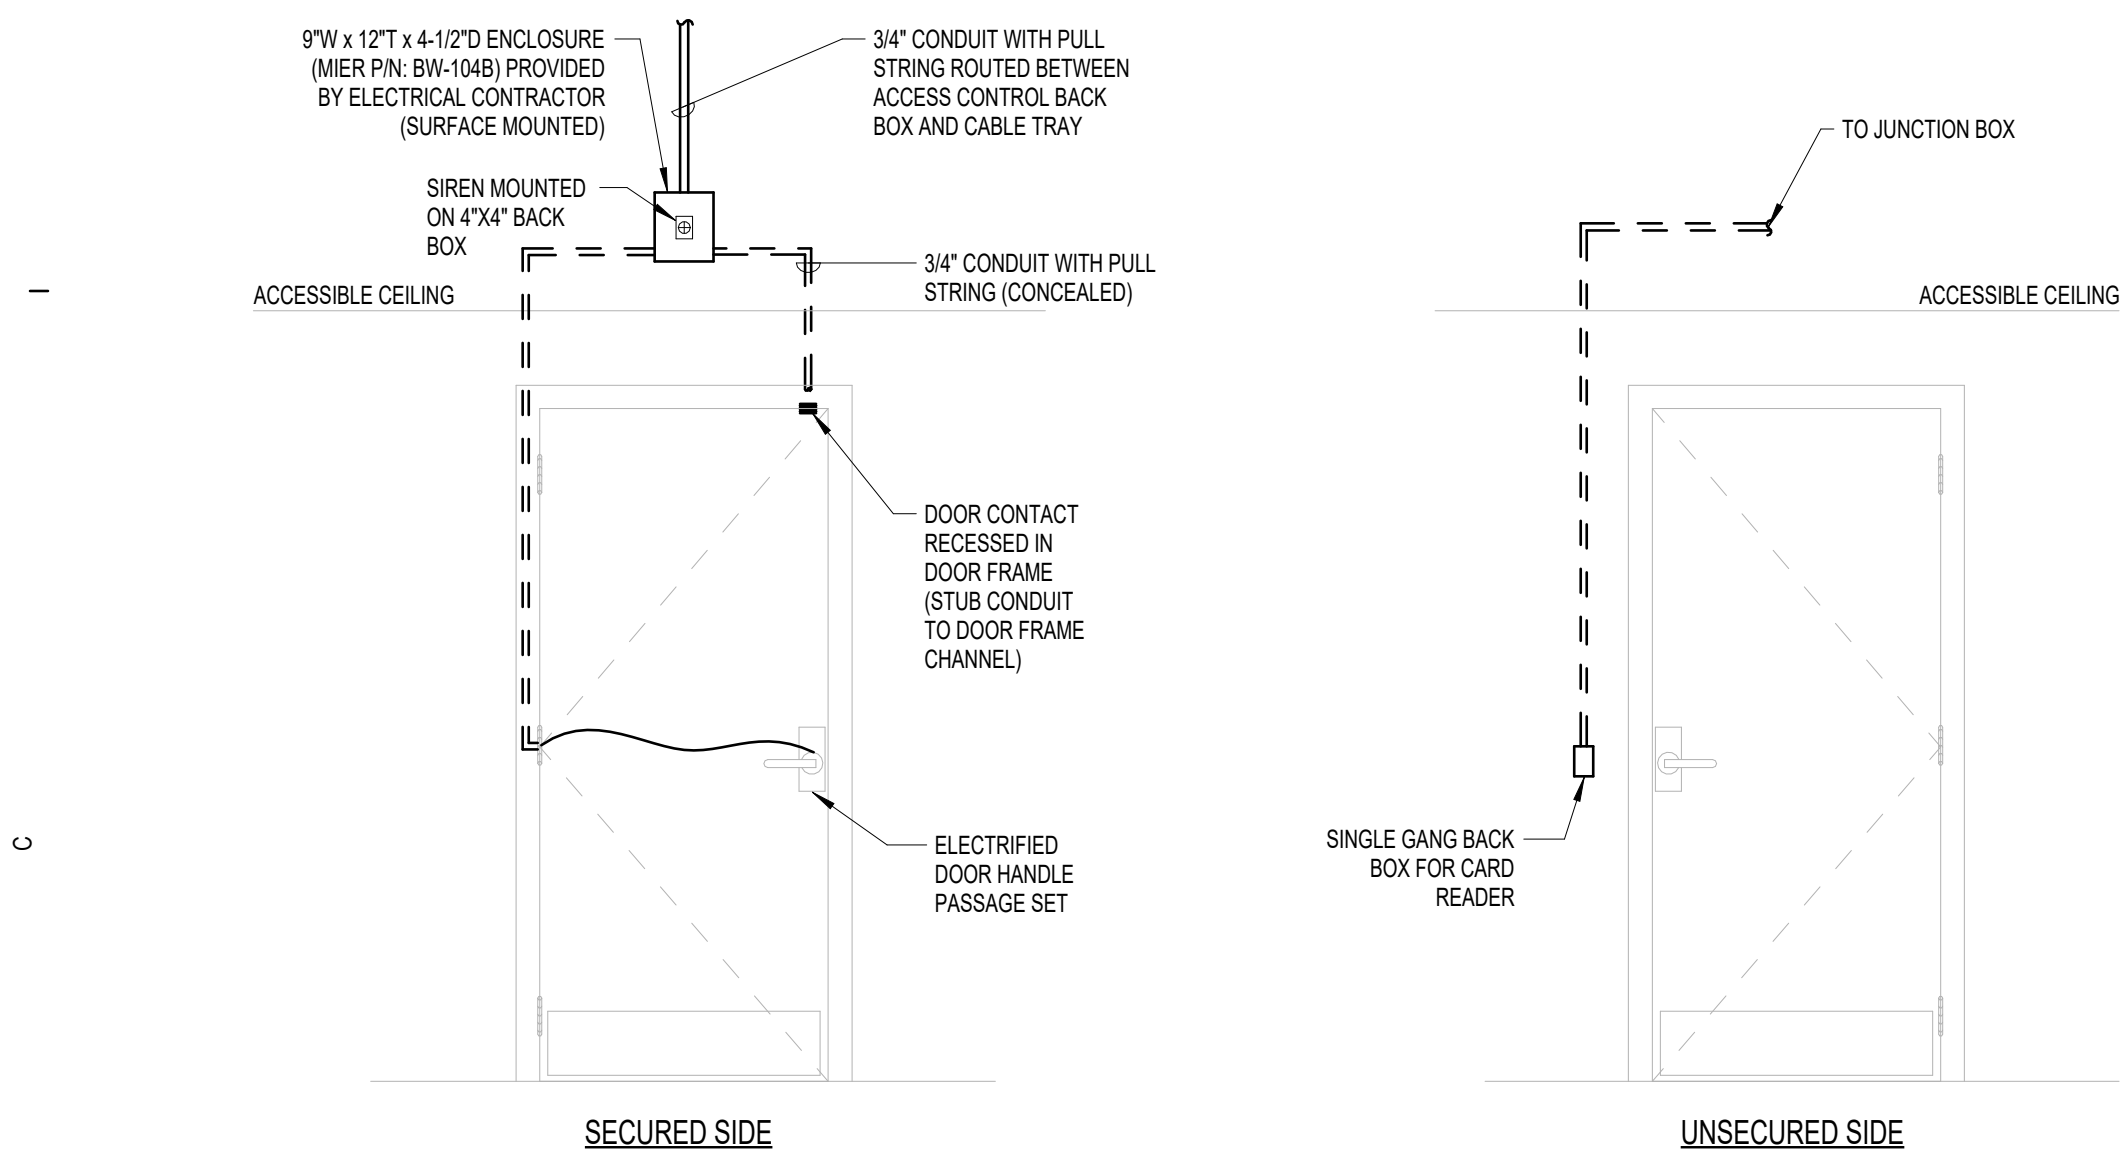

- NOTES:
1. ALL CONDUITS SHALL BE 3/4" UNLESS NOTED OTHERWISE.
 2. REFER TO FLOOR PLANS FOR EXACT DOOR SWING.
 3. REFER TO SHOP DRAWINGS FOR EXACT CONDUIT ROUGH-IN LOCATIONS.
 4. PROVIDE PULL STRINGS IN ALL CONDUITS.

4 SINGLE DOOR WITH CARD READER, SIREN & ELECTRIC STRIKE


NTS

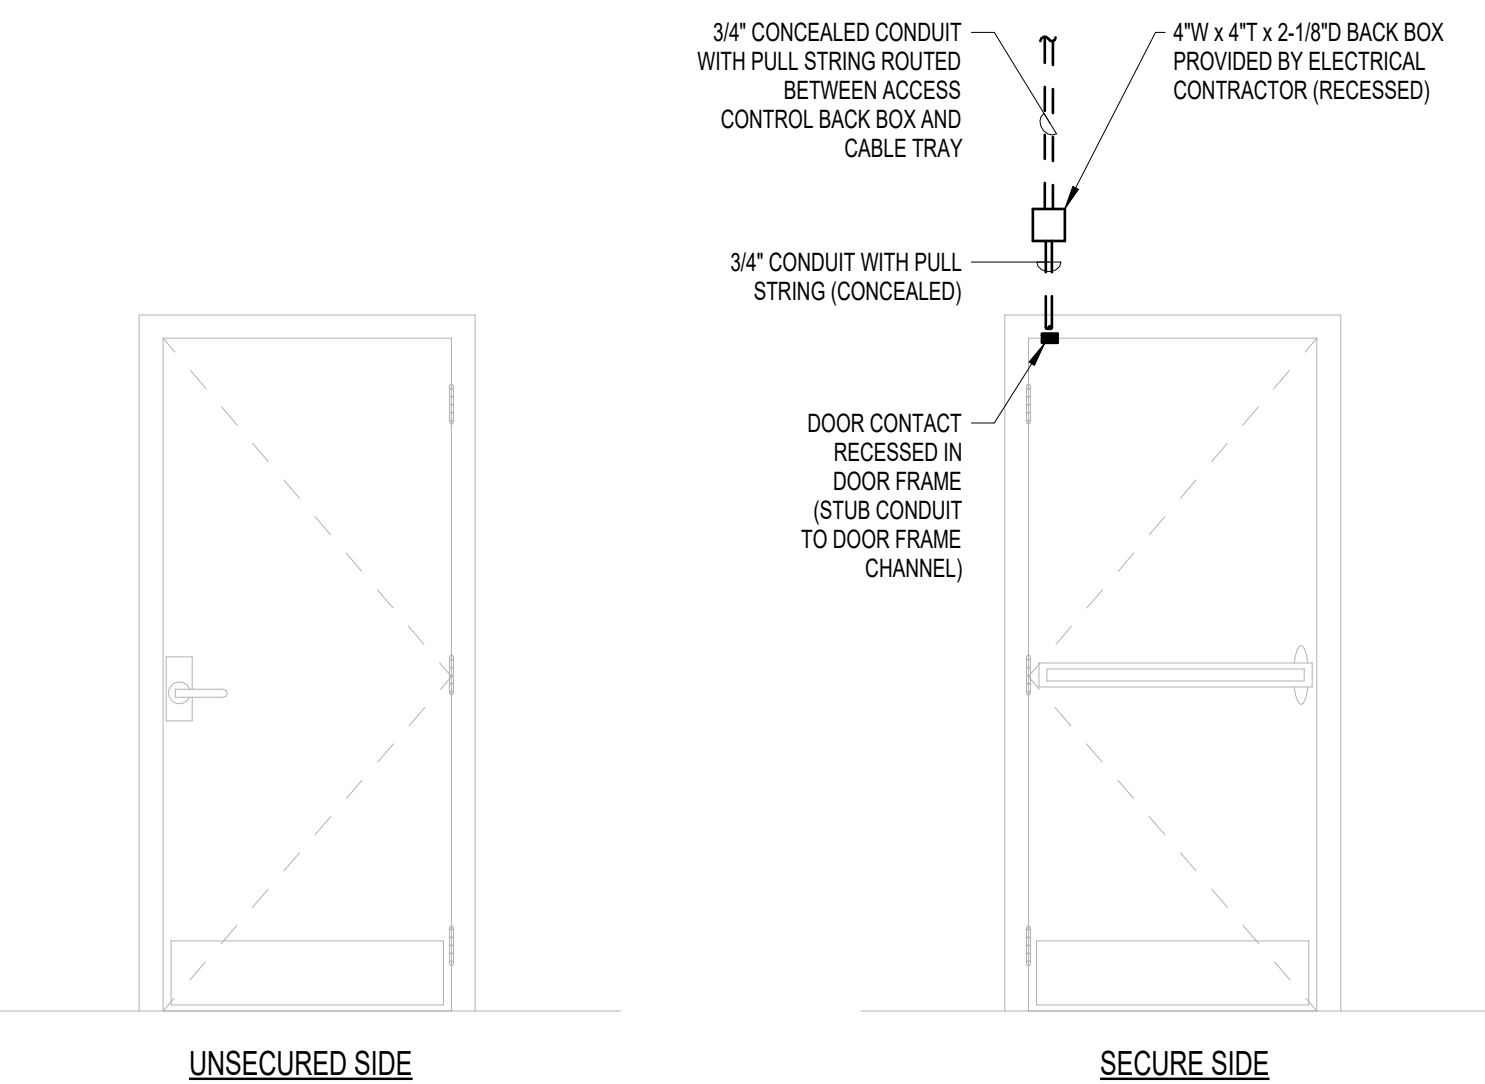

- NOTES:
1. ALL CONDUITS SHALL BE 3/4" UNLESS NOTED OTHERWISE.
 2. REFER TO FLOOR PLANS FOR EXACT DOOR SWING.
 3. REFER TO SHOP DRAWINGS FOR EXACT CONDUIT ROUGH-IN LOCATIONS.
 4. STUB CONDUIT INTO DOOR FRAME.
 5. PROVIDE PULL STRINGS IN ALL CONDUITS.

5 SINGLE DOOR WITH DOOR POSITION SWITCH

NTS

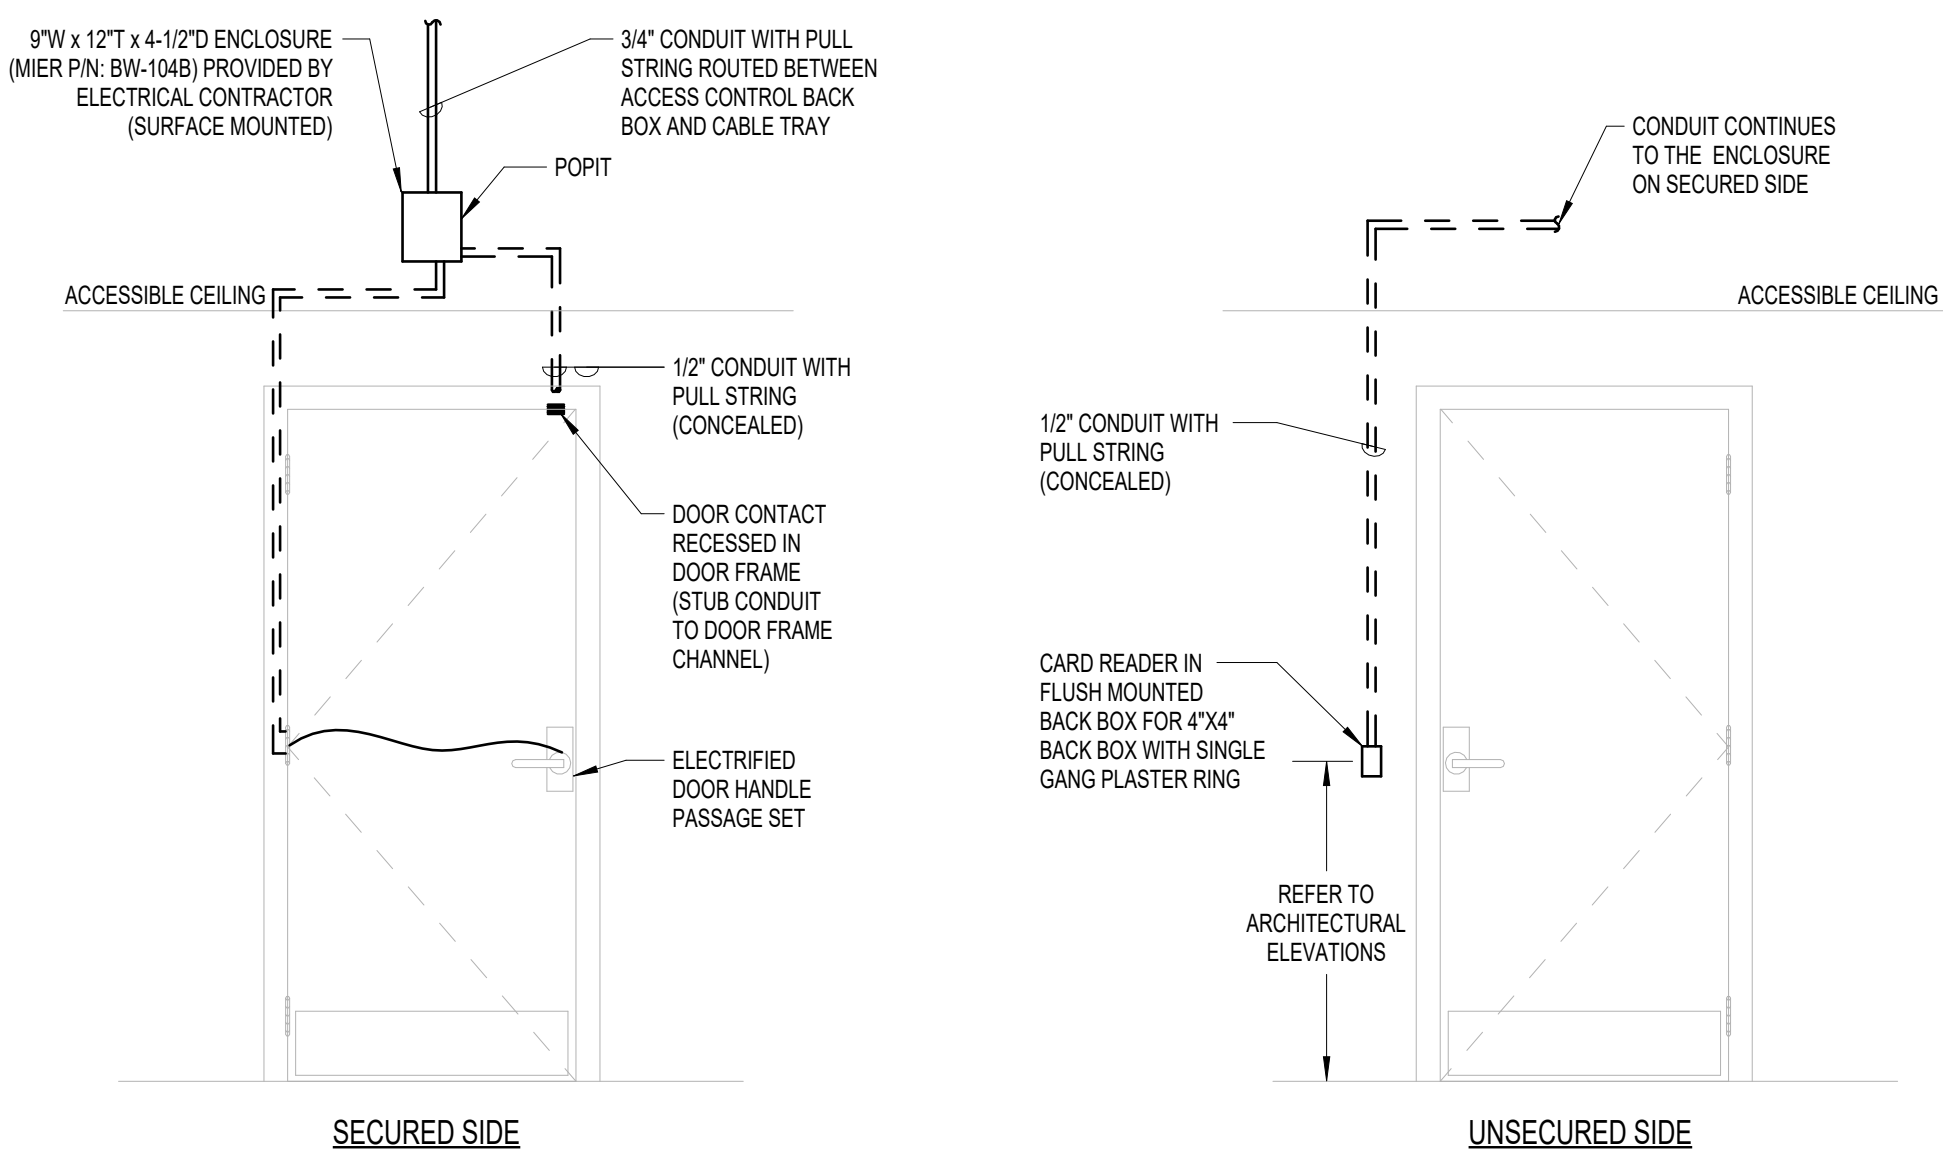

- NOTES:
1. ALL CONDUITS SHALL BE 3/4" UNLESS NOTED OTHERWISE.
 2. REFER TO FLOOR PLANS FOR EXACT DOOR SWING.
 3. REFER TO SHOP DRAWINGS FOR EXACT CONDUIT ROUGH-IN LOCATIONS.
 4. PROVIDE PULL STRINGS IN ALL CONDUITS.

1 SINGLE DOOR WITH CARD READER & ELECTRIC STRIKE

1/8" = 1'-0"