


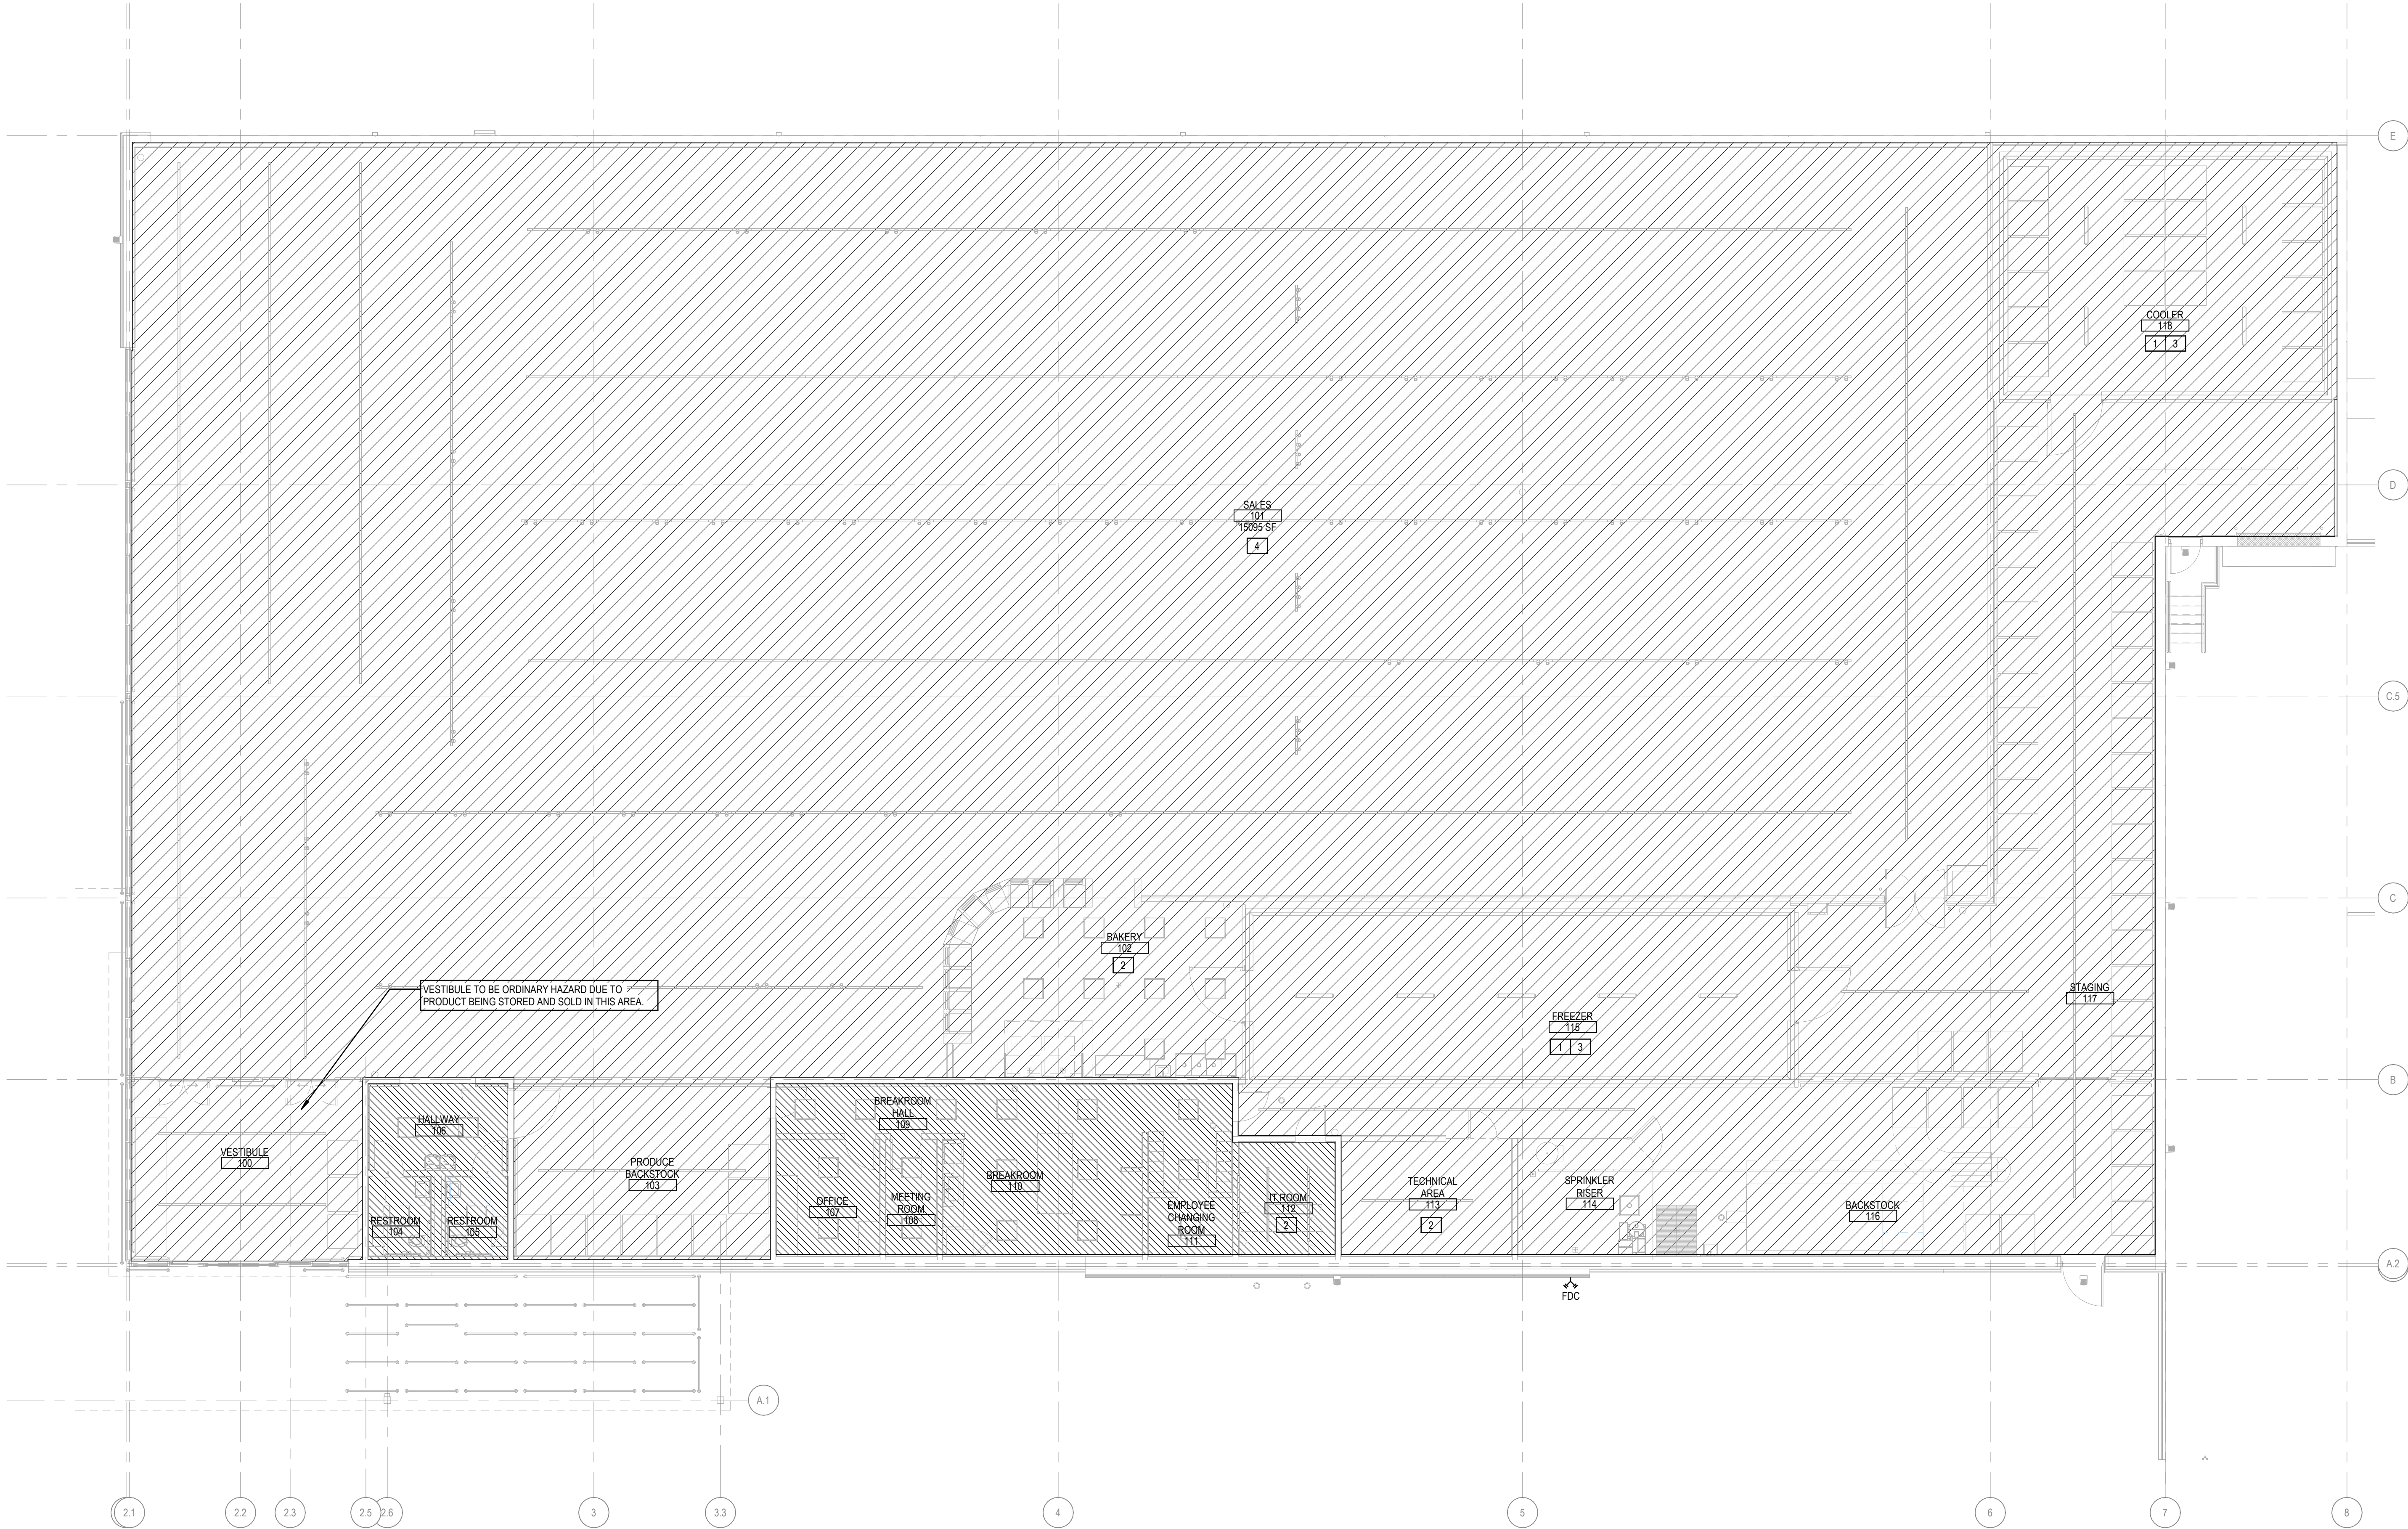

FIRE PROTECTION PLAN
1/8" = 1'-0"

FIRE PROTECTION KEYNOTES

1. PROVIDE ORDINARY DRY PENDENT SPRINKLERS IN COOLER/FREEZER CEILING AND UPRIGHT SPRINKLERS IN OPEN CEILING ABOVE.
2. PROVIDE HIGH TEMP SPRINKLER HEADS IN THE TECHNICAL ROOM, IT ROOM, AND ABOVE KITCHEN HOOD.
3. COORDINATE SPRINKLER PIPING WITH AGGREGATE BOXES' CLEARANCE. PROVIDE MINIMUM 4" CLEAR ABOVE AGGREGATE BOXES FOR INSTALL AND SERVICE. CONTACT MANUFACTURER FOR ADDITIONAL CLEARANCE INFORMATION.
4. FIRE PROTECTION PIPING WITHIN SALES AREA TO BE PAINTED WHITE.

DEFERRED SUBMISSION

THE FIRE PROTECTION DRAWINGS AND SPECIFICATIONS WITHIN THE PROGRESSIVE COMPANIES DOCUMENT SET ARE PERFORMANCE BASED AND INTENDED TO CONVEY SCOPE OF THE WORK. THE FIRE PROTECTION CONTRACTOR SHALL SUBMIT FOR REVIEW AND APPROVAL AS A DEFERRED SUBMITTAL TO THE LOCAL AHI SHOP DRAWINGS AND HYDRAULIC CALCULATIONS INDICATING THE SPRINKLER SYSTEM LAYOUT, INCLUDING FINAL HEAD LOCATIONS AND MAIN LEADER PIPING SIZING. THE FIRE PROTECTION CONTRACTOR SHALL PROVIDE THESE DOCUMENTS SEALED BY A LICENSED FIRE PROTECTION ENGINEER.

FIRE SPRINKLER DESIGN CRITERIA


CLASSIFICATION: **LIGHT HAZARD.**
DENSITY: 0.10 GPM/SQ. FT.
TYPICAL OPERATING AREA: 1,500 SQ. FT.
TYPICAL SPRINKLER SPACING: 225 SQ. FT. MAX.
TEMPERATURE RATING: 165°F.

CLASSIFICATION: **ORDINARY HAZARD.**
DENSITY: 0.15 GPM/SQ. FT.
TYPICAL OPERATING AREA: 1,500 SQ. FT.
TYPICAL SPRINKLER SPACING: 130 SQ. FT. MAX.
TEMPERATURE RATING: 165°F.


CLASSIFICATION: **GROUP 1 EXTRA HAZARD.**
DENSITY: 0.30 GPM/SQ. FT.
TYPICAL OPERATING AREA: 2300 SQ. FT.
TEMPERATURE RATING: 165°F.

GENERAL INSTALLATION NOTES:

1. THE AWARDED FPC SHALL BE RESPONSIBLE TO ORDER A NEW WATER FLOW TEST IF EXISTING DATA TAKEN WITHIN THE LAST YEAR IS NOT AVAILABLE.
2. DESIGN CALCULATIONS FOR NEW SPRINKLERS SHALL ALLOW FOR 10 PERCENT SAFETY FACTOR.
3. EXISTING FIRE DEPARTMENT CONNECTIONS AND HOSE REELS SHALL REMAIN.
4. CLASSIFICATION PERTAINS TO BOTH NEW ADDITIONS AND REMODEL AREAS.

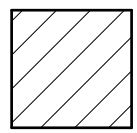

FIRE PROTECTION SCOPE - ORDINARY HAZARD

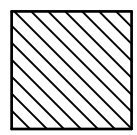

FIRE PROTECTION SCOPE - LIGHT HAZARD

LIDL US, LLC

LIDL 1517 NORCROSS, GA

ISSUANCE
11/07/2025 PERMIT CYCLE 1

PROJECT NUMBER
7955191
PROJECT MANAGER
A. HENGSTEBECK
PROFESSIONAL
M. GROSE
DRAWN BY
T. SMITH
CHECKED BY
B. KOOMAN

FIRE PROTECTION PLAN
FP101




5/20/2025 10:05 PM Autodesk Docs/79550191 - LIDL 1517 Norcross, GA - MECH-4


5/20/2025 10:05 PM

5/20/2025 10:05 PM


THIS DOCUMENT AND ANY INFORMATION CONTAINED HEREIN ARE THE PROPERTY OF PROGRESSIVE COMPANIES ENGINEERING & PLANNING, LLC. NO PART OF THIS DOCUMENT MAY BE REPRODUCED OR TRANSMITTED IN ANY FORM OR BY ANY MEANS, ELECTRONIC OR MECHANICAL, WITHOUT PERMISSION IN WRITING FROM PROGRESSIVE COMPANIES ENGINEERING & PLANNING, LLC. AN INSTRUMENT OF SERVICE AND PROFESSIONAL ARCHITECTURE. OTHER RESERVED RIGHTS INCLUDING THE COPYRIGHT THEREIN.

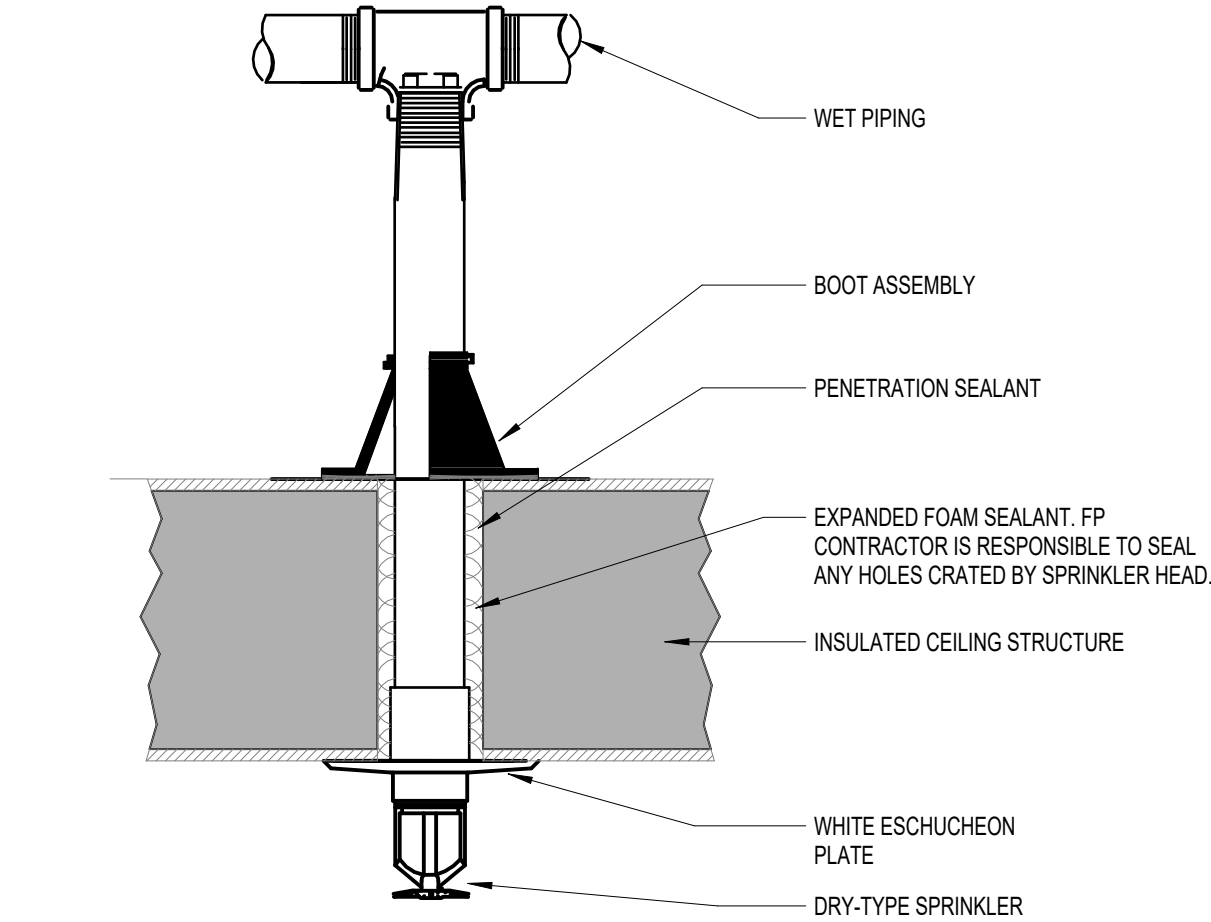


E5 DRY-TYPE SPRINKLER INSTALLATION
NOT TO SCALE

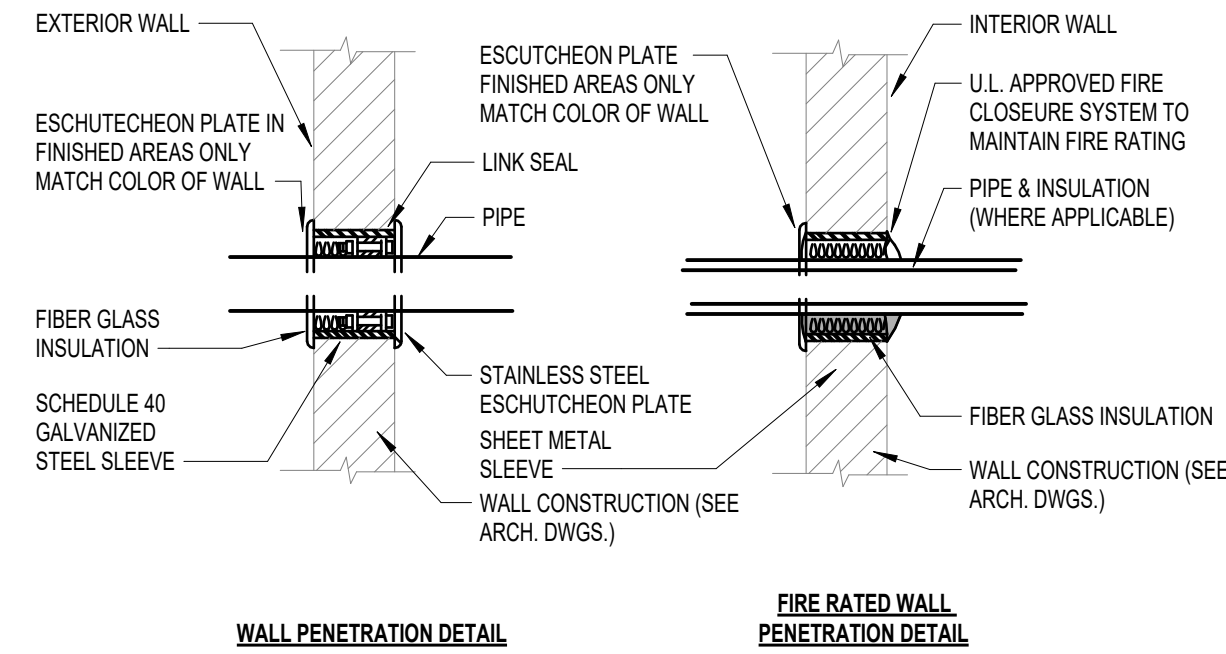

E3 WALL PENETRATION
NOT TO SCALE

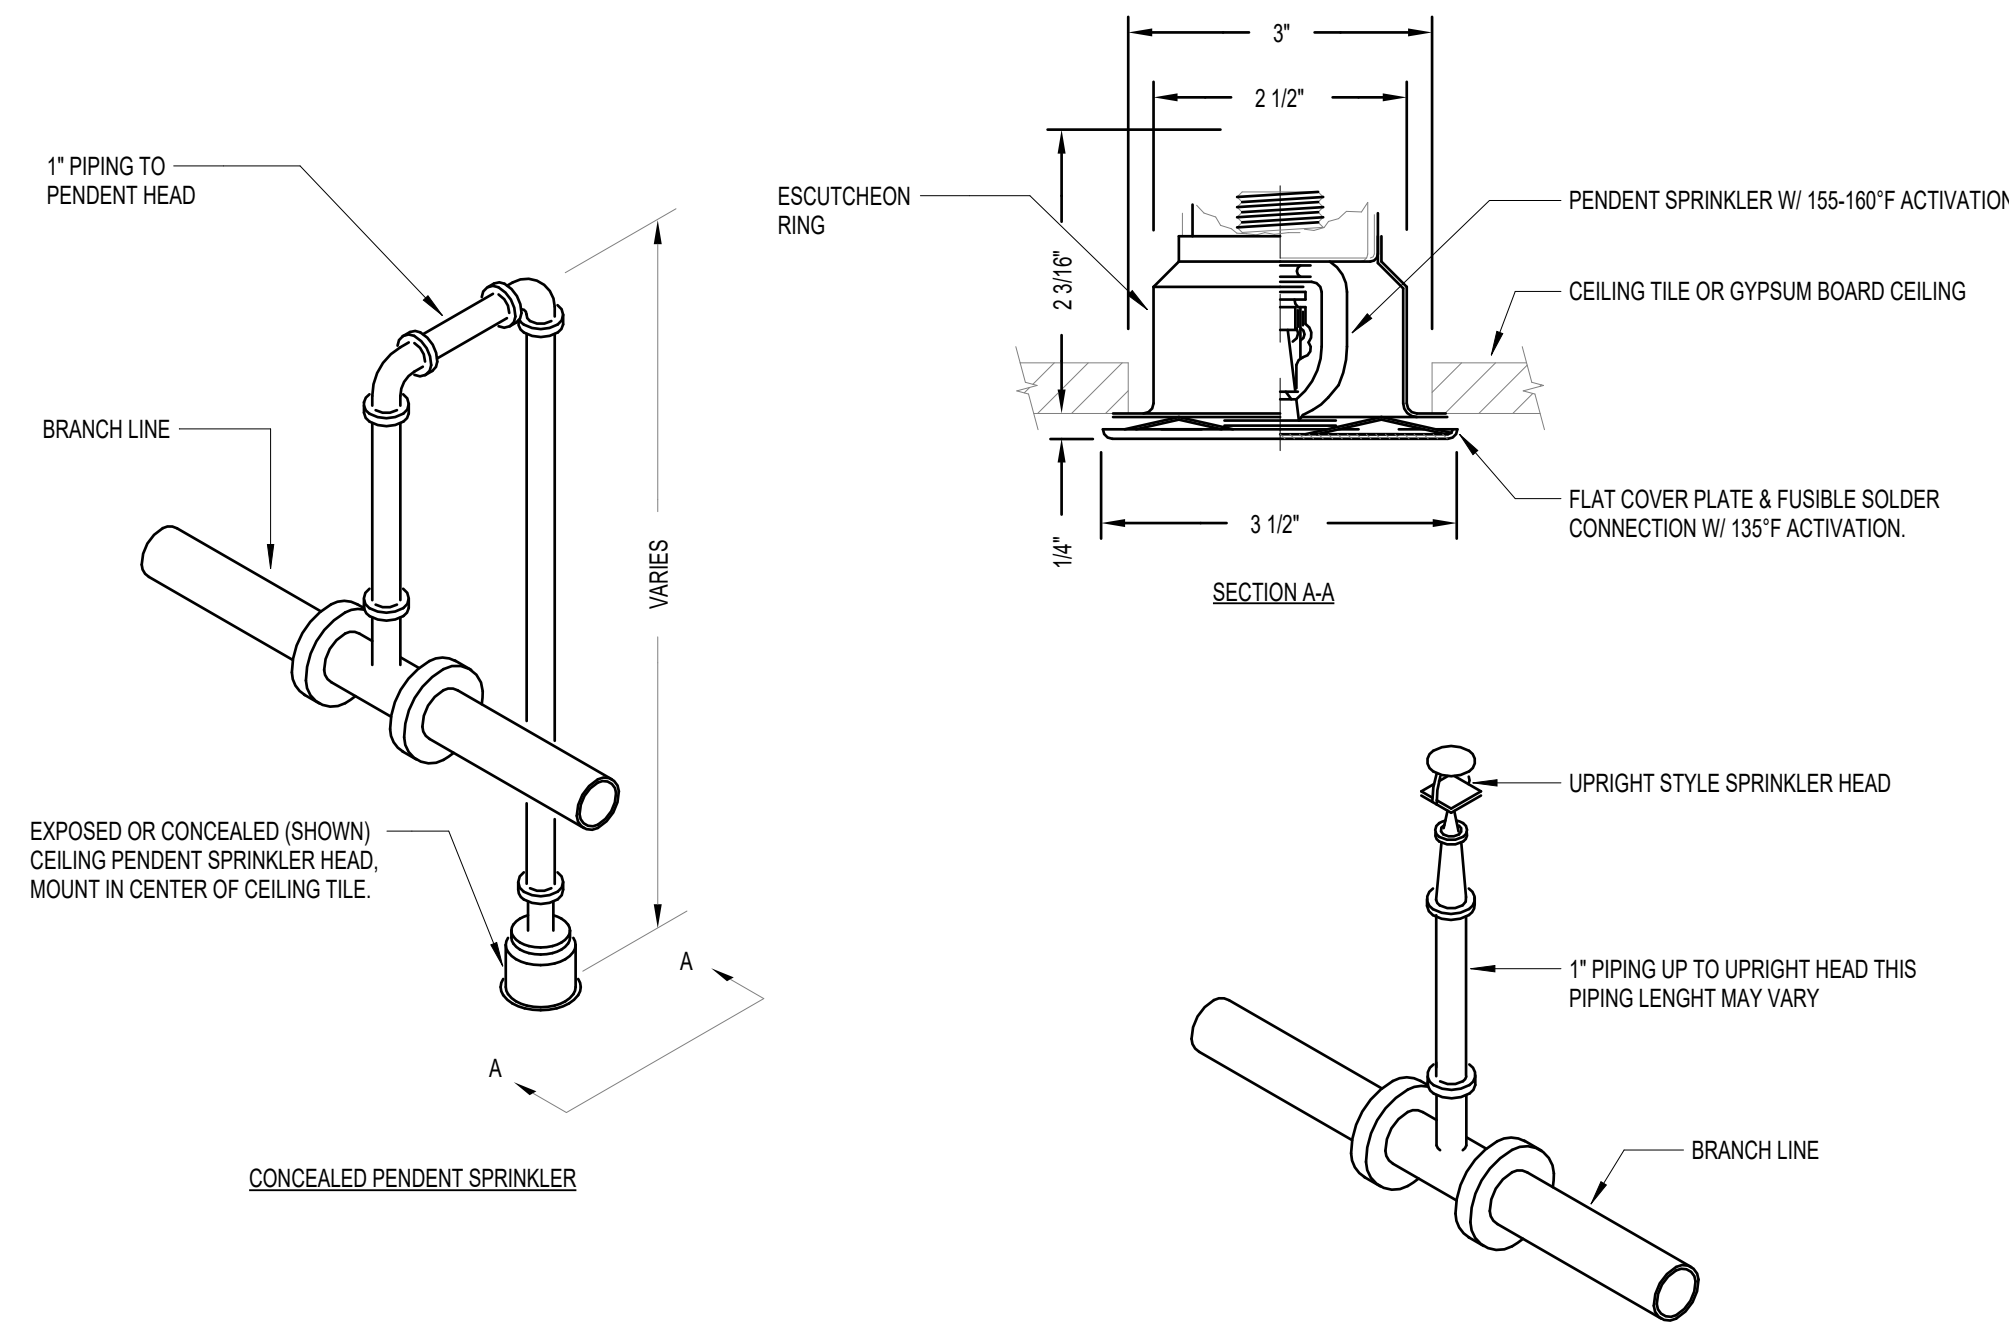

E2 CONCEALED SPRINKLER ARM OVER AND UPRIGHT SPRINKLER
NOT TO SCALE

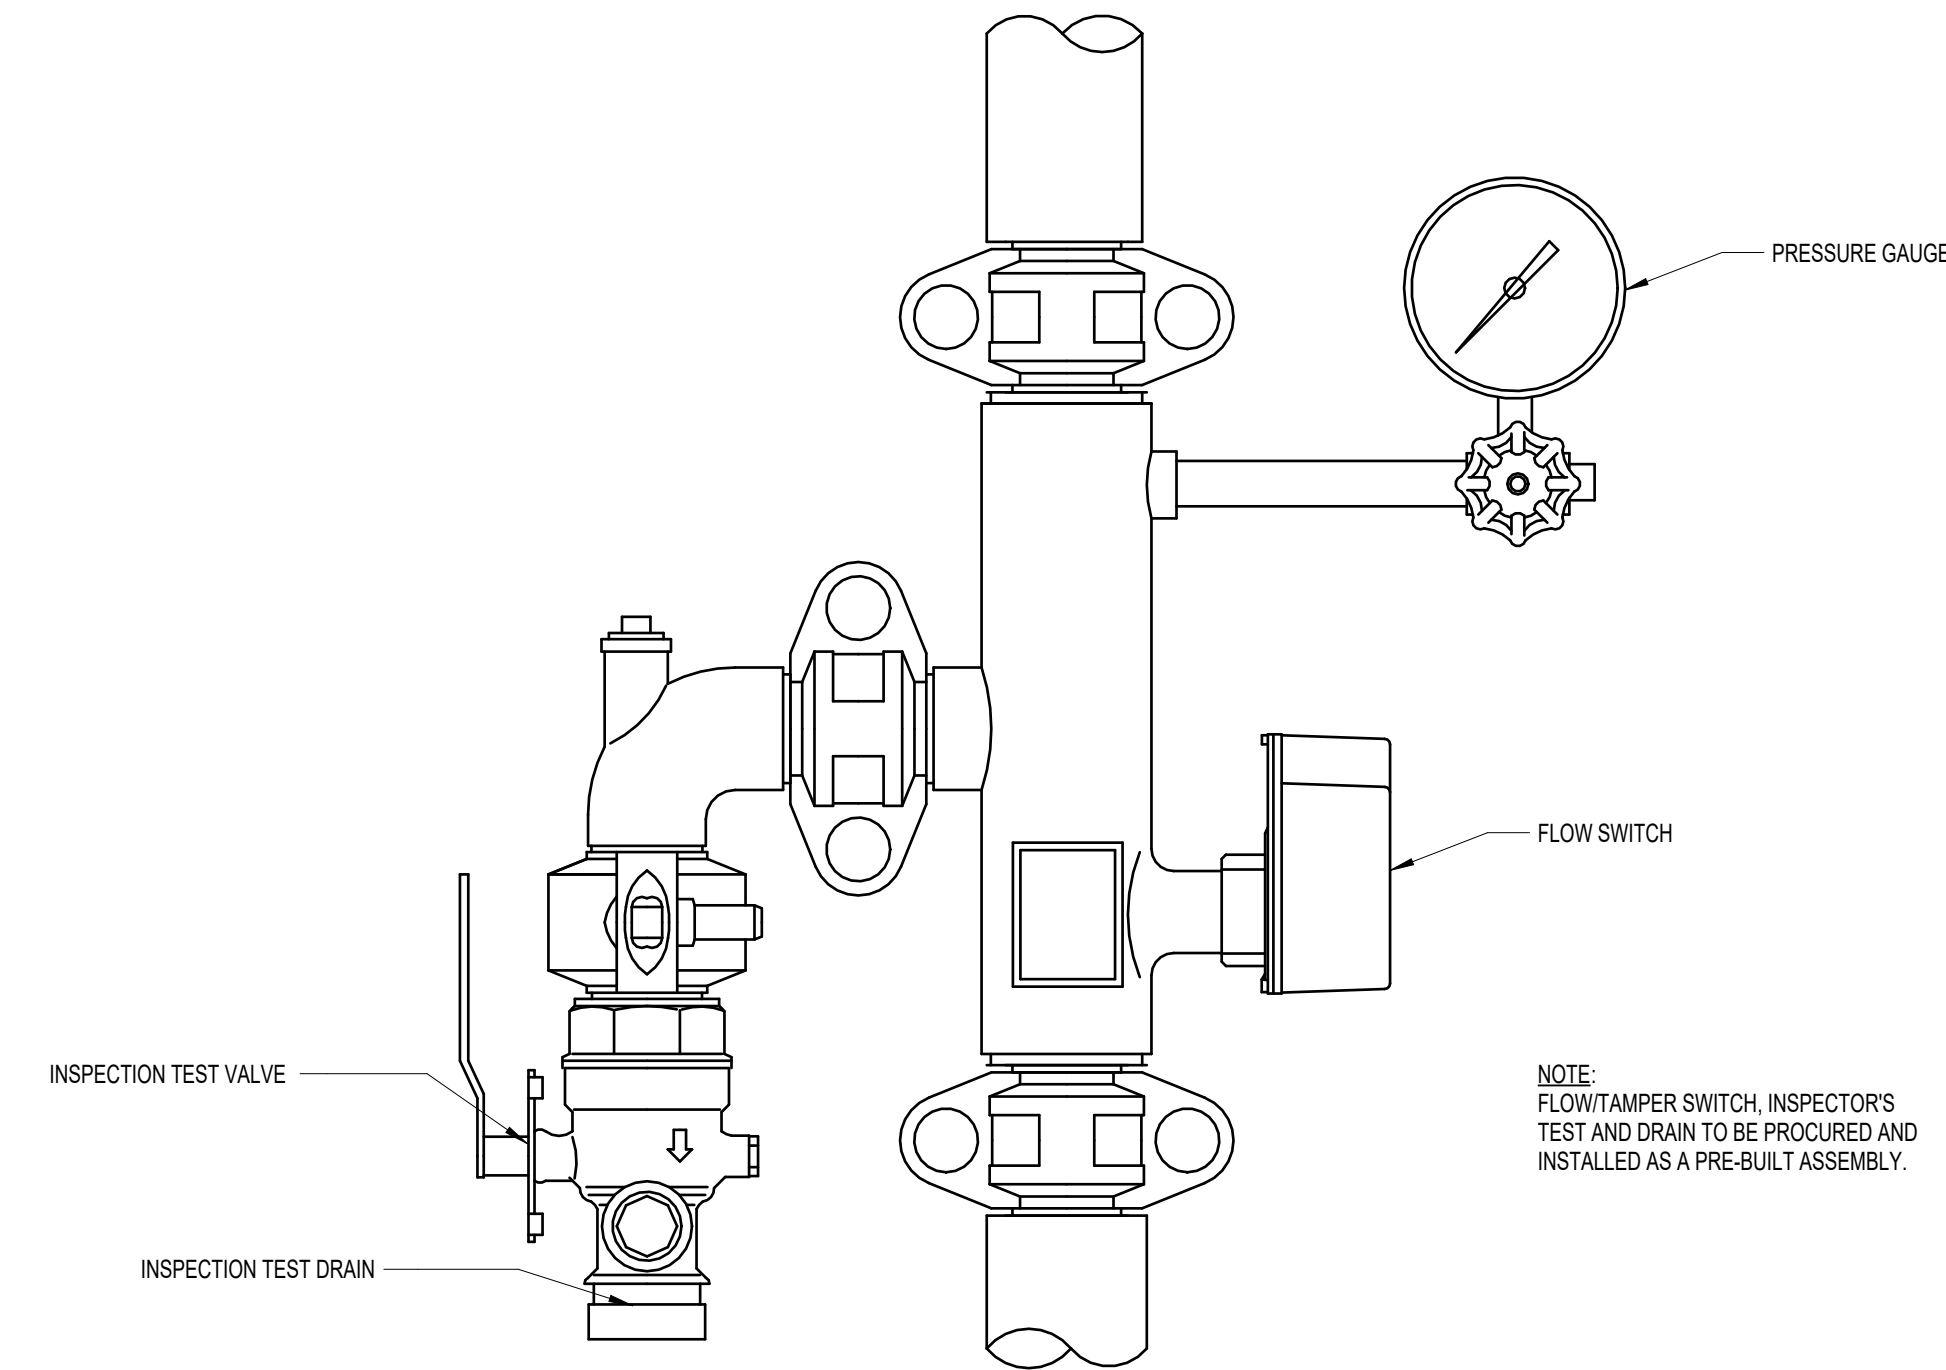

C2 INSPECTORS TEST AND FLOW SWITCH ASSEMBLY
NOT TO SCALE

DEFERRED SUBMISSION

THE FIRE PROTECTION DRAWINGS AND SPECIFICATIONS WITHIN THE PROGRESSIVE COMPANIES DOCUMENT SET ARE PERFORMANCE BASED AND INTENDED TO CONVEY SCOPE OF THE WORK. THE FIRE PROTECTION CONTRACTOR SHALL SUBMIT FOR REVIEW AND APPROVAL AS A DEFERRED SUBMITTAL TO THE LOCAL AHJ SHOP DRAWINGS AND HYDRAULIC CALCULATIONS INDICATING THE SPRINKLER SYSTEM LAYOUT, INCLUDING FINAL HEAD LOCATIONS AND MAIN LEADER PIPING SIZING. THE FIRE PROTECTION CONTRACTOR SHALL PROVIDE THESE DOCUMENTS SEALED BY A LICENSED FIRE PROTECTION ENGINEER.

ISSUANCE
11/07/2025 PERMIT CYCLE 1

PROJECT NUMBER
79550191
PROJECT MANAGER
A. HENGSTEBECK
PROFESSIONAL
M. GROSE
DRAWN BY
T. SMITH
CHECKED BY
B. KOOMAN

FIRE PROTECTION DETAILS
FP600

LIDL US, LLC
LIDL 1517 NORCROSS, GA

499 JIMMY CARTER BLVD NORCROSS, GA 30993



PROGRESSIVE ARCHITECTURE ENGINEERING & PLANNING, LLC
PROGRESSIVE COMPANIES
Charlotte, NC | Detroit, MI | Grand Rapids, MI
weareprogressive.com