


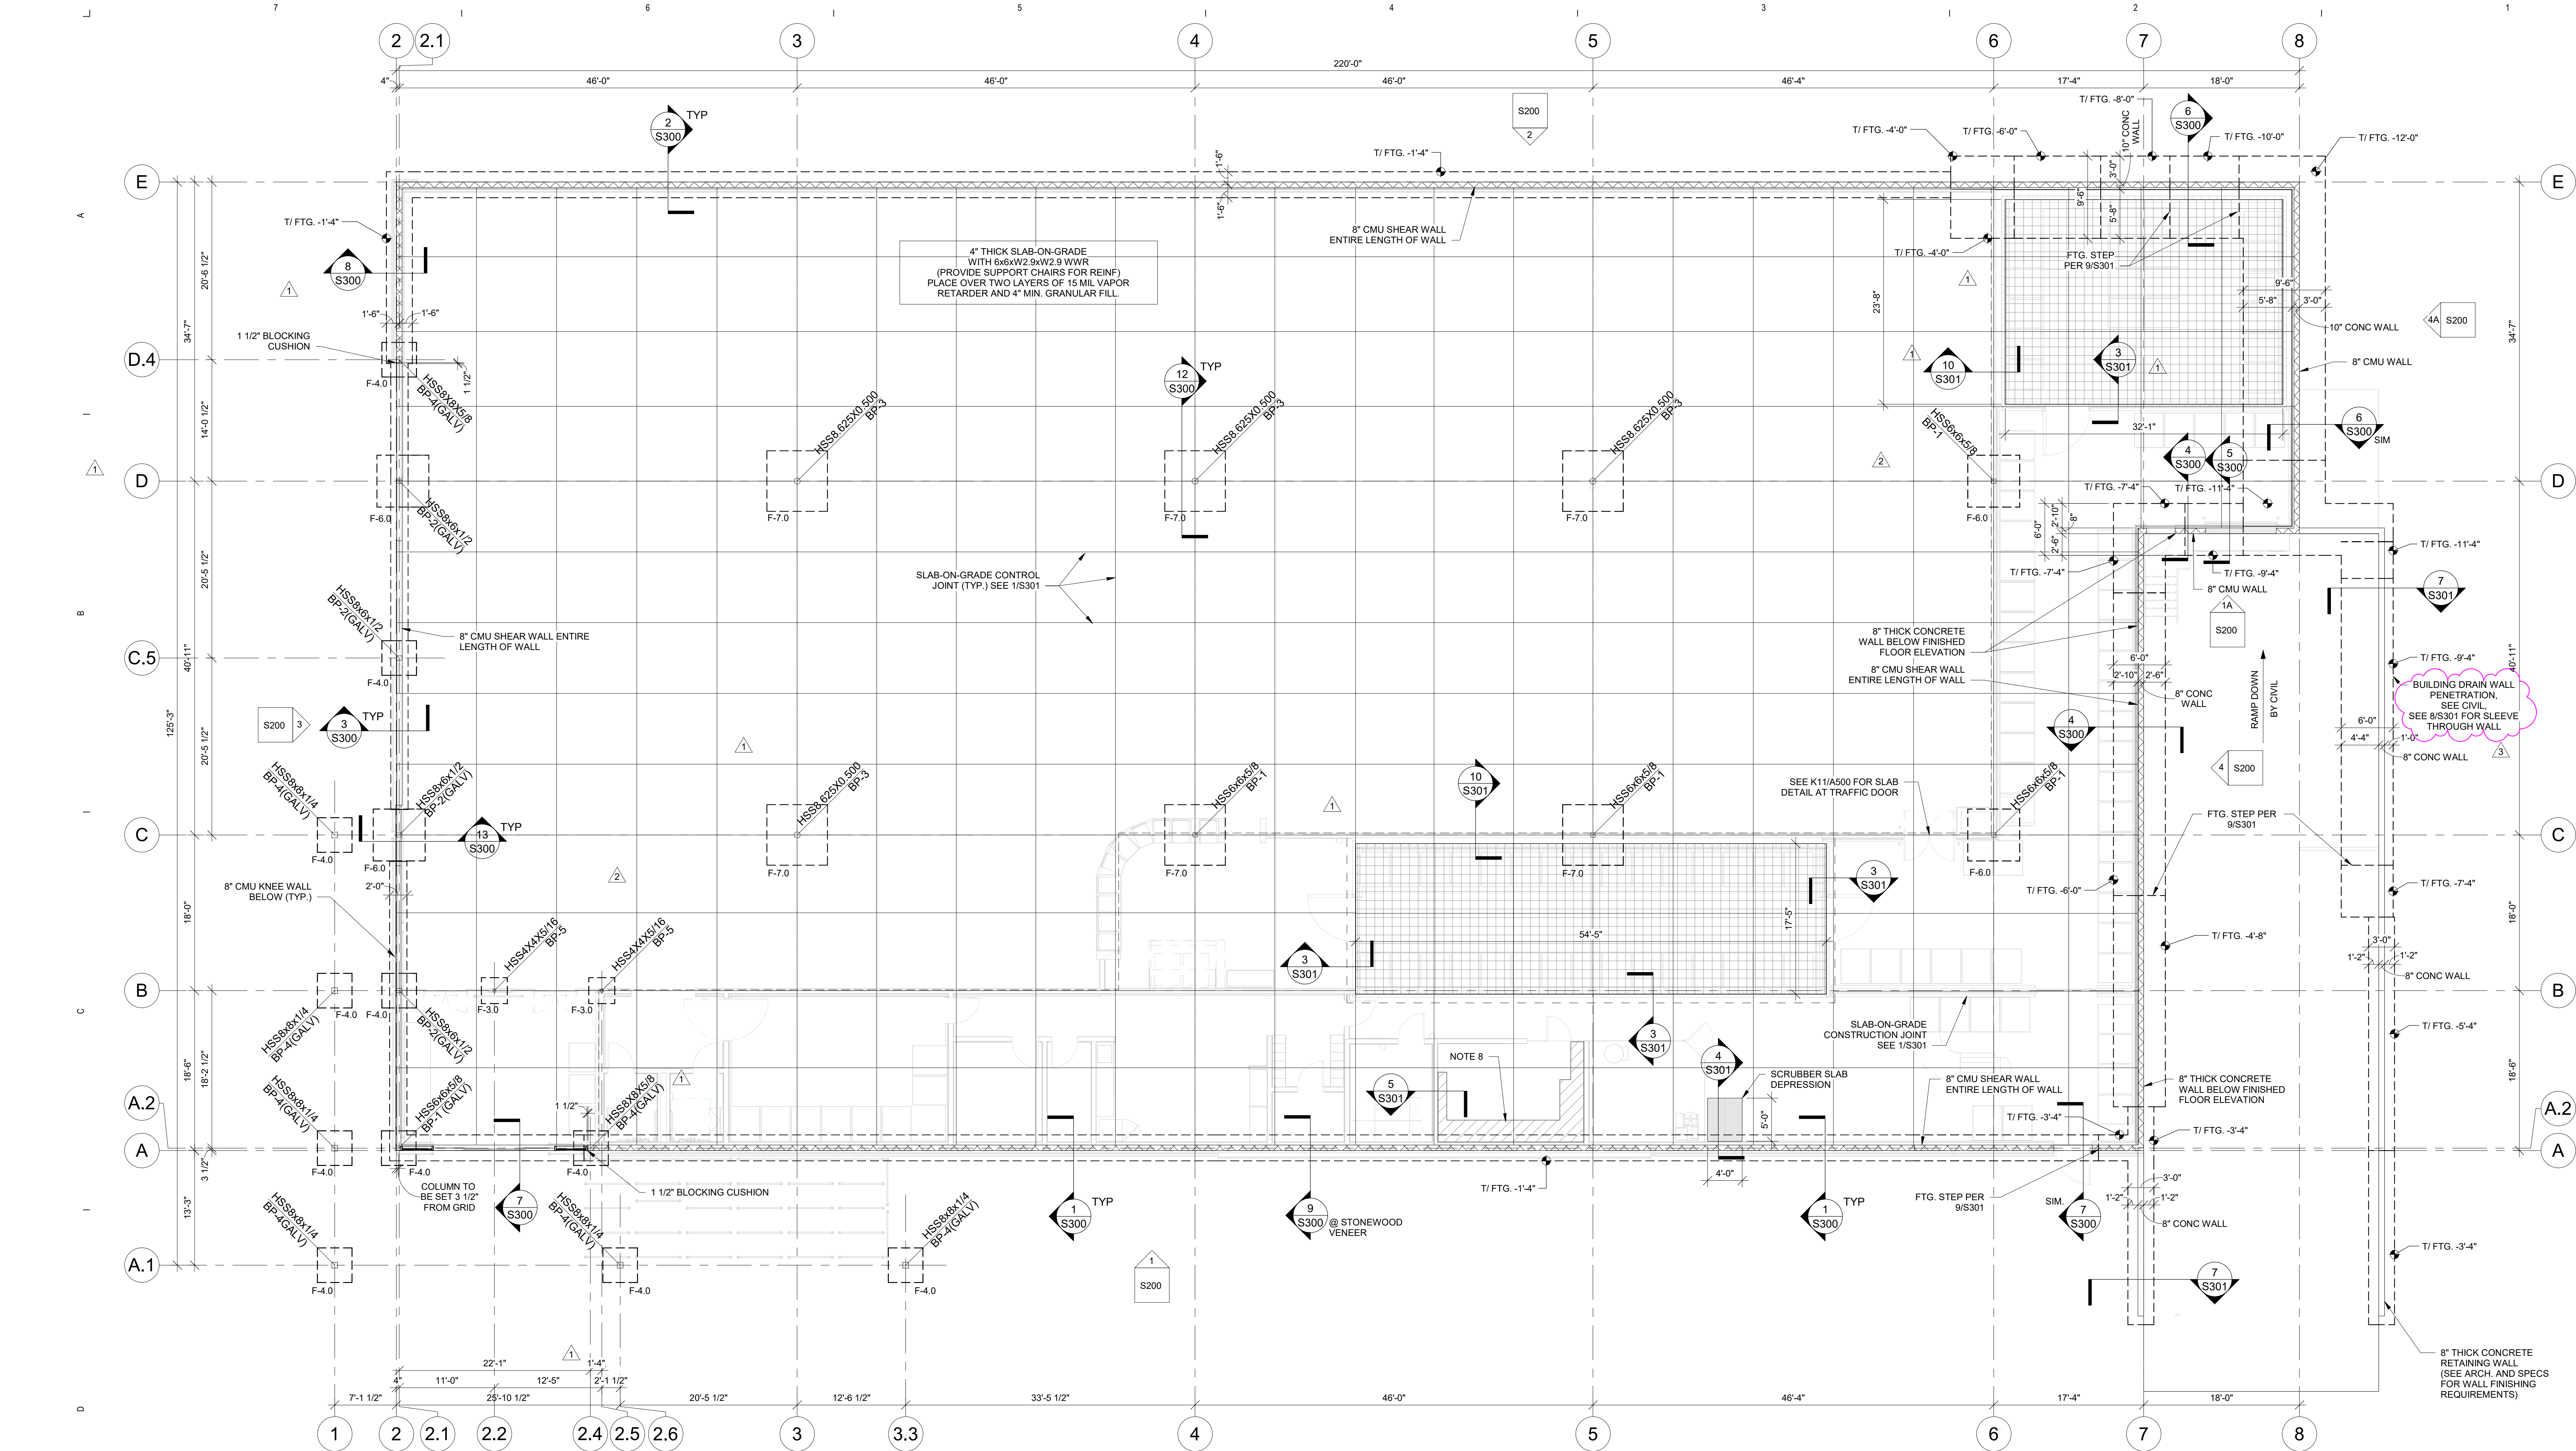


GROUND FLOOR AND FOUNDATION PLAN

1/8" = 1'-0"

PLAN NOTES - FOUNDATIONS

- 1) TOP OF SLAB-ON-GRADE ELEVATION = 0'-0" U.N.O. (CORRESPONDS TO SITE ELEVATION 1030.00').
- 2) ELEVATIONS INDICATED (±X'-X") ARE RELATIVE TO 0'-0".
- 3) TOP OF INTERIOR FOOTING ELEVATION = (-1'-4") U.N.O.
- 4) TOP OF EXTERIOR COLUMN FOOTING ELEVATION = (-1'-4") U.N.O. EXTERIOR FOOTINGS TO BEAR 2'-6" MIN. BELOW GRADE.
- 5) TOP OF EXTERIOR WALL FOOTING ELEVATION = (-1'-4") U.N.O. EXTERIOR FOOTINGS TO BEAR 2'-6" MIN. BELOW GRADE.
- 6) ALL PIERS, COLUMNS, AND FOOTINGS SHALL BE CENTERED ON GRID LINES U.N.O.
- 7) SEE ARCHITECTURAL DRAWING A104 FOR SLAB POUR SEQUENCE DIAGRAM.
- 8) 3 1/2" THICK CONCRETE HOUSEKEEPING PAD BENEATH ELECTRICAL EQUIPMENT. SEE S/S301. COORDINATE ALL PAD DIMENSIONS WITH SIZE AND LOCATION OF ACTUAL EQUIPMENT PURCHASED.
- 9) SEE S200 FOR STRUCTURAL ELEVATIONS AND CMU WALL REINFORCING.
- 10) SEE S001 FOR GENERAL NOTES.
- 11) SEE S300-S301 FOR TYPICAL FOUNDATION DETAILS.
- 12) KEY:

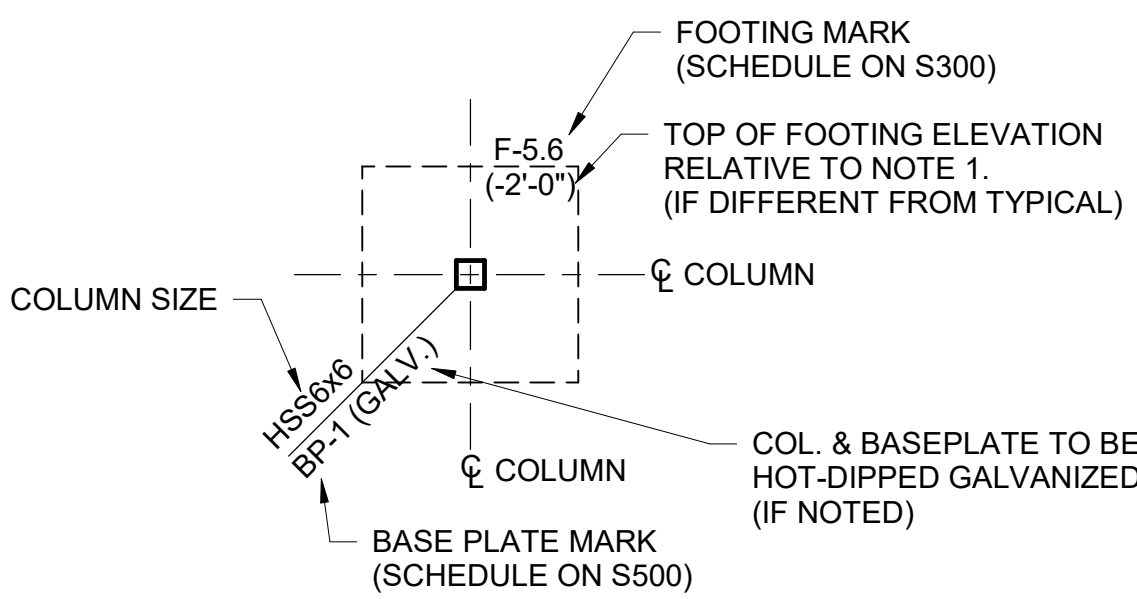

5/20/2025 1:58:44 PM Autodesk Docs/2025/02/02, Lidl Norcross, GA/2025/02/02, LIDL NorcrossGA, STR, 0251.vst
2025/02/02 LIDL NORCROSS AND FOUNDATION PLAN

THIS DOCUMENT AND ANY INFORMATION CONTAINED HEREIN ARE THE PROPERTY OF DEVITA INC. AND ARE NOT TO BE REPRODUCED OR TRANSMITTED IN ANY FORM OR BY ANY MEANS, ELECTRONIC OR MECHANICAL, INCLUDING PHOTOCOPYING, RECORDING, OR BY ANY INFORMATION STORAGE AND RETRIEVAL SYSTEM, WITHOUT THE WRITTEN PERMISSION OF DEVITA INC. © 2025 DEVITA INC. ALL RIGHTS RESERVED.

DEVITA
Engineering Great Ideas
ATLANTA | CHARLOTTE | HUNTSVILLE | KNOXVILLE
www.devitainc.com
877.4.DEVITA
corp@devita-inc.com
Devita & Associates, Inc. Project: 25126-02
Drawn By: SAG Checked By: MLH

PROJECT NUMBER
79650191
PROJECT MANAGER
S. CHOYAN
PROFESSIONAL
RL
DRAWN BY
SAG
CHECKED BY
MLH

GROUND FLOOR
AND
FOUNDATION
PLAN
S101

PROGRESSIVE
COMPANIES
Charlotte, NC | Detroit, MI | Grand Rapids, MI
weareprogressive.com




LIDL US, LLC
LIDL P1517 NORCROSS, GA

499 JIMMY CARTER BLVD. NORCROSS, GA 30093

If this document is sealed and signed in a digital or electronic format and is received from someone other than the sealing professional identified in the document, you must contact the sealing professional in writing to validate authenticity of the document. The sealing professional disavows the seal and signature and shall not be liable for any liability associated with it where the authenticity of any digital or electronic seal or signature has not been validated in this manner.

ISSUANCE



10/16/2025	100% QA/QC
11/07/2025	PERMIT CYCLE 1
12/16/2025	PERMIT CYCLE 2
01/14/2026	PERMIT CYCLE 3
05/28/2026	CCD 01

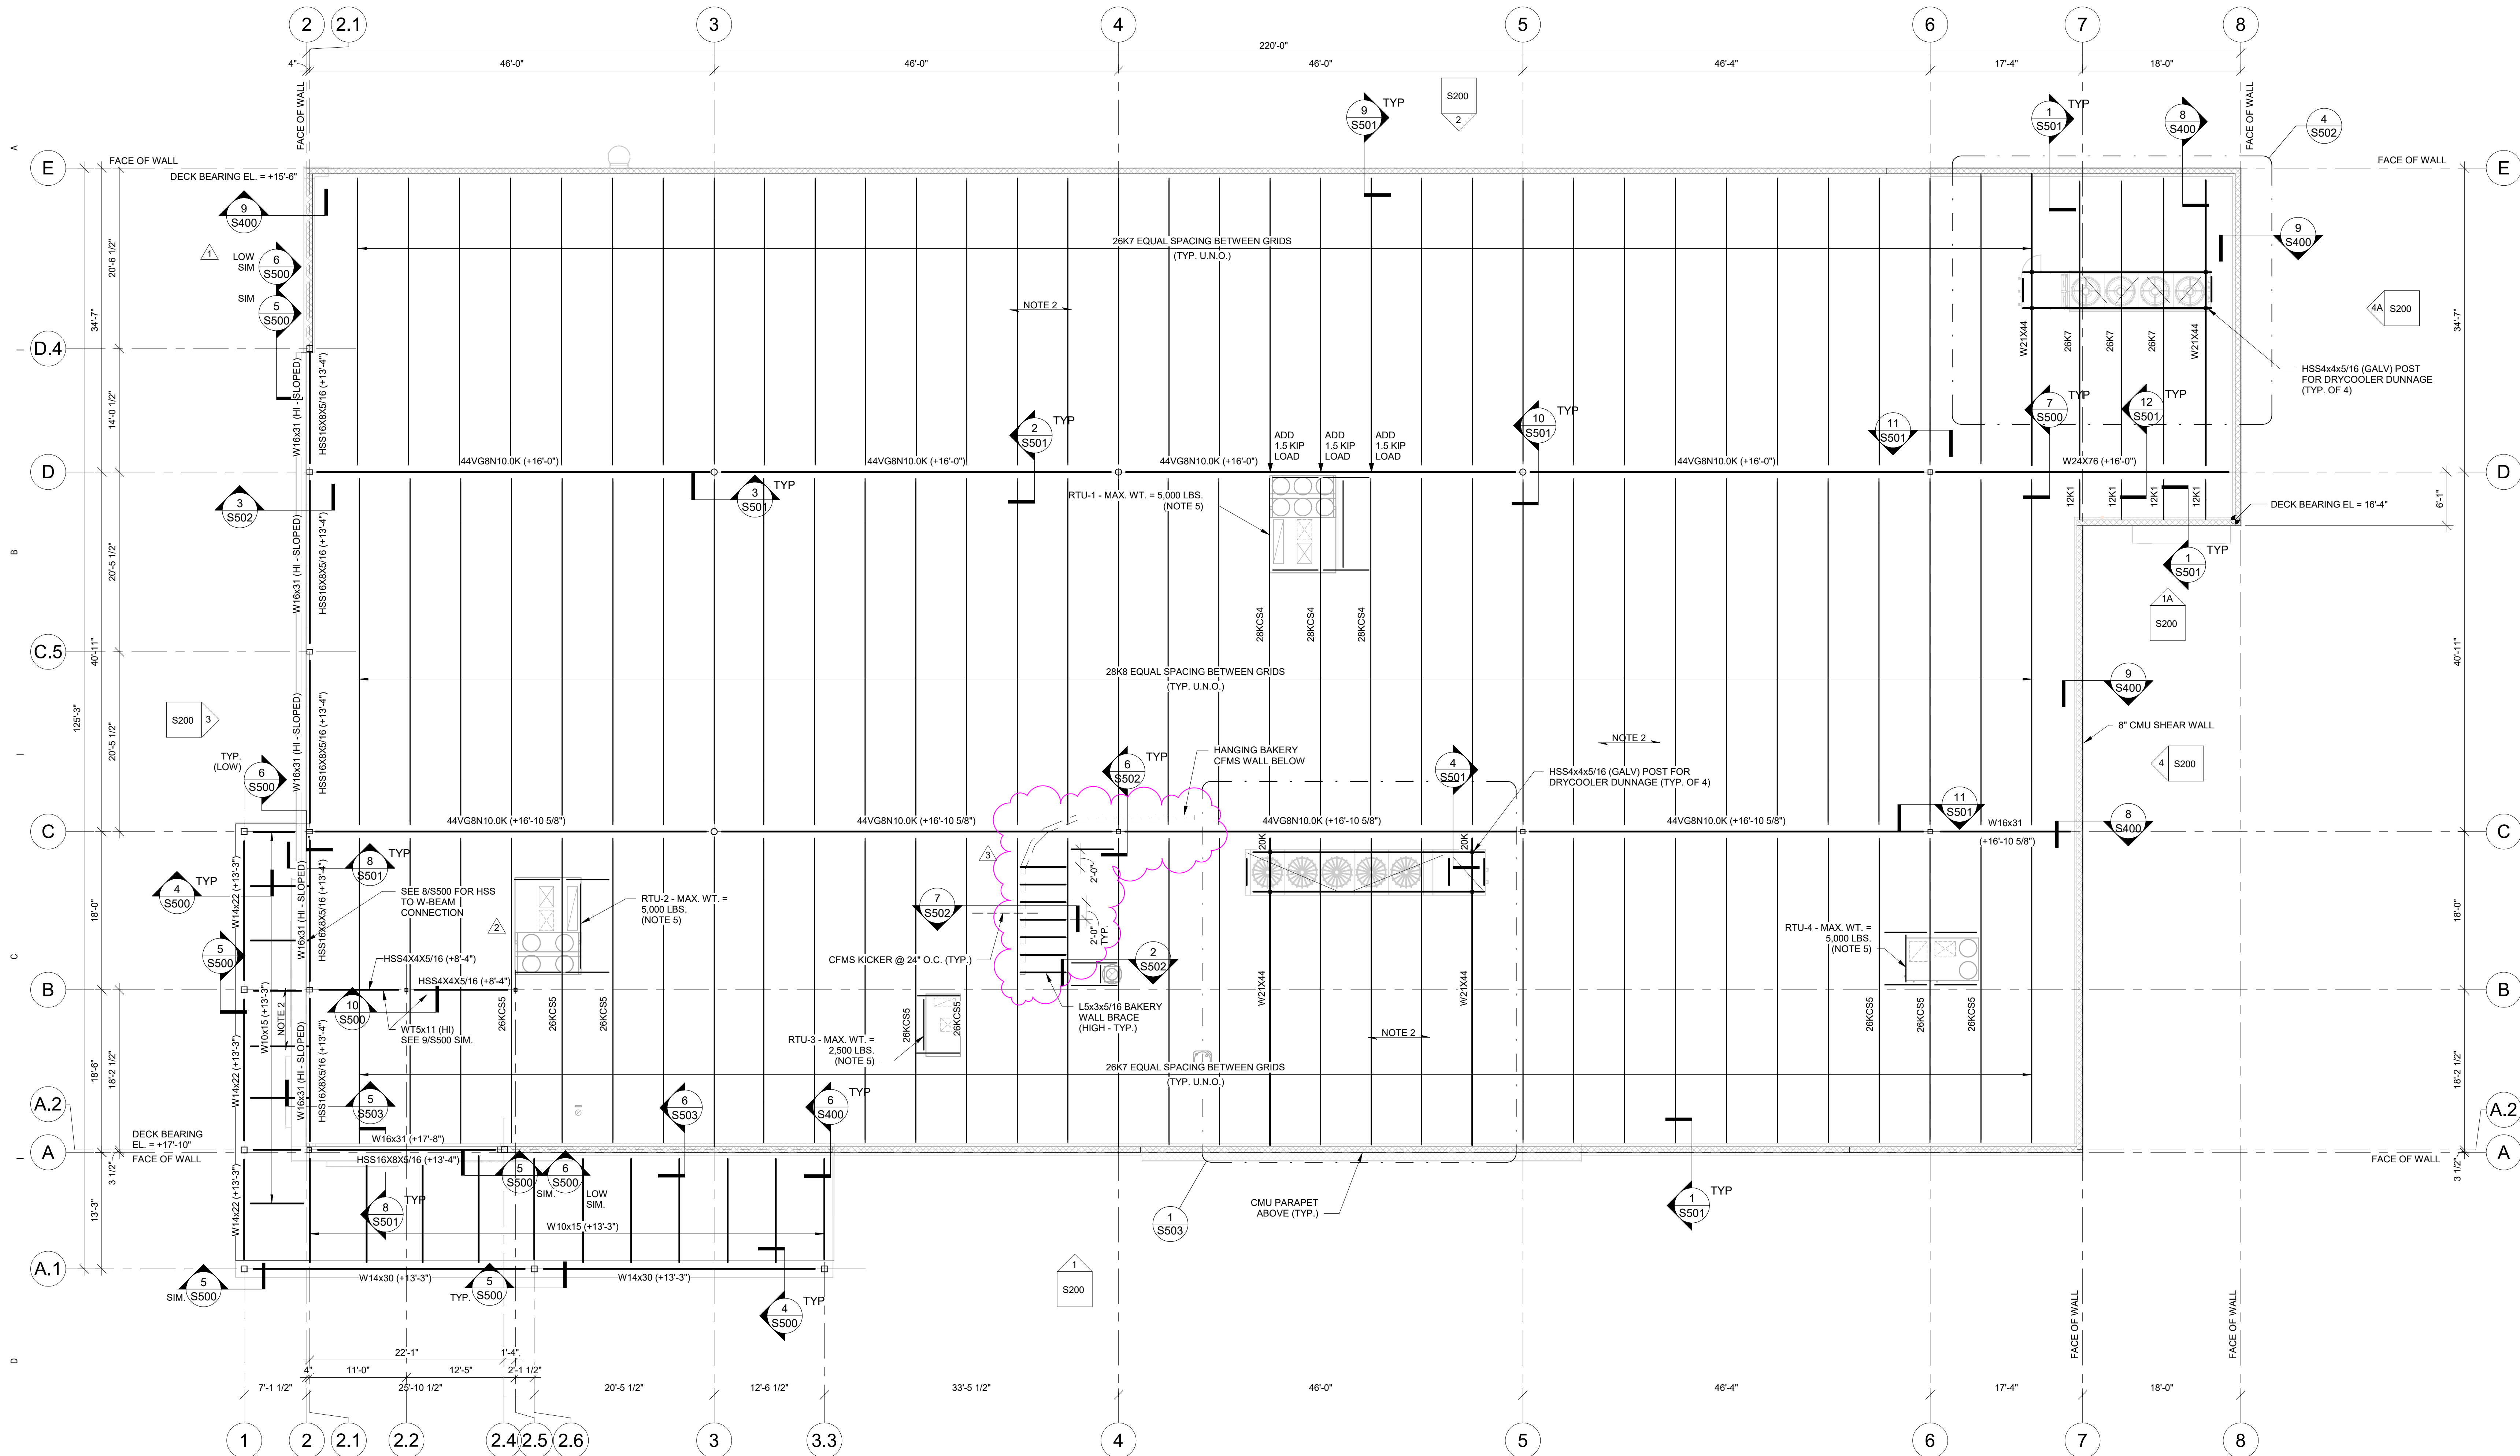

ROOF FRAMING PLAN

PLAN NOTES

- 1) ELEVATIONS INDICATED (+X'-X") ARE TOP OF STEEL ELEVATIONS (U.N.O.) AND ARE RELATIVE TO TOP OF SLAB-ON-GRADE ELEVATION (0'-0").
- 2) 1/2" DEEP, 20 GAUGE ROOF DECK WITH 5/8" Ø PUDDLE WELDS IN 36/5 PATTERN AT ALL SUPPORTS AND 1 1/2" #10 TEK SCREWS @ 8" O.C. ALL SIDELAPS.
- 3) ALL BEAMS AND JOISTS ARE SPACED EVENLY BETWEEN COLUMN LINES U.N.O. AT MAX. SPACING OR 6" O.C.
- 4) COORDINATE SIZE AND LOCATION OF ALL OPENINGS WITH ARCHITECTURAL AND MEP DRAWINGS, AND ALL REQUIREMENTS OF ACTUAL EQUIPMENT PURCHASED.
- 5) PROVIDE DECK SUPPORT FRAMING AT RTU CURBS PER 2/S502 AND JOIST REINFORCING PER 1/S502.
- 7) JOIST GIRDER DESIGNATION REFLECTS TYPICAL COMBINED REACTIONS FROM SUPPORTED JOISTS AND STEEL BEAMS U.N.O. ON PLAN. JOIST DESIGNER SHALL DESIGN JOIST GIRDER FOR THE REACTIONS AT ALL PANEL POINT LOCATIONS WHERE INDICATED SEPARATELY ON THE PLAN. THE REACTIONS INDICATED ON THESE DRAWINGS DO NOT INCLUDE THE LOAD DUE TO THE JOIST GIRDER SELF WEIGHTS.
- 8) SEE S001 FOR GENERAL NOTES.
- 9) SEE S400 THRU S502 FOR TYPICAL DETAILS.
- 10) MECHANICAL DUCTWORK AT THIS LOCATION TO PASS THROUGH JOIST GIRDERS AT GRID B AND C. G.C. AND MEP ENGINEER TO COORDINATE SIZE AND LOCATIONS OF DUCTWORK WITH LOCATIONS OF JOIST GIRDER WEB MEMBERS.
- 11) SPRINKLER LINE AT THIS LOCATION TO PASS THROUGH JOIST GIRDERS AT GRID B AND C. G.C. AND MEP ENGINEER TO COORDINATE LOCATION AND ELEVATION OF SPRINKLER LINE WITH LOCATIONS OF JOIST GIRDER WEB MEMBERS.
- 12) STEEL FRAMING KEY.

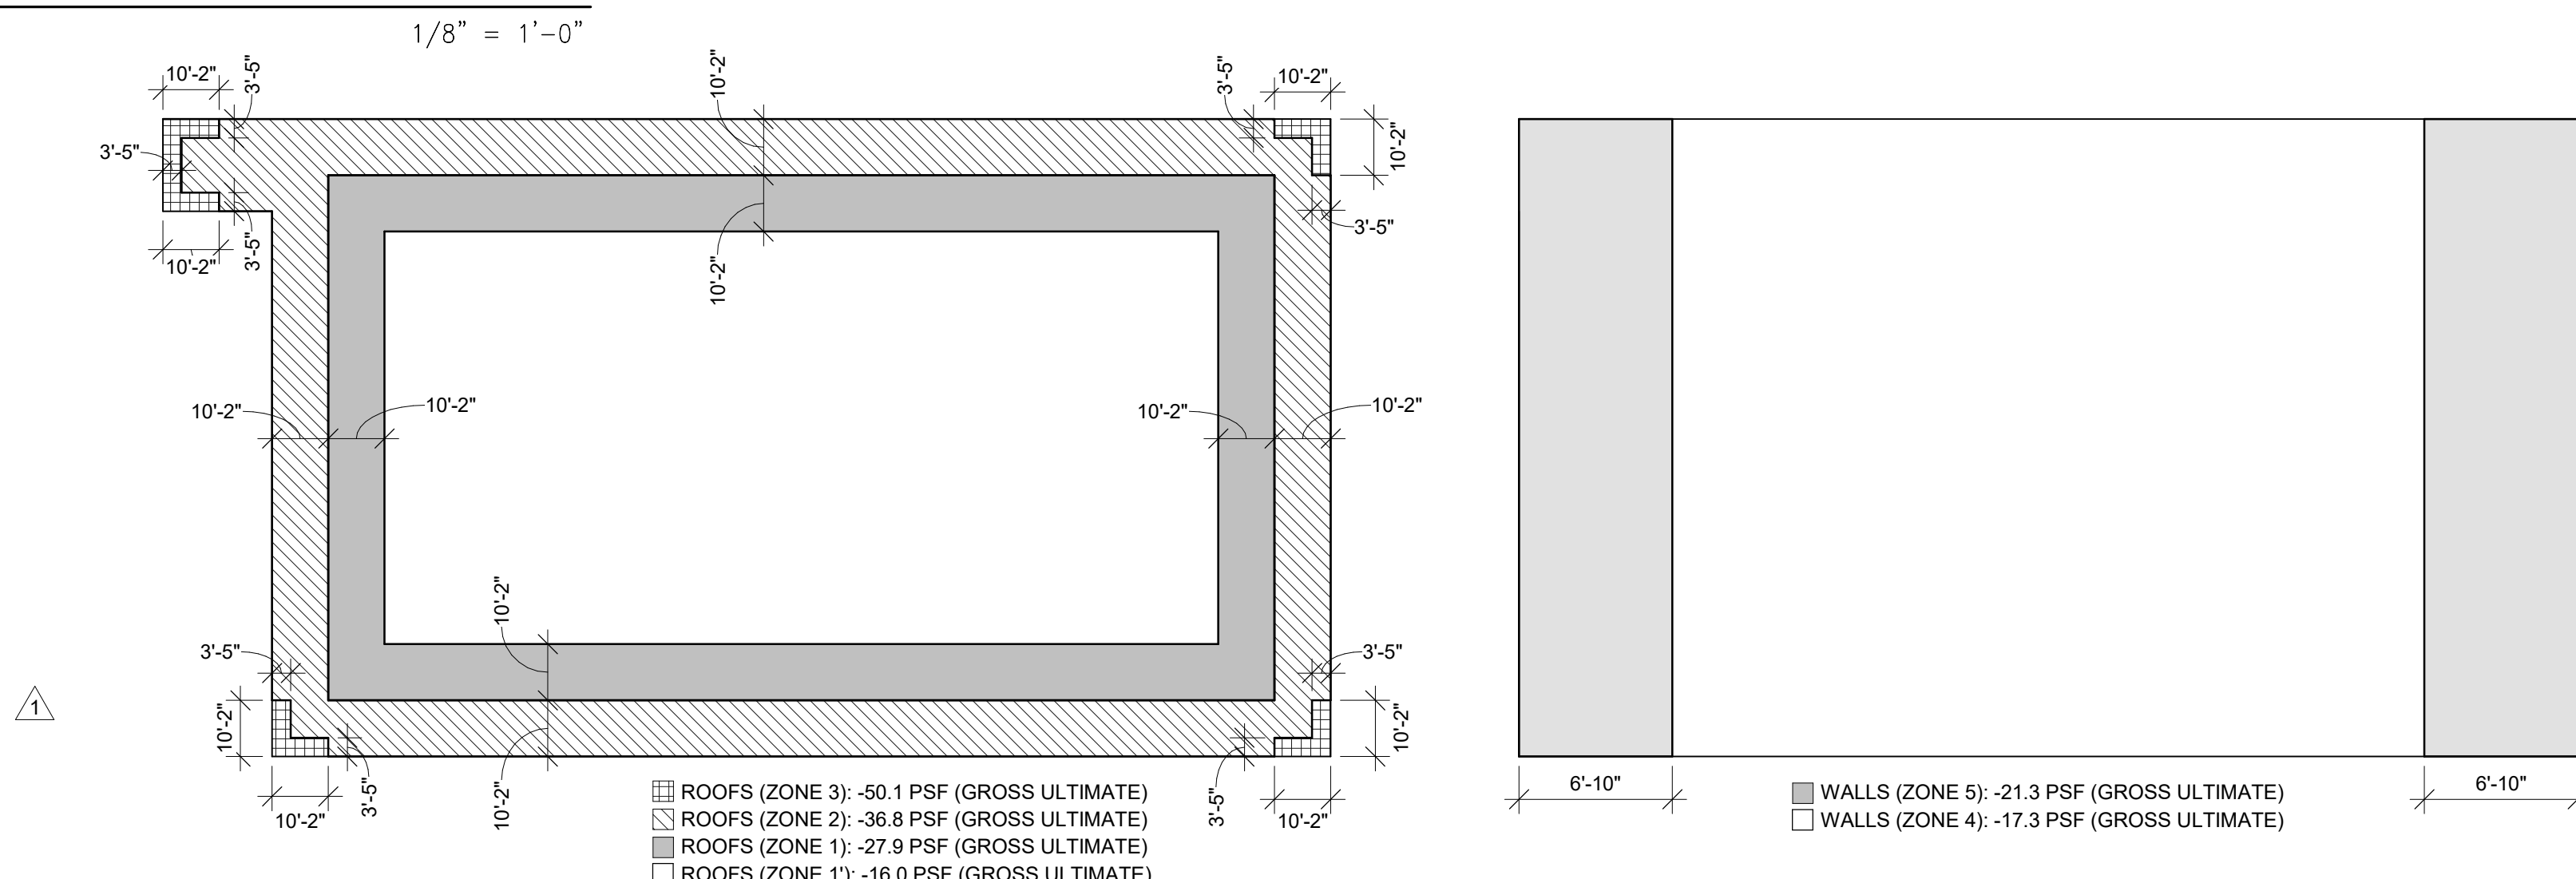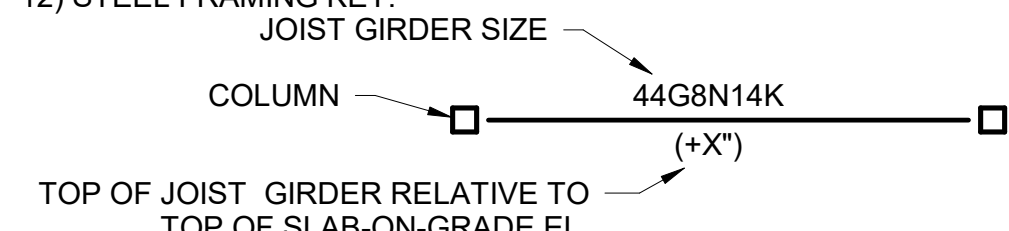

WIND UPLIFT DIAGRAM AND C&C WALL LOADS

ISSUANCE

- | | |
|------------|----------------|
| 10/02/2025 | 100% QA/QC |
| 11/07/2025 | PERMIT CYCLE 1 |
| 12/16/2025 | PERMIT CYCLE 2 |
| 01/14/2026 | PERMIT CYCLE 3 |
| 05/28/2026 | CCD 01 |

1 A

1

2

3




























4A



4

- | |
|---|
| 1 |
| 2 |
| 3 |
| 4 |
| 5 |
| 6 |
| 7 |
| 8 |
| 9 |
| 1 |
| 1 |
| 1 |


ABBREVIATIONS: EWB = EACH WAY BOTTOM

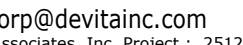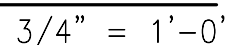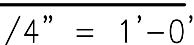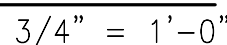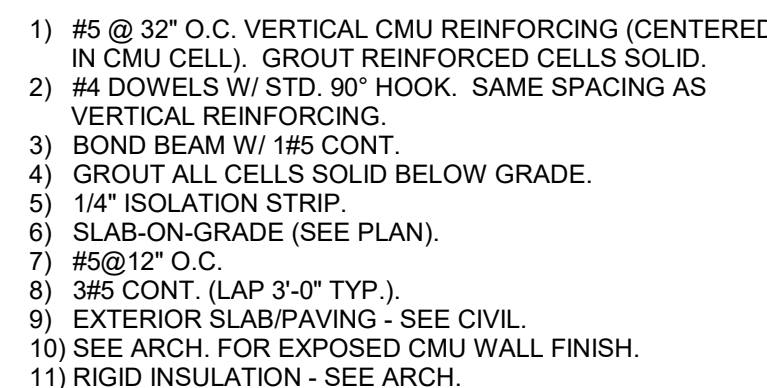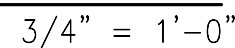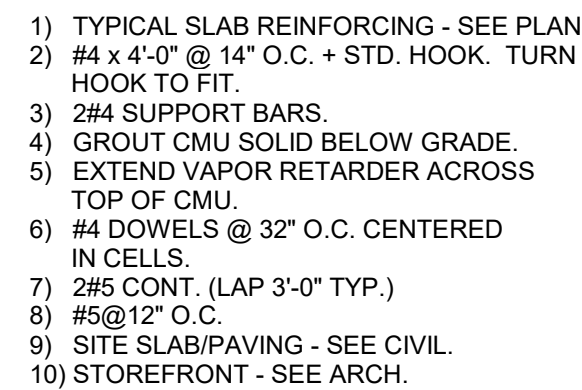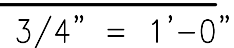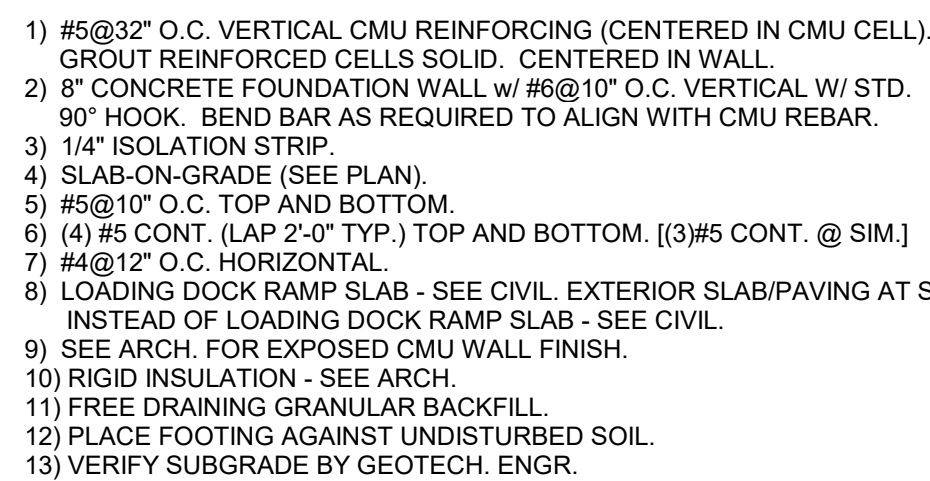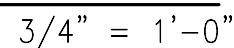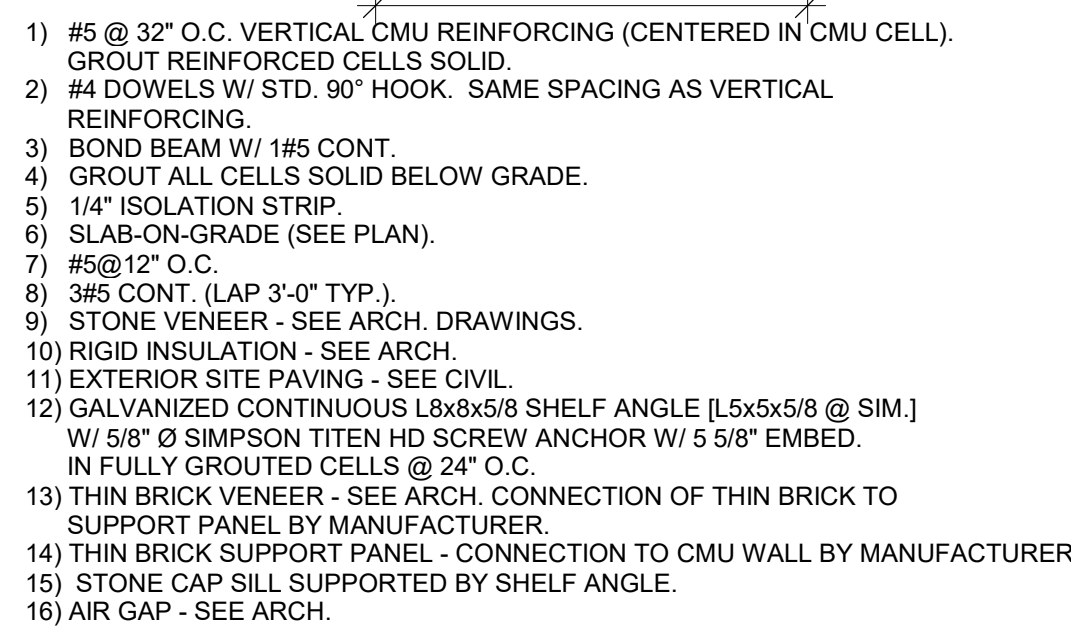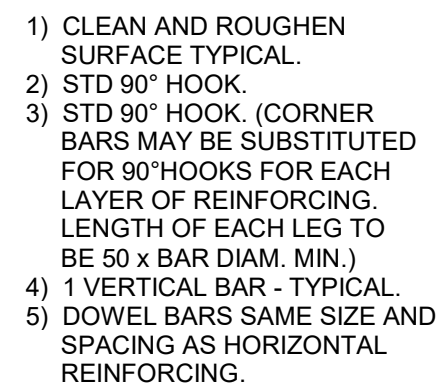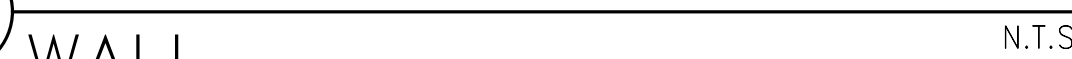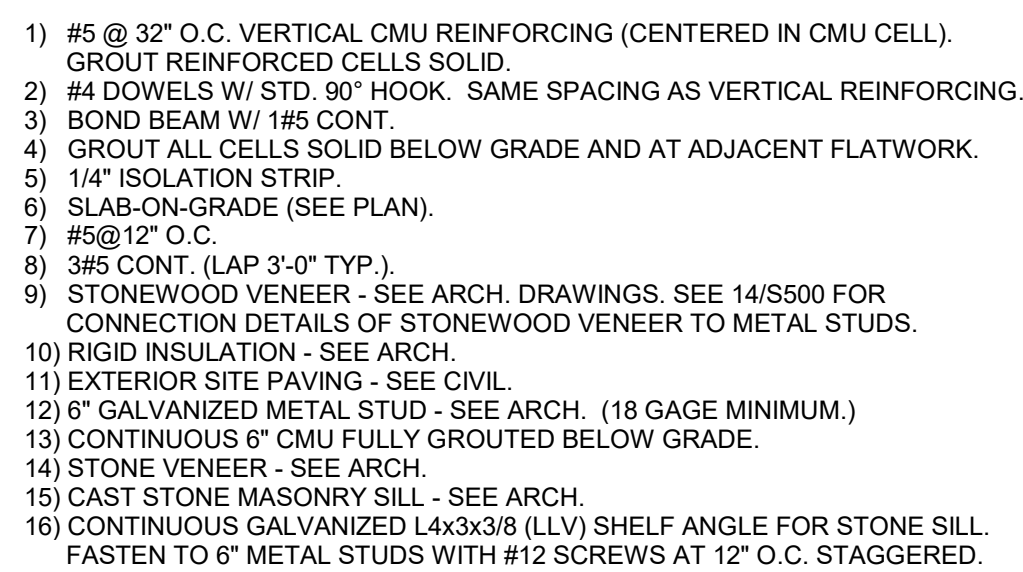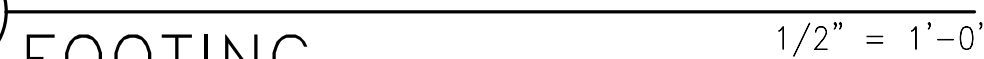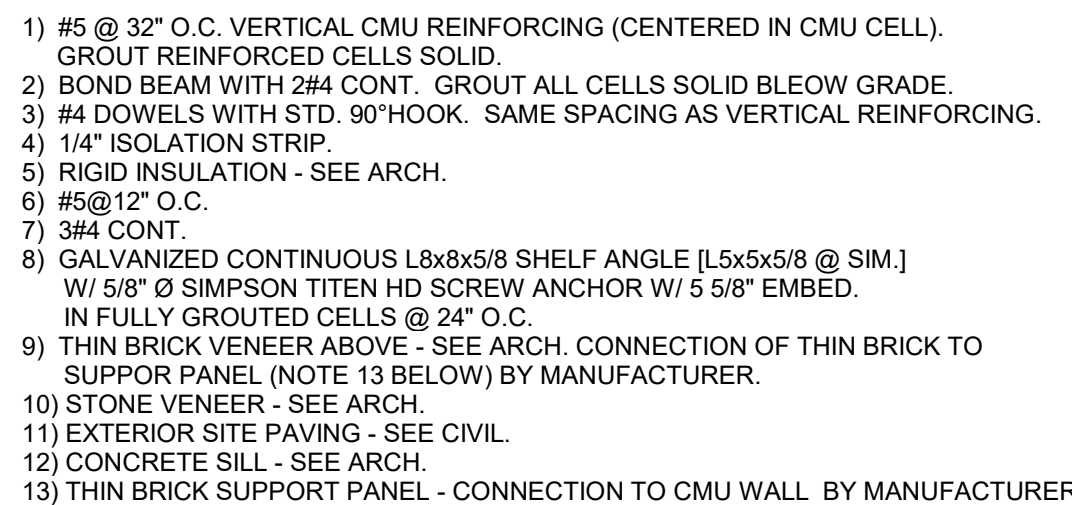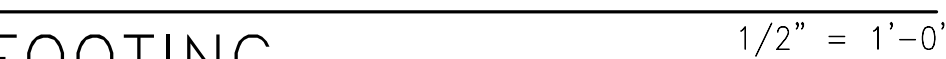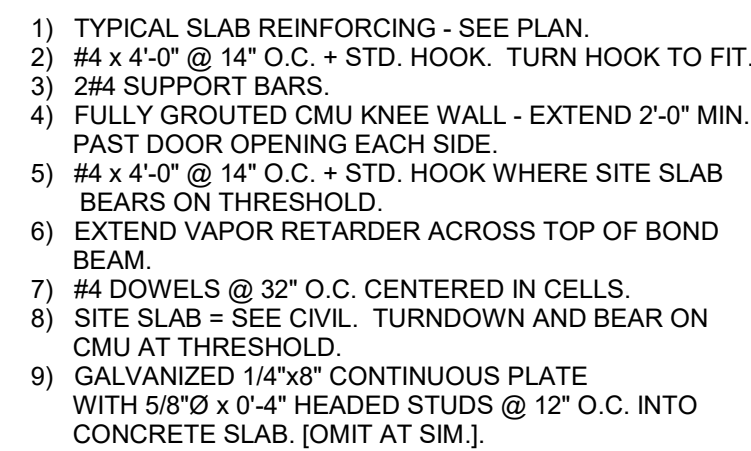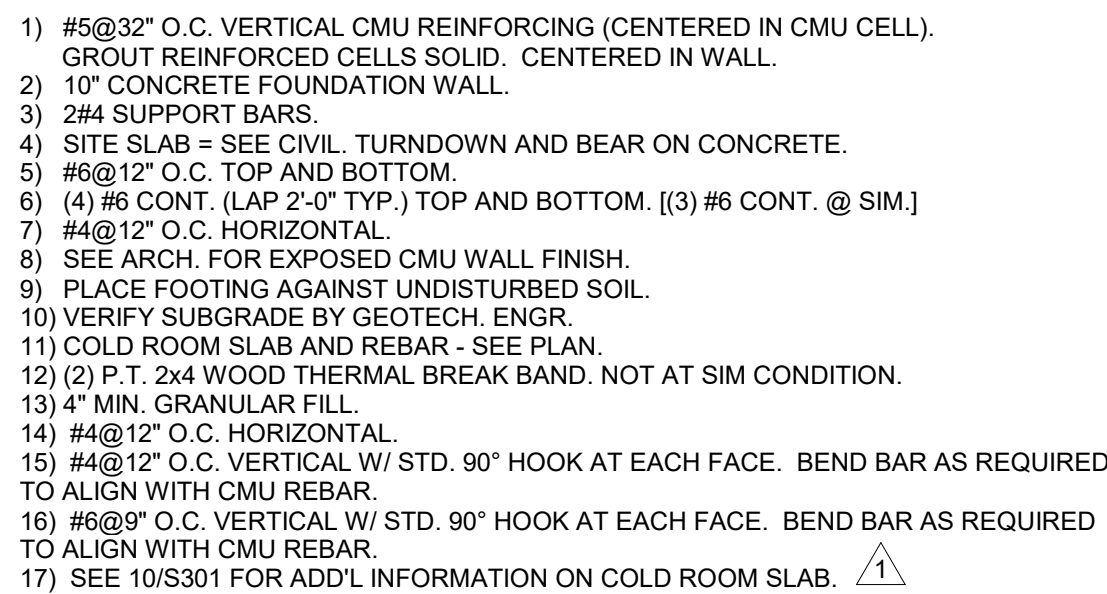

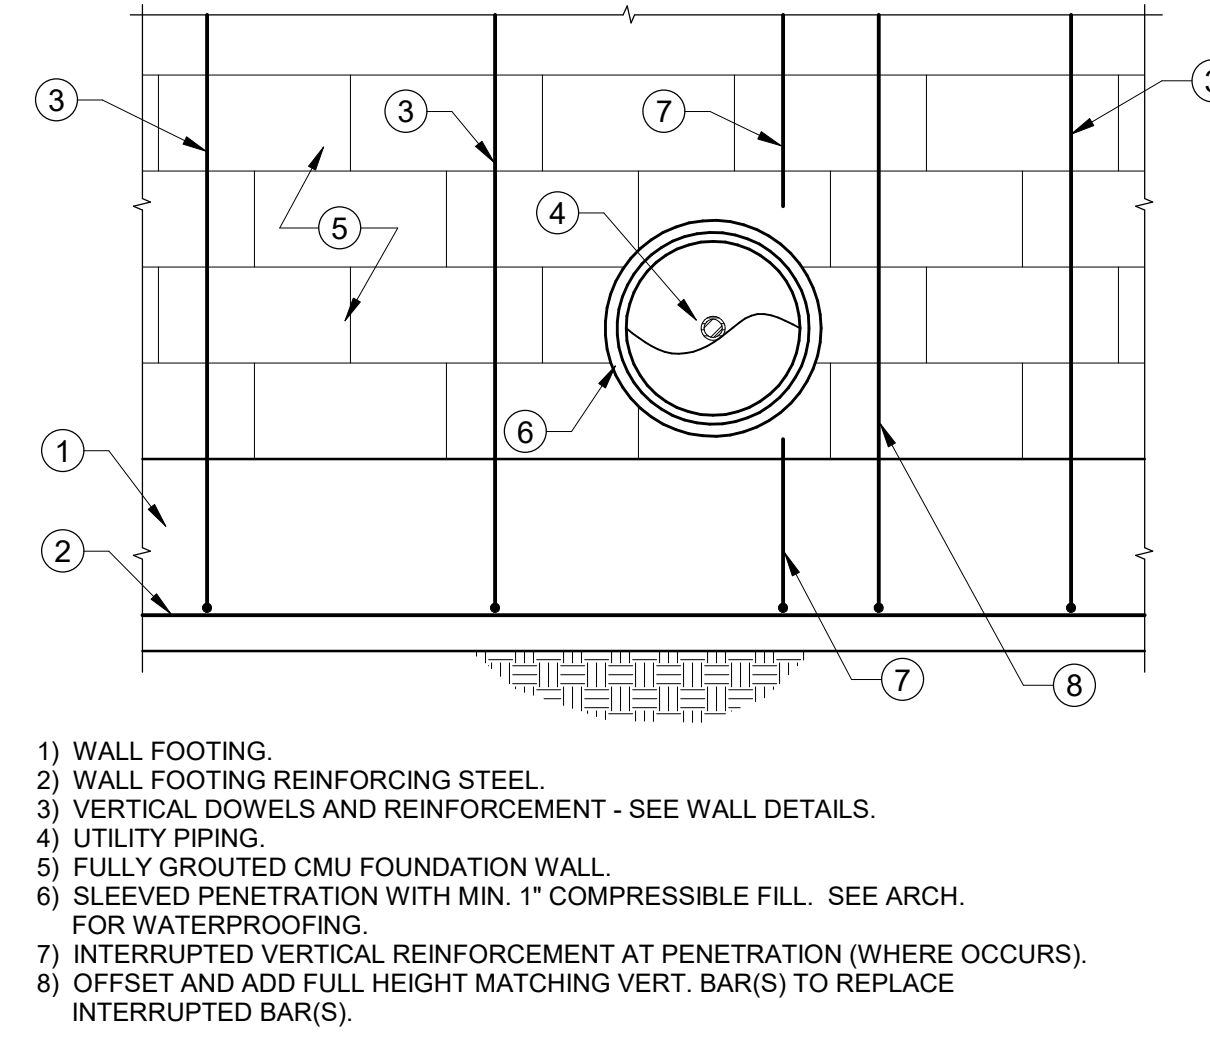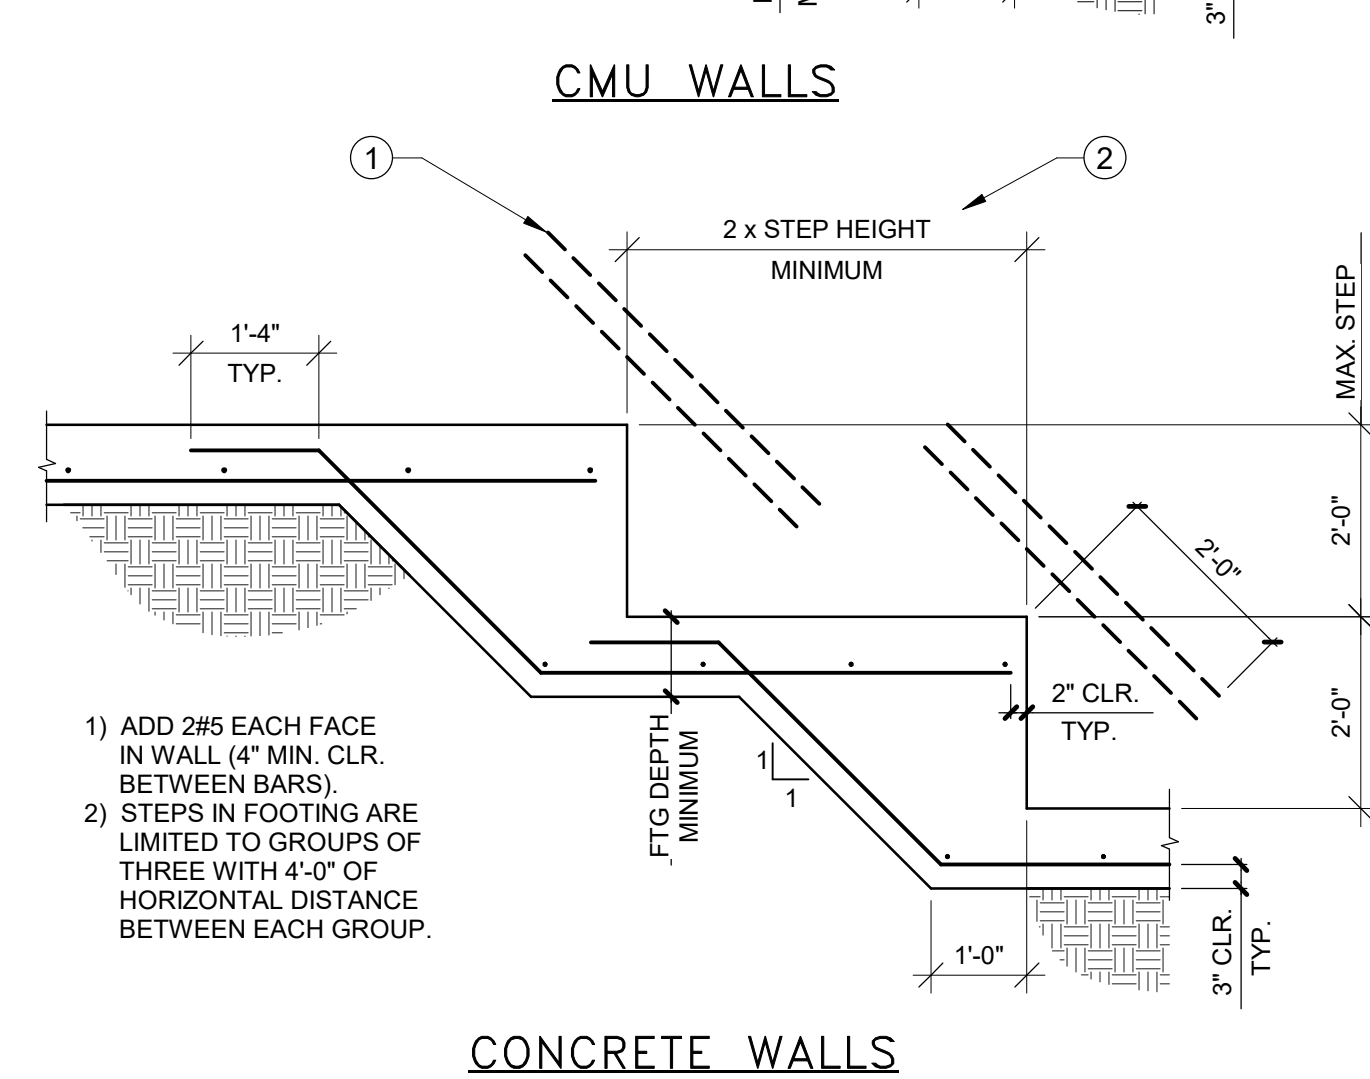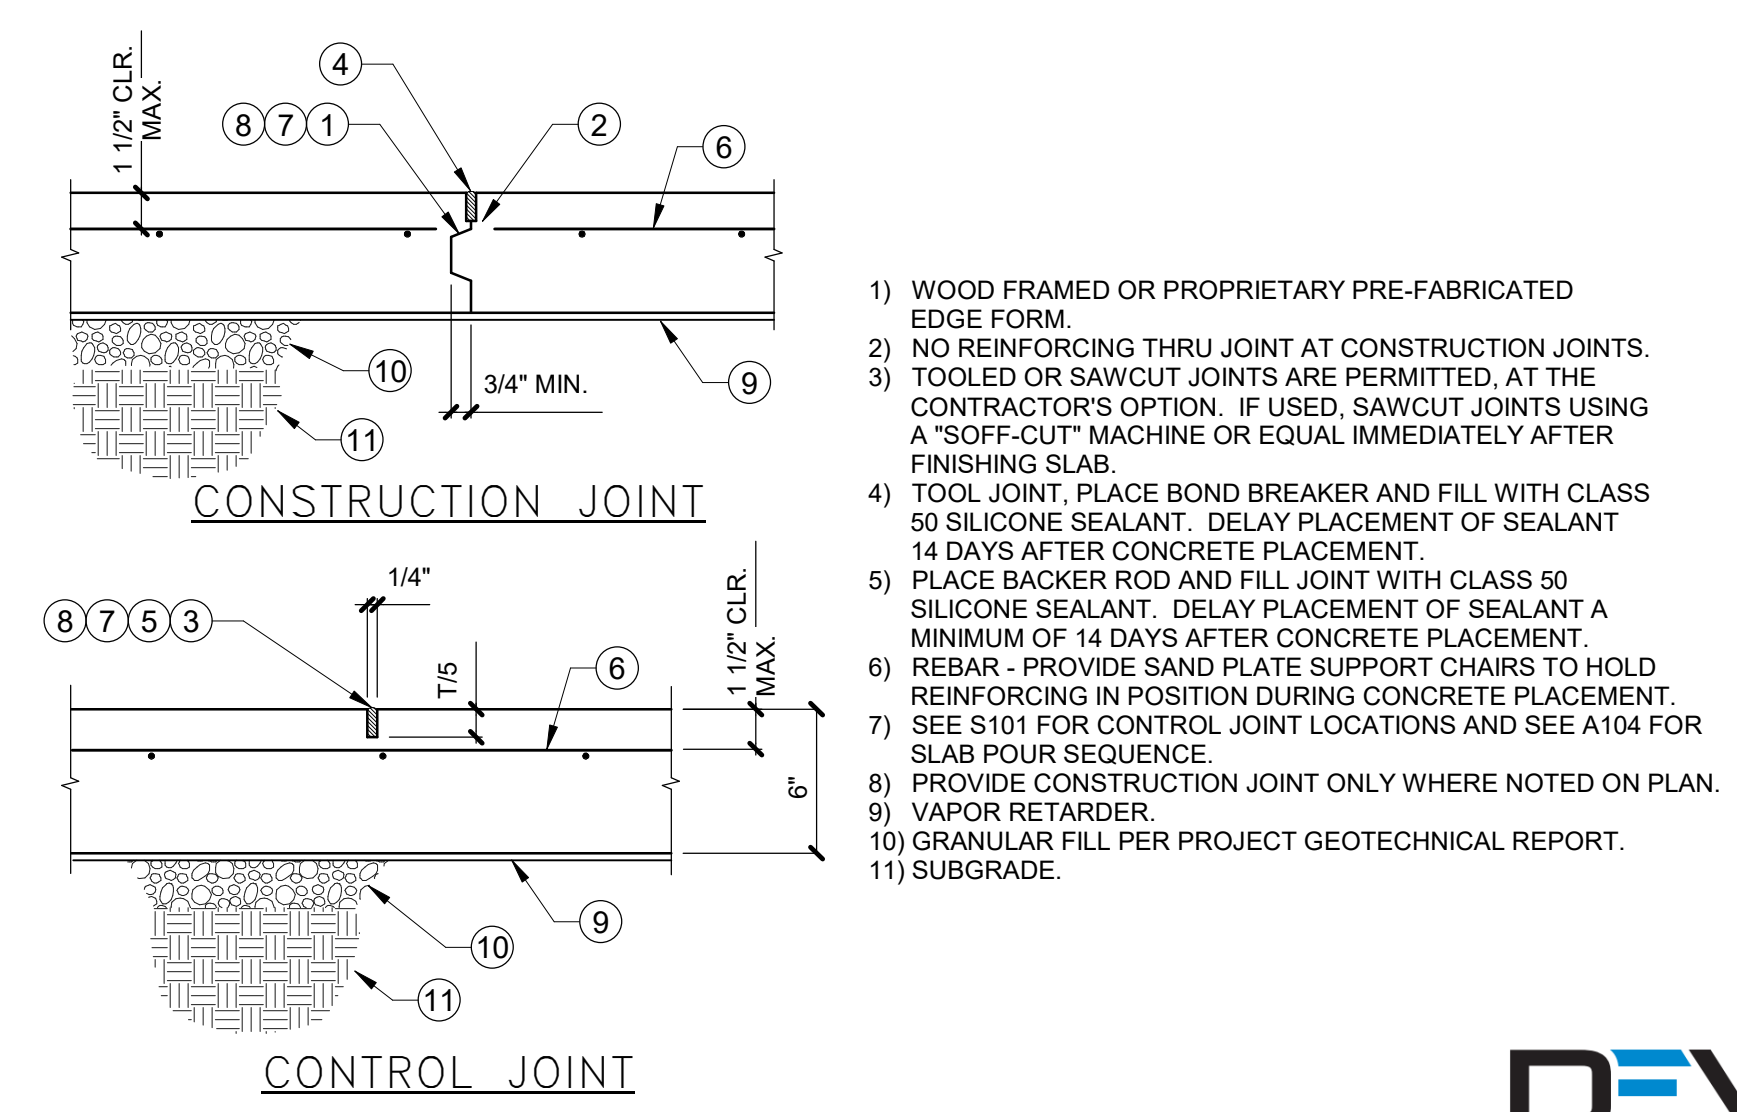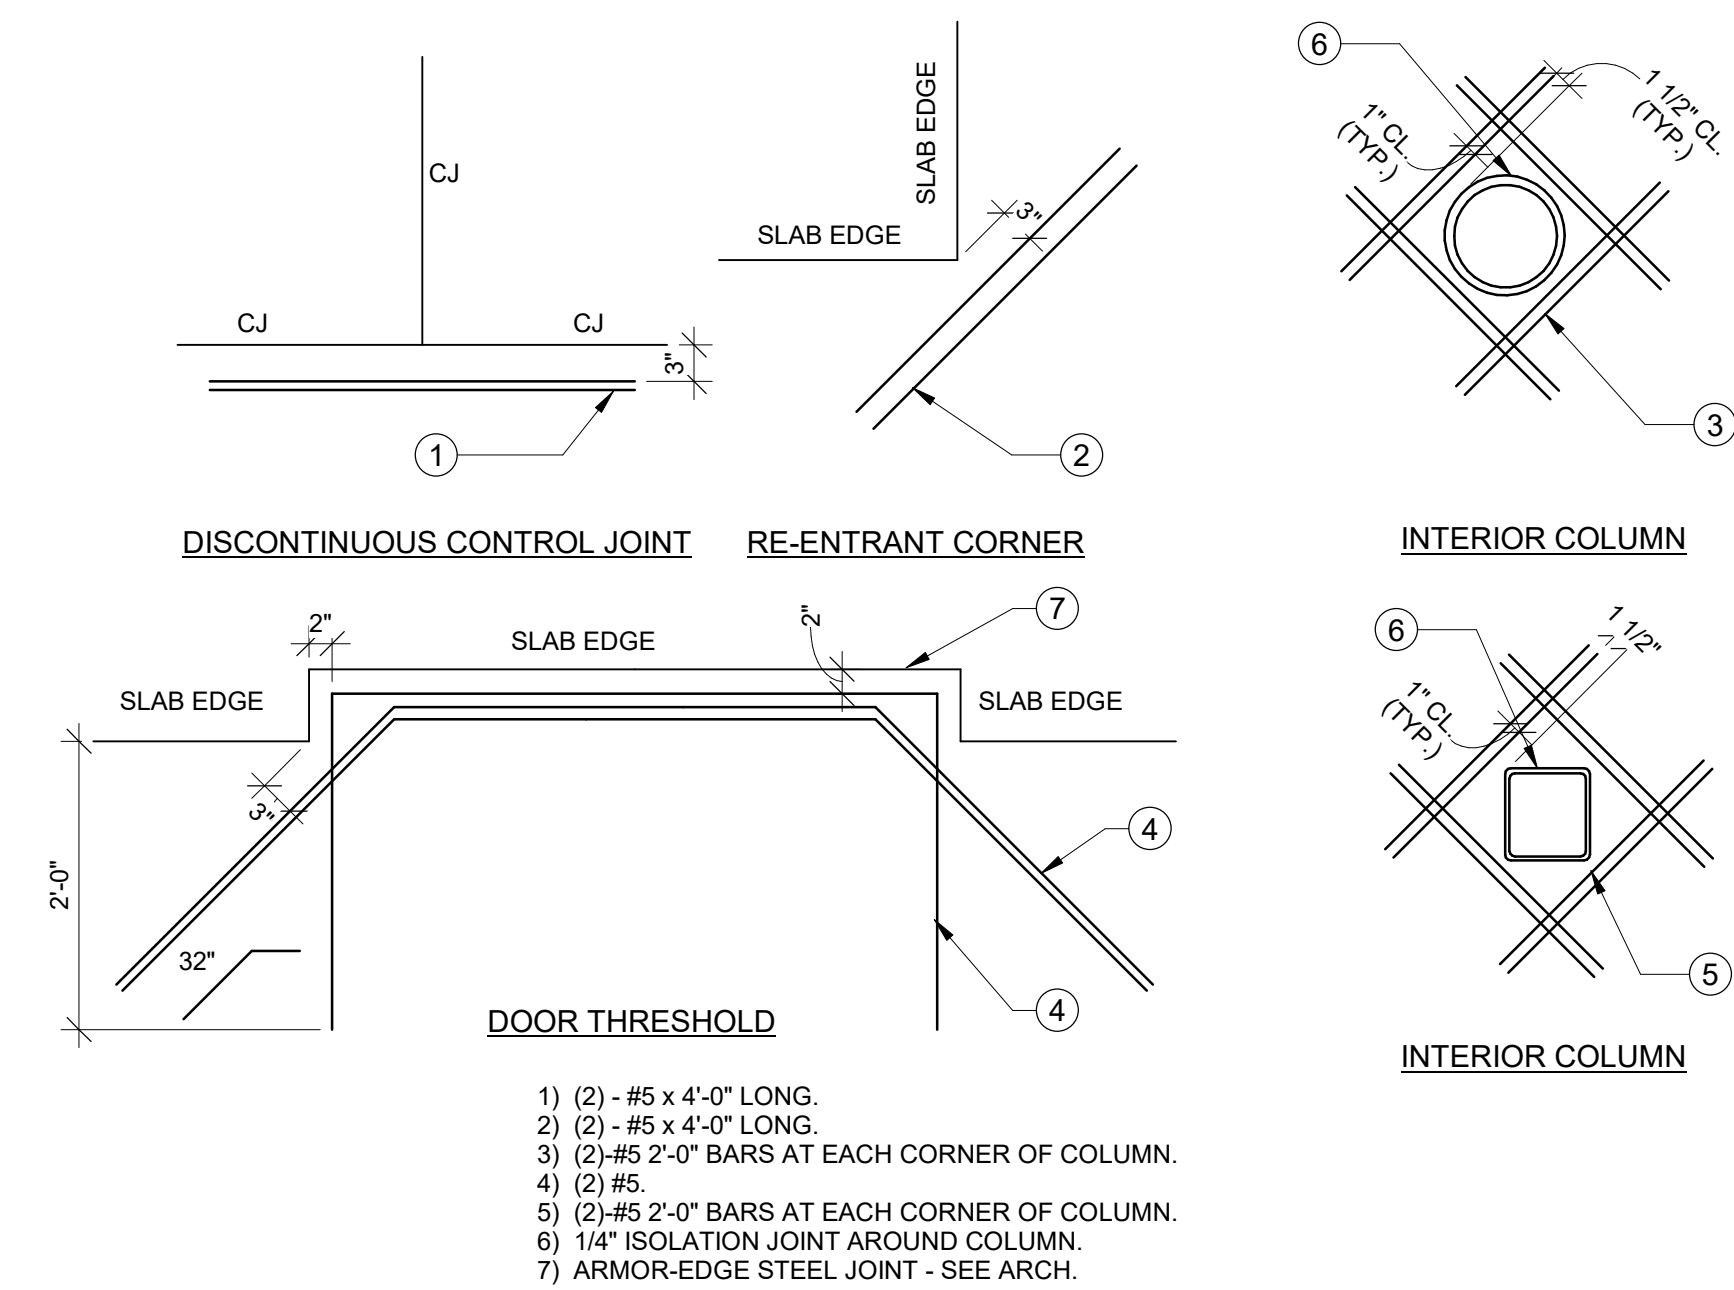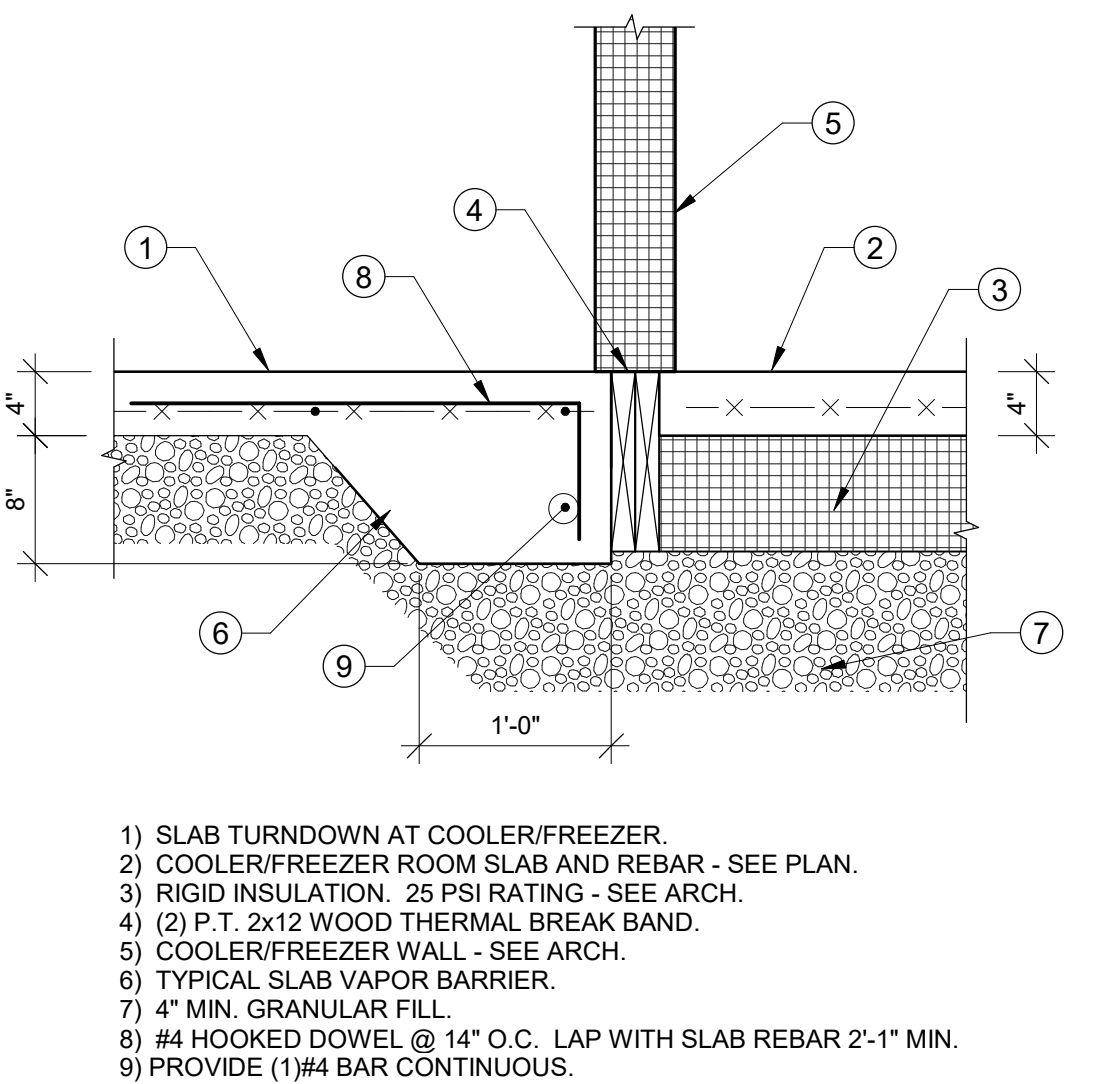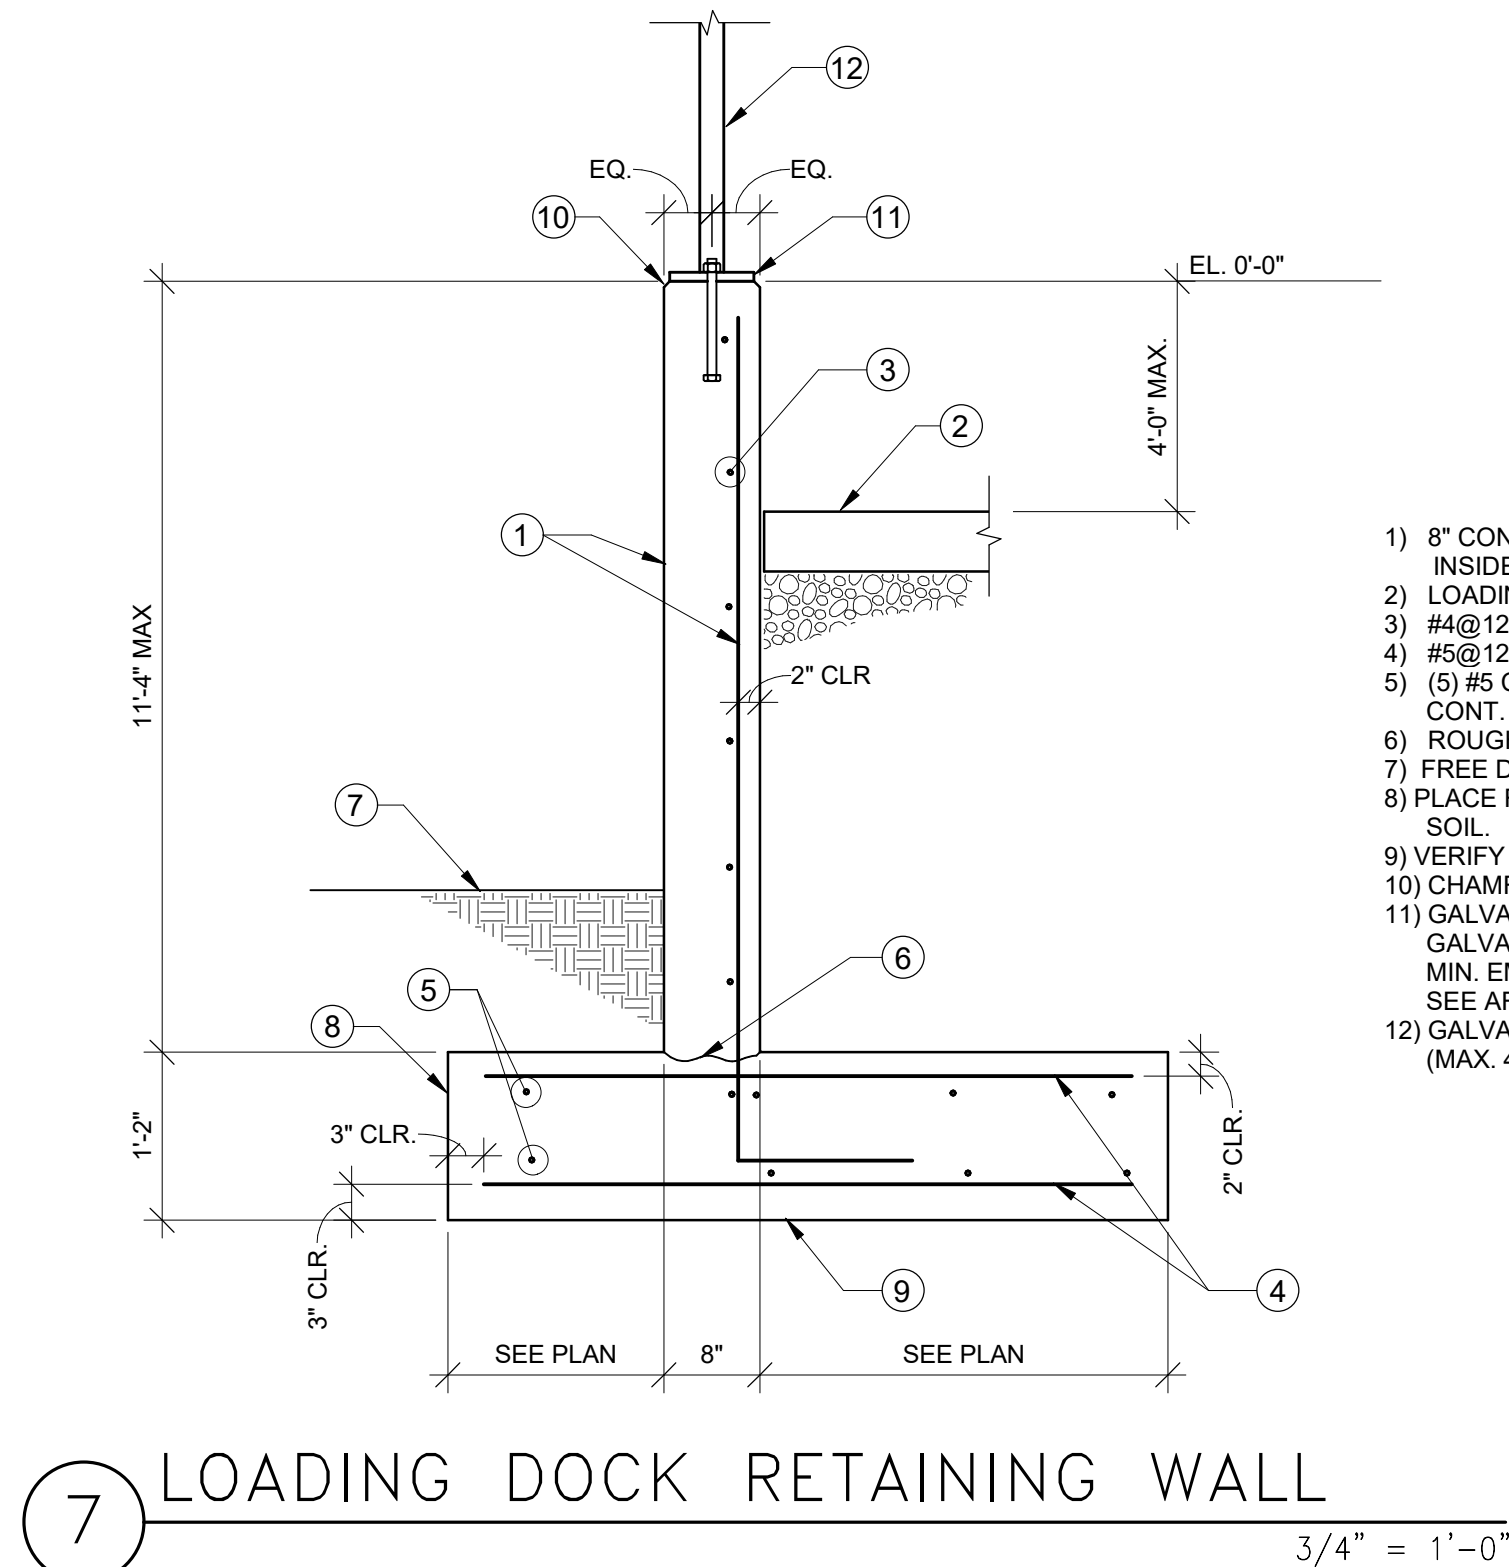

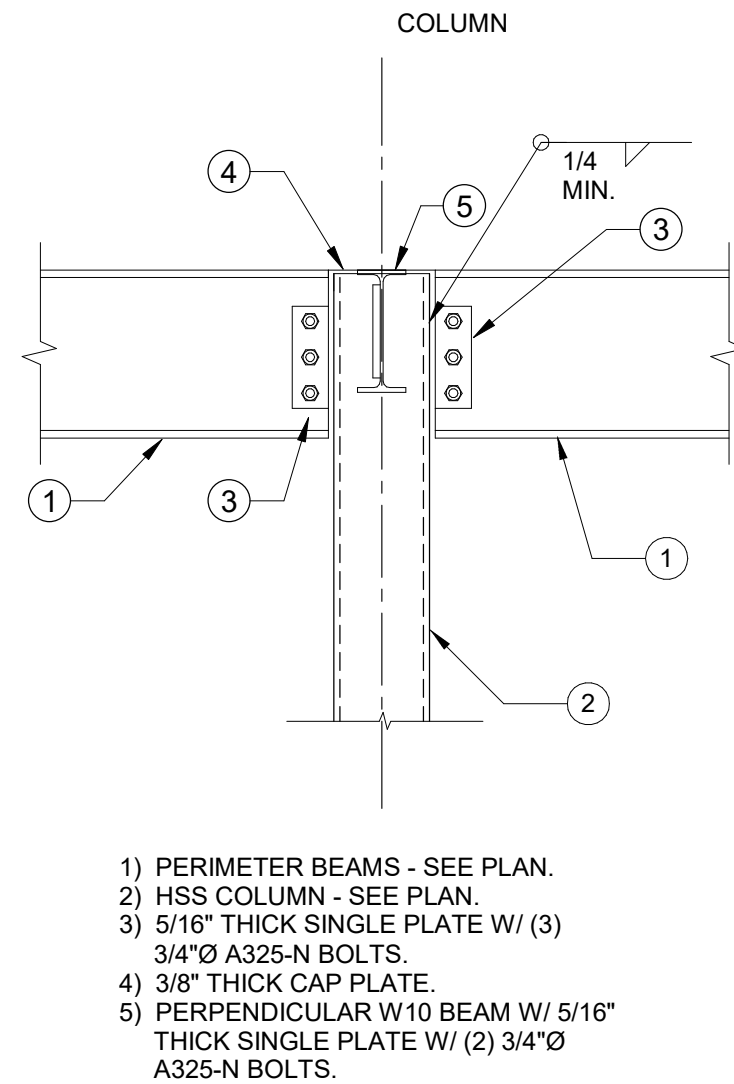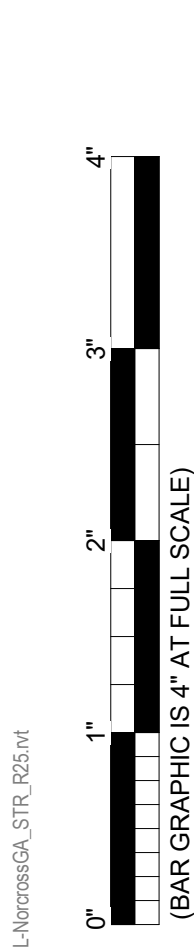

5 TYPICAL WIDE FLANGE BEAM TO COLUMN DETAIL
3/4" = 1'-0"

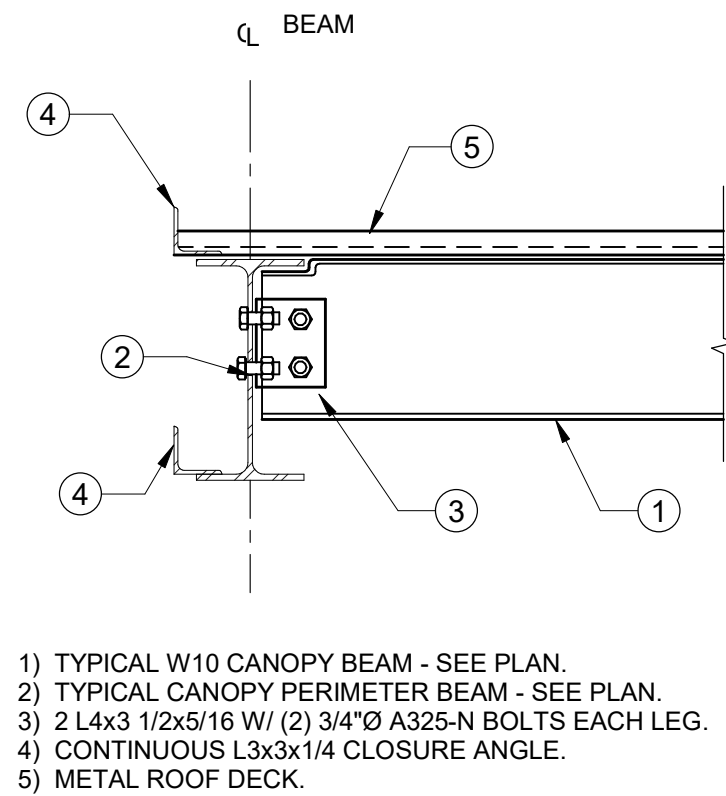


4 TYPICAL CANOPY BEAM AND EDGE DETAIL
1" = 1'-0"


MARK	BASE PLATE SIZE			ANCHOR BOLT			REMARKS
	WIDTH	LENGTH	THICKNESS	NO.	SIZE	*LENGTH	
BP-1	13"	13"	1"	4	3/4"Ø	9"	
BP-2	13"	15"	3/4"	4	3/4"Ø	9"	GALV. PLATE & ANCHORS
BP-3	16"	16"	1 1/4"	4	3/4"Ø	9"	
BP-4	15"	15"	3/4"	4	3/4"Ø	9"	GALV. PLATE & ANCHORS
BP-5	11"	11"	3/4"	4	3/4"Ø	9"	

* LENGTH INDICATED IS MINIMUM EMBEDMENT.


3 COLUMN BASE PLATE SCHEDULE
N.T.S.

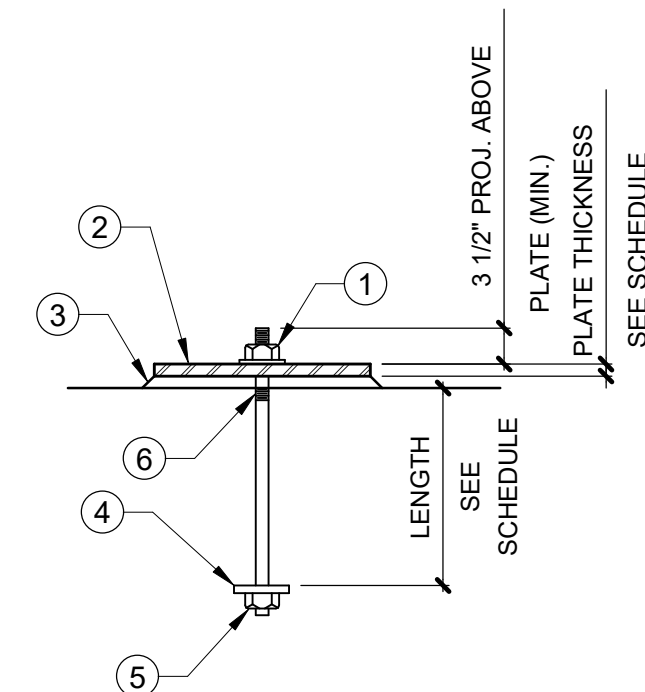


2 BASE PLATE SETTING DETAIL
N.T.S.

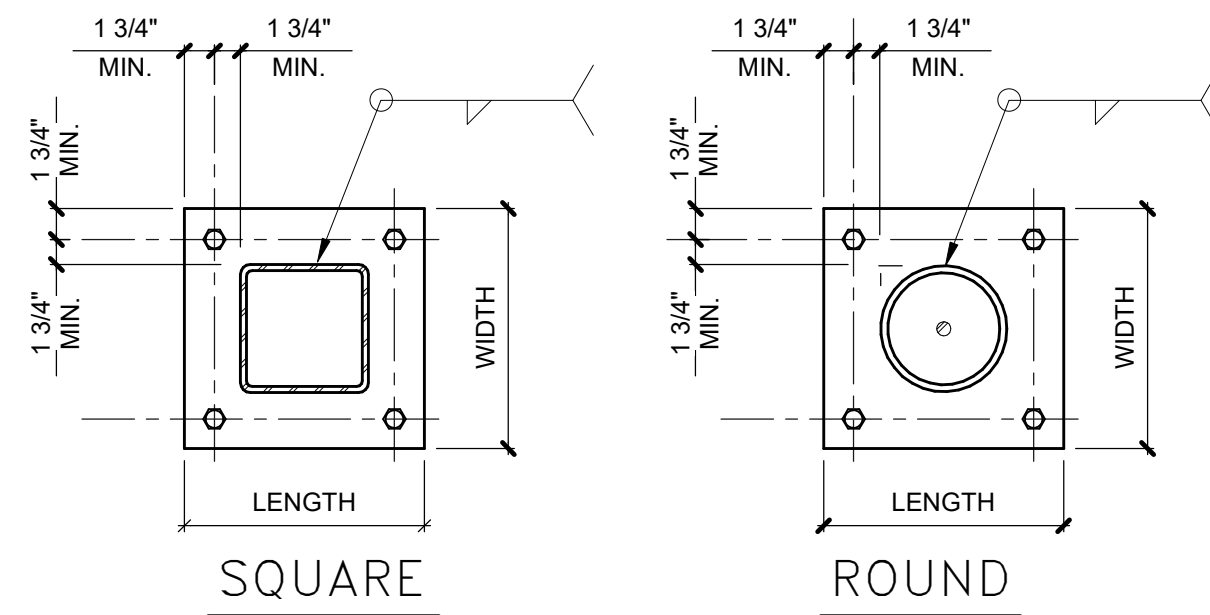


1 SQUARE OR ROUND HSS COLUMN BASE PLATE
N.T.S.

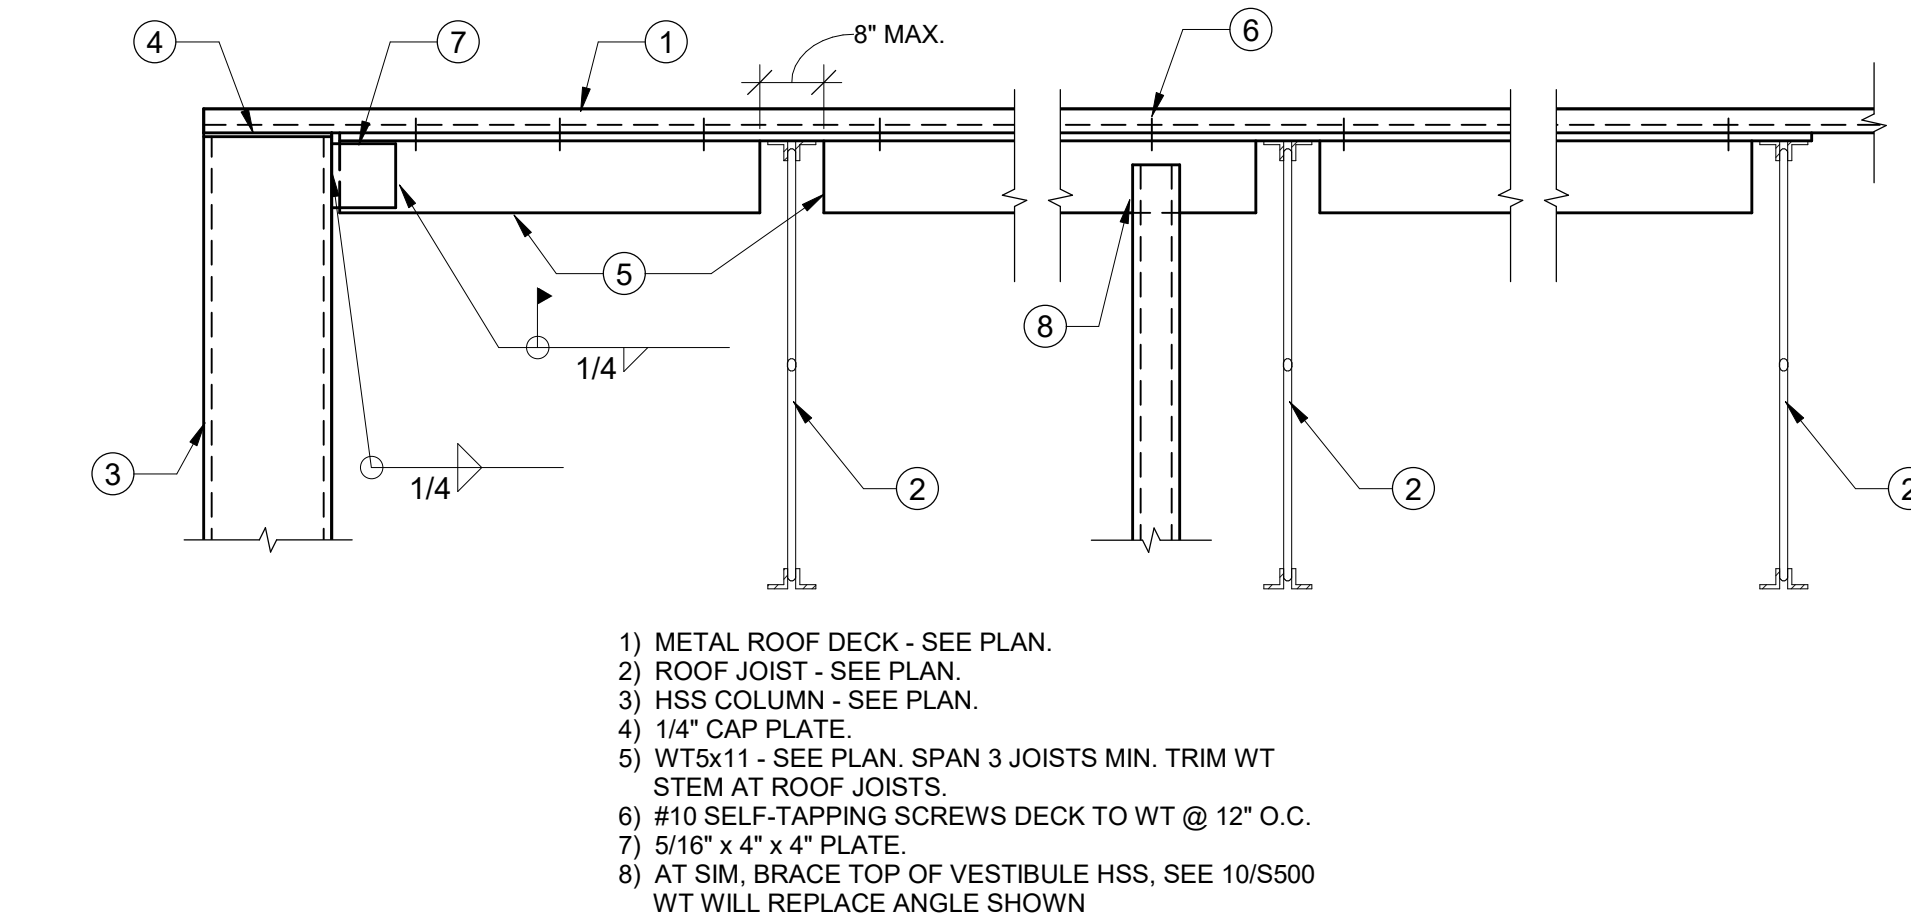


9 WT BRACE AT HSS POST
1" = 1'-0"

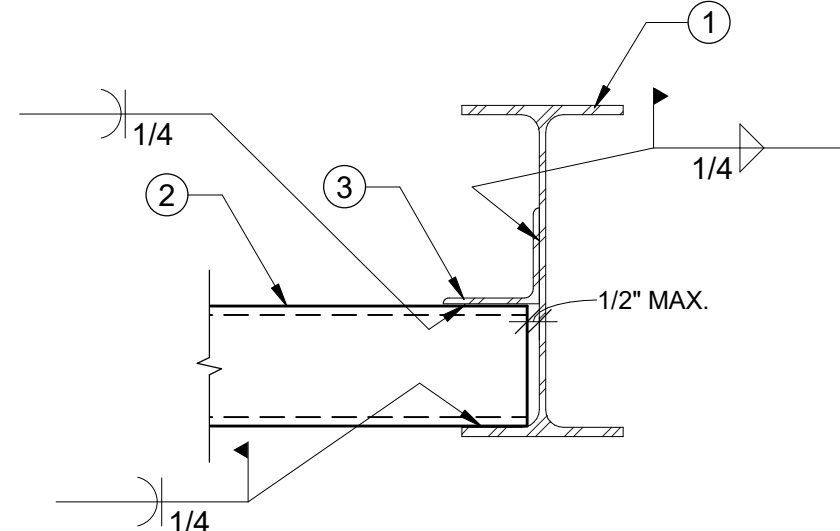


8 HSS TO W-BEAM CONNECTION
1 1/2" = 1'-0"

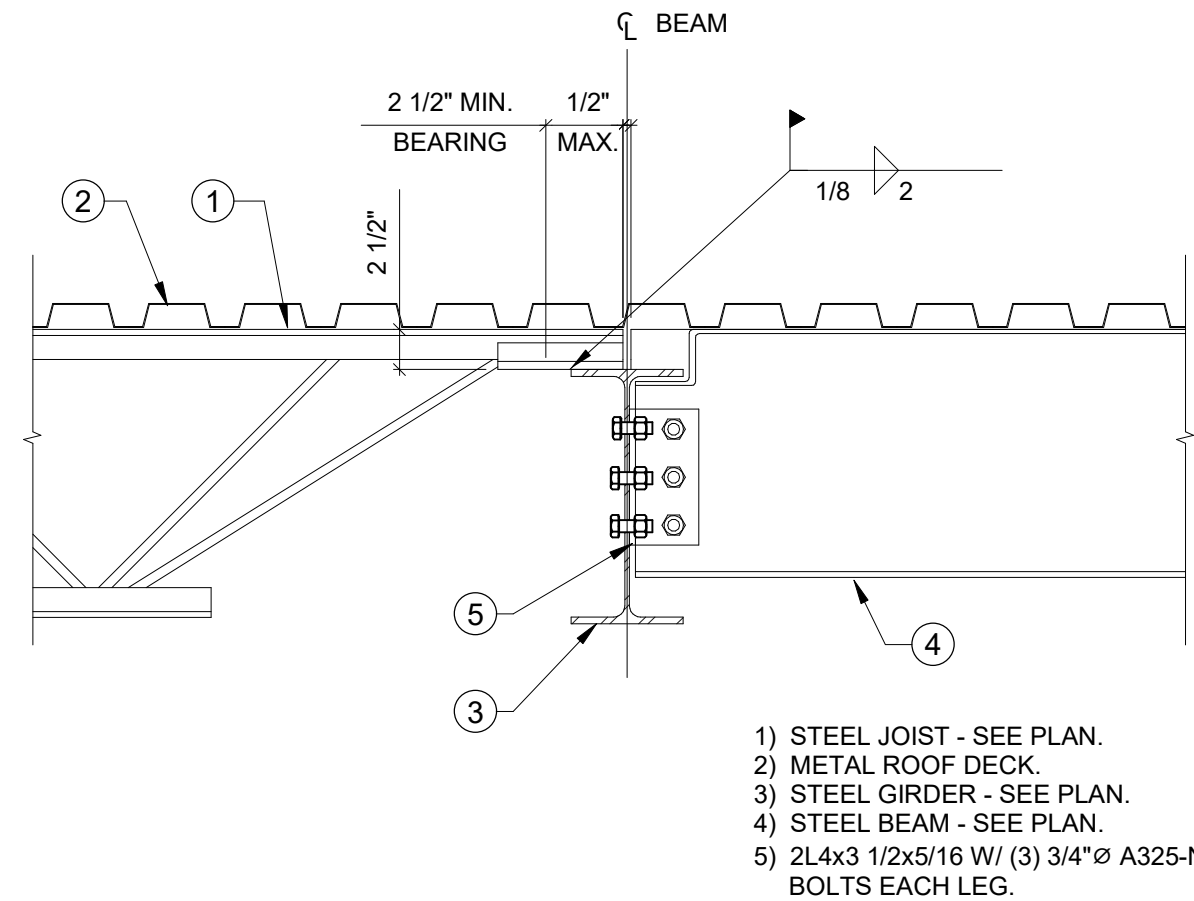


7 "K" JOIST AND STEEL BEAM BEARING ON STEEL GIRDER
N.T.S.

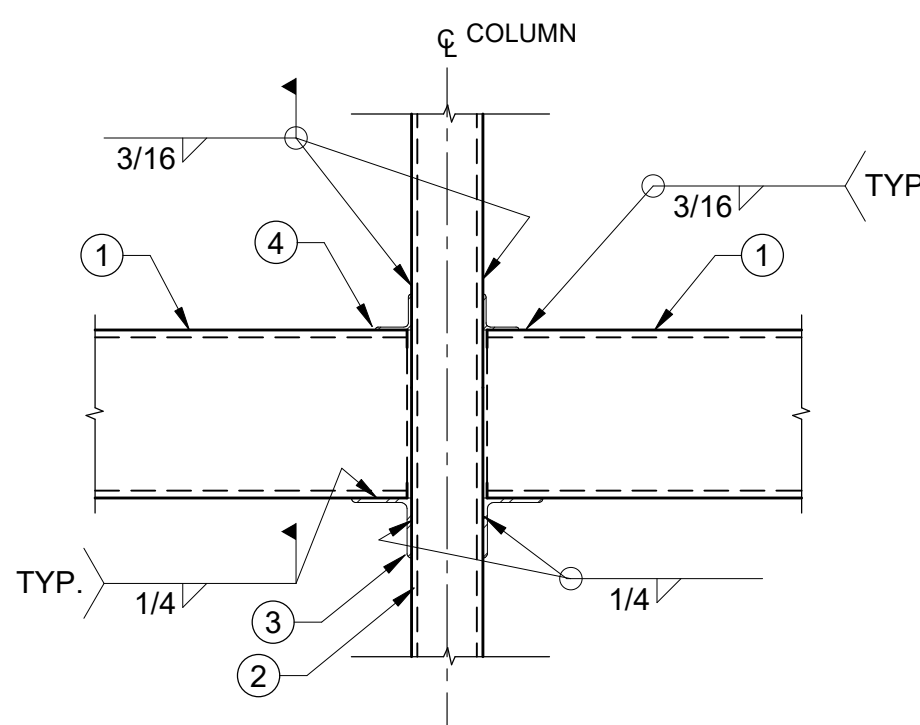

6 TYPICAL HSS TO COLUMN CONNECTION
3/4" = 1'-0"

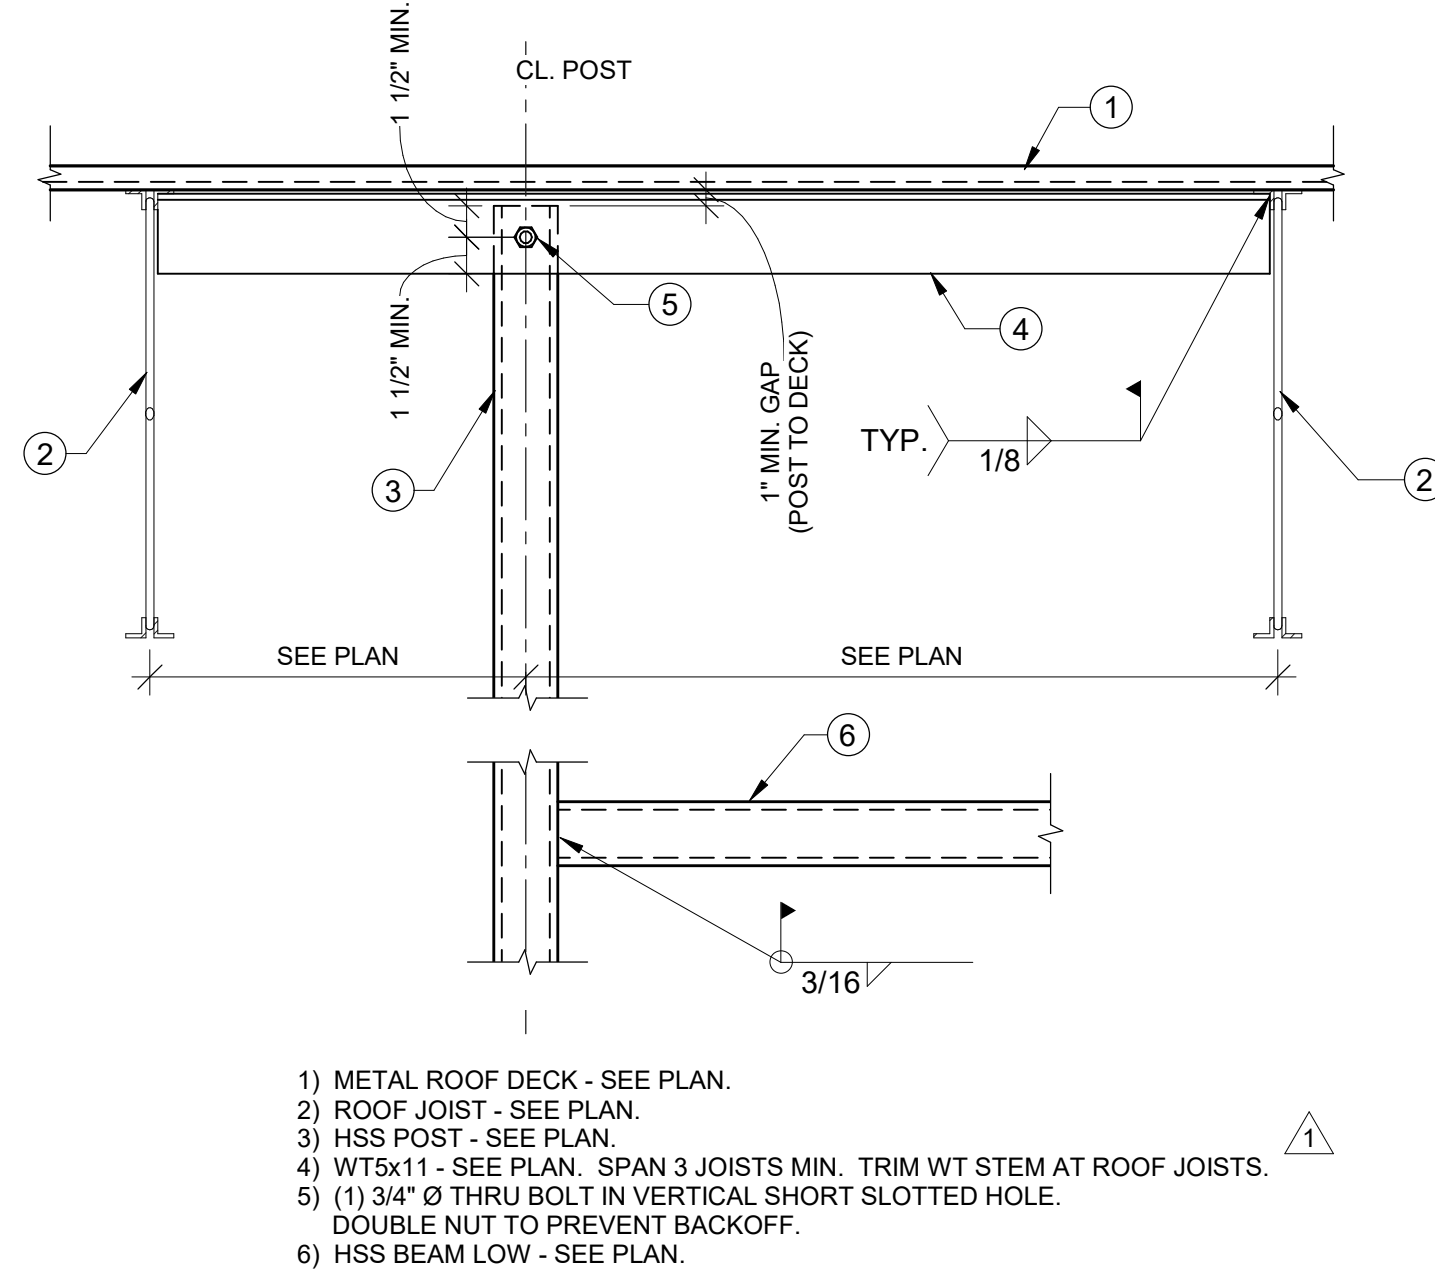

10 TOP OF VESTIBULE POST BRACING
1" = 1'-0"

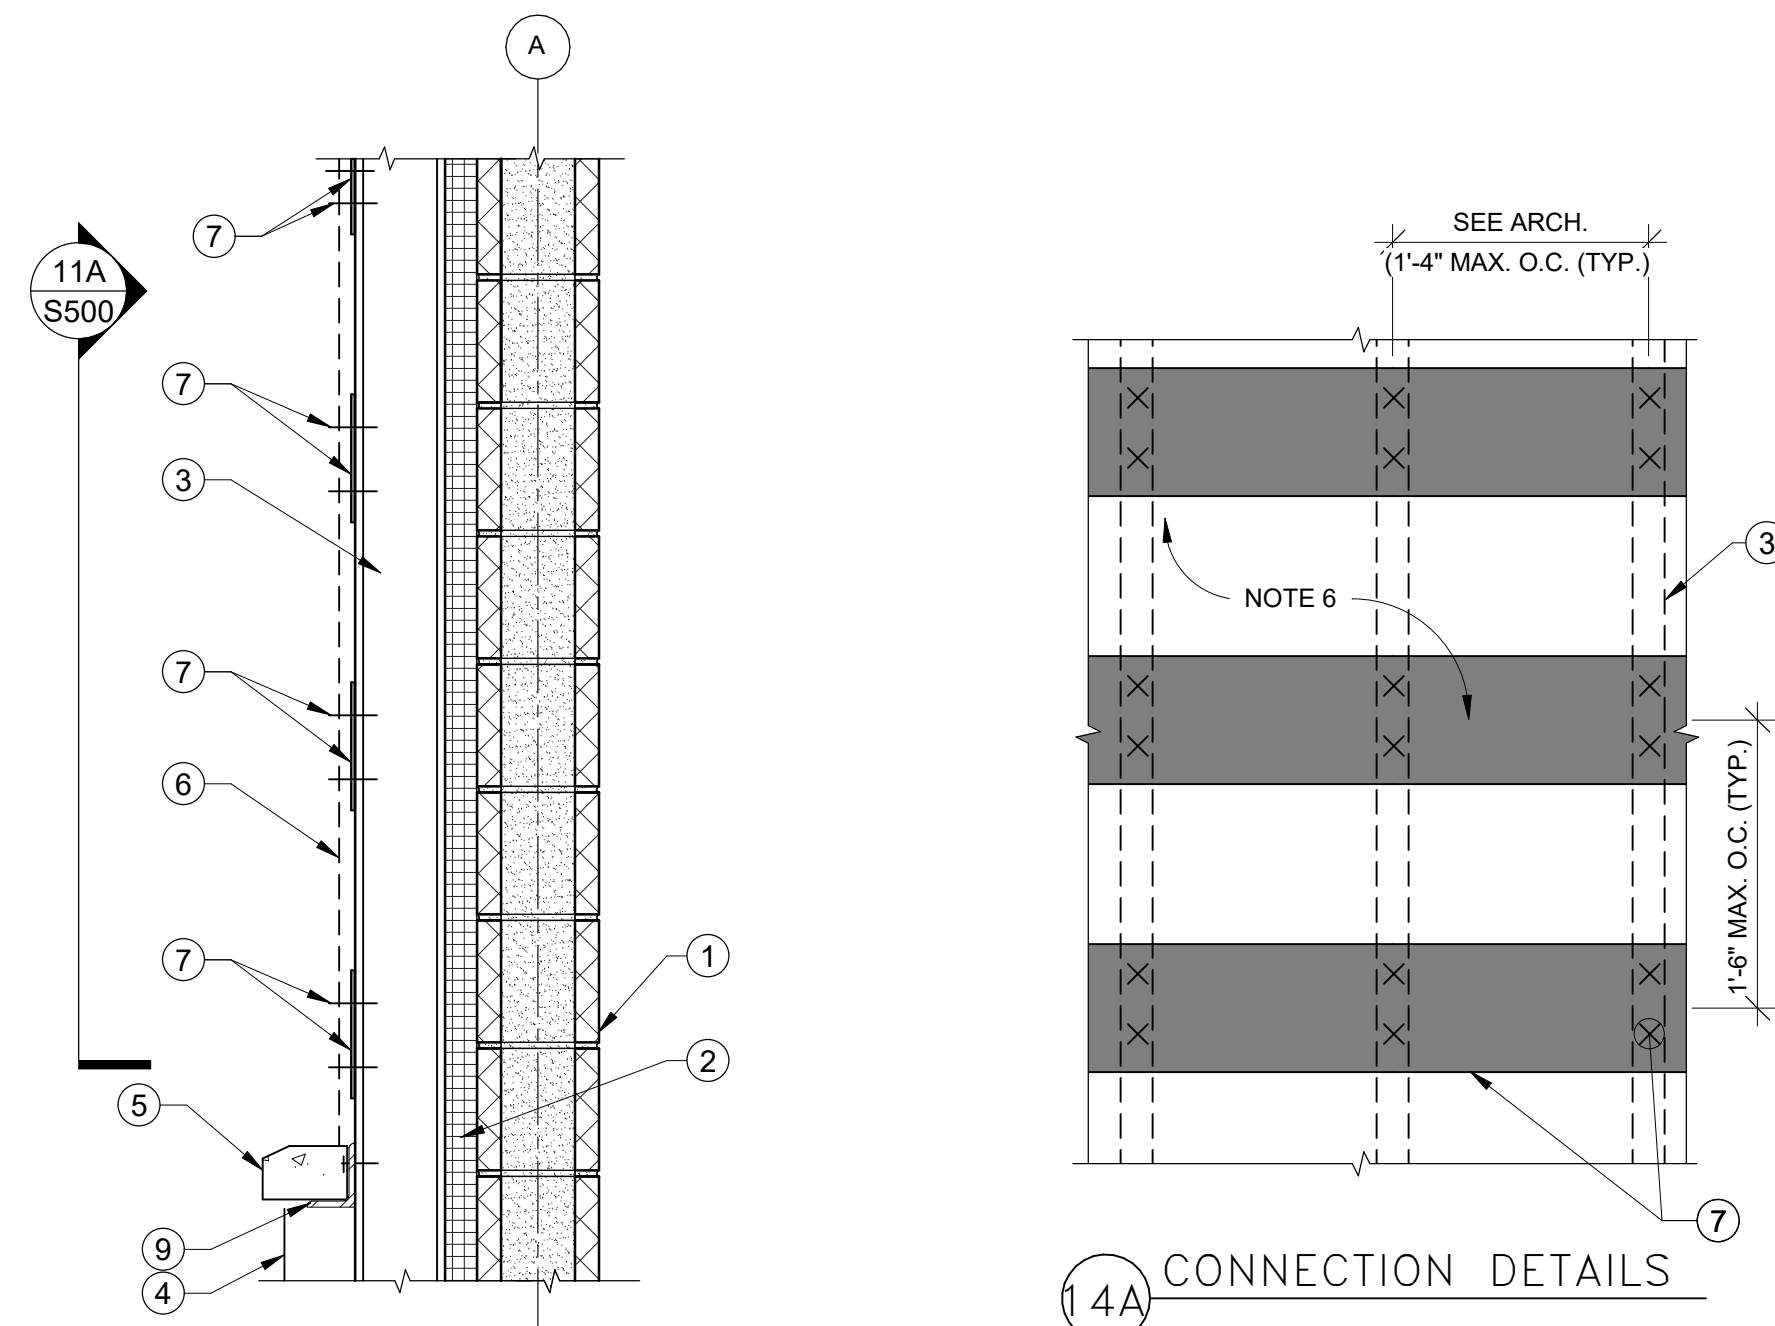

11 STONEWOOD VENEER TO STUD WALL CONNECTION DETAILS
1" = 1'-0"

