

A ANNUNCIATOR IS A TYPICAL LAYOUT. THE CONTRACTOR IS RESPONSIBLE FOR THE DESIGN AND INSTALLATION OF THE ANNUNCIATOR IN ACCORDANCE WITH THE SPECIFICATIONS AND ADOPTED CODES AND STANDARDS. CONTRACTOR SHALL SUBMIT SHOP DRAWINGS TO AHJ.

(Y) YELLOW LED
 (R) RED LED
 (G) GREEN LED
 (K) KEY SWITCH


A. REFER TO SHEET E000 FOR LEGENDS, ABBREVIATIONS AND GENERAL NOTES.




- Ⓡ HEAT DETECTOR
- Ⓡ SMOKE DETECTOR
- Ⓡ PULL STATION
- Ⓡ FLOW SWITCH

- Ⓨ TAMPER SWITCH
- Ⓨ POST INDICATOR VALVE
- Ⓨ DUCT SMOKE DETECTOR
- Ⓨ TROUBLE

© POWER

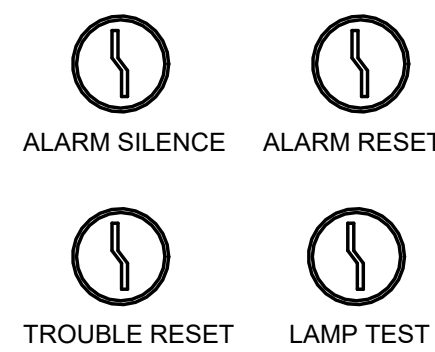

A. RISER IS DIAGRAMMATICAL AND ONLY SHOWS TYPICAL LAYOUT OF APPLIANCES, DEVICES AND EQUIPMENT. THE CONTRACTOR IS RESPONSIBLE FOR THE DESIGN AND INSTALLATION OF THE SYSTEM IN ACCORDANCE WITH THE SPECIFICATIONS AND ADOPTED CODES AND STANDARDS. CONTRACTOR SHALL SUBMIT SHOP DRAWINGS TO AHJ.

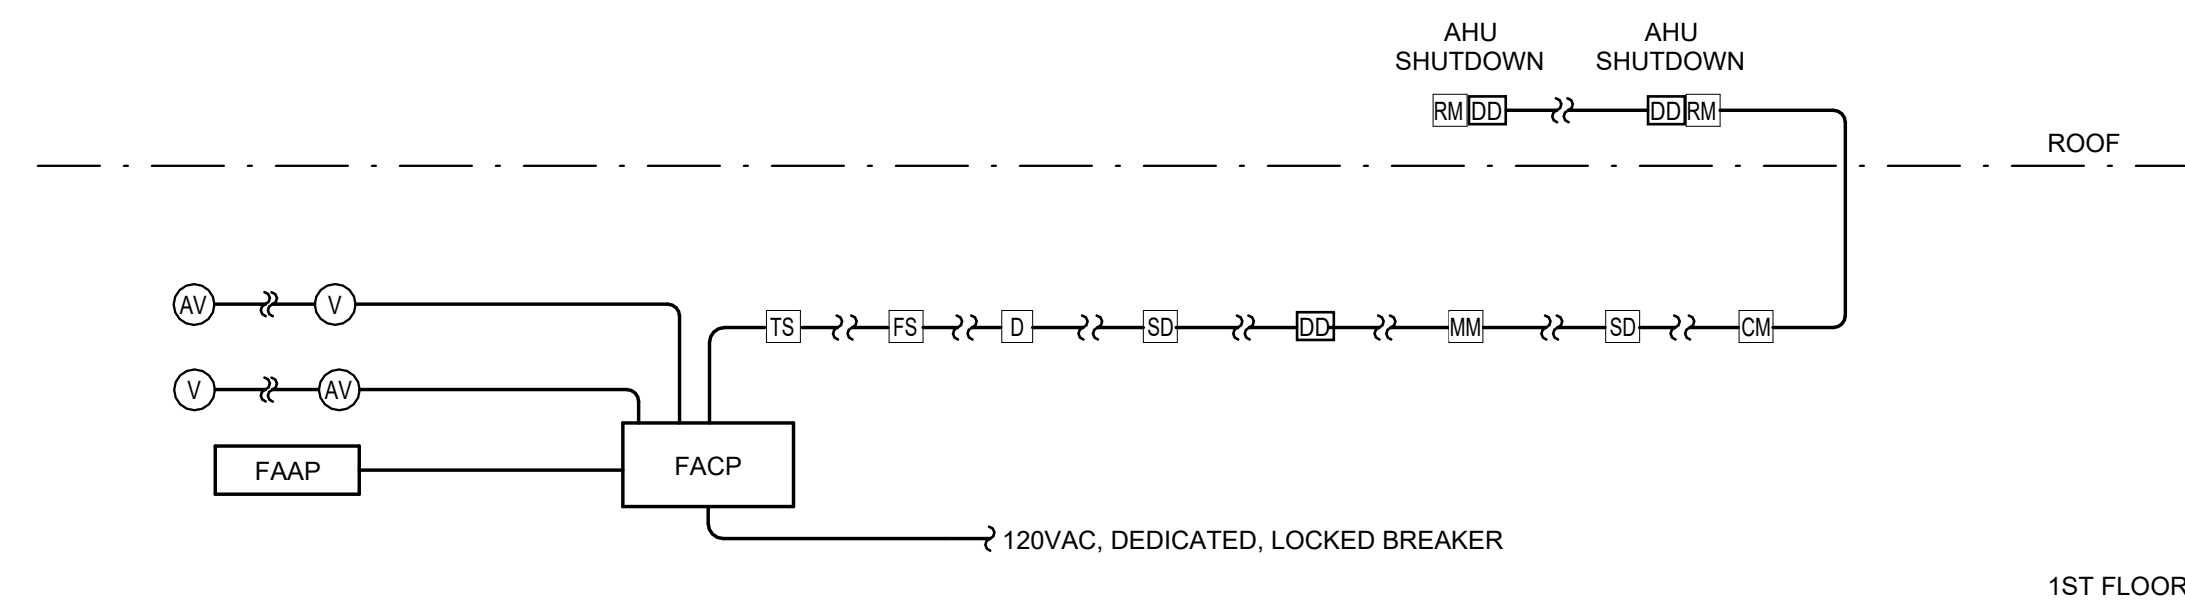

NO SCALE

NO SCALE